



VISTA 01

ESC 1/25

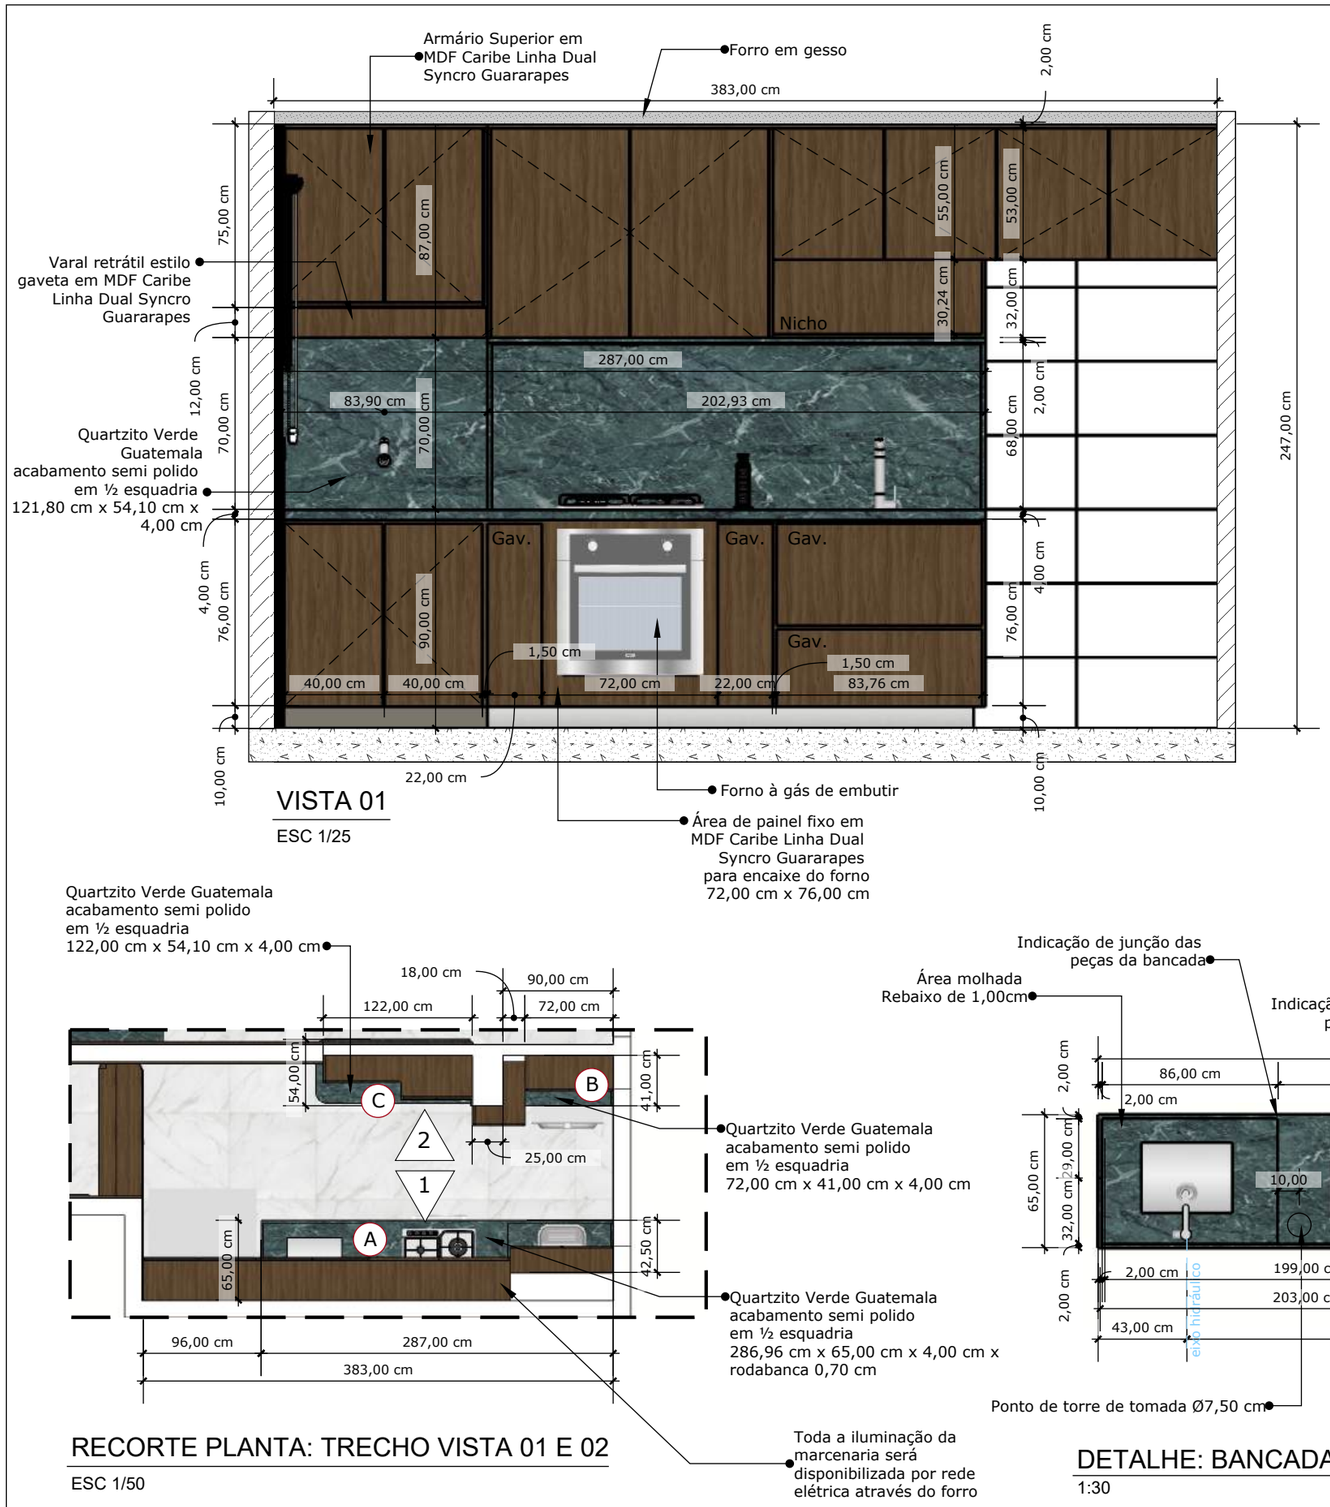


PERSPECTIVA: VISTA 01

1:30

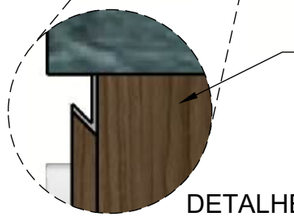

DETALHE PUXADOR

1/50

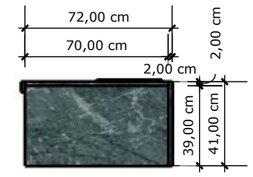

DETALHE: BANCADA B


1:30

Quartzito Verde Guatemala acabamento semi polido em ½ esquadria 122,00 cm x 54,10 cm x 4,00 cm

RECORTE PLANTA: TRECHO VISTA 01 E 02

ESC 1/50


Toda a iluminação da marcenaria será disponibilizada por rede elétrica através do forro

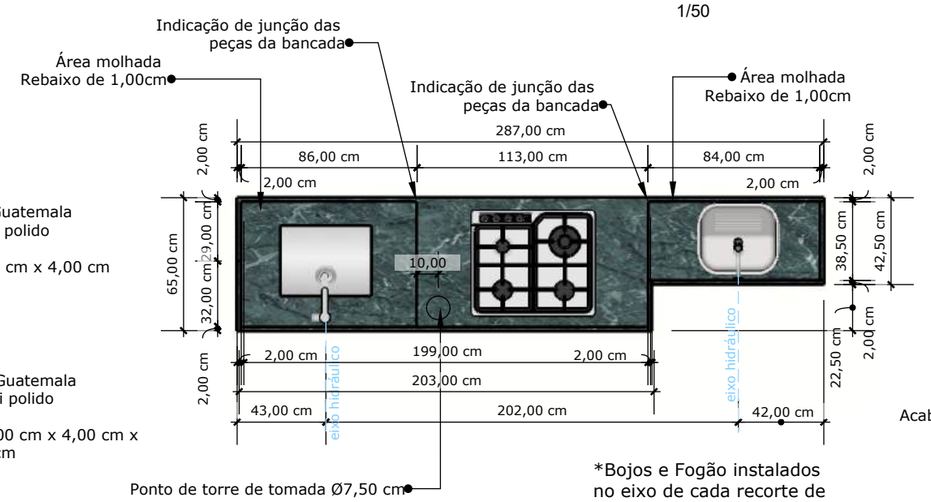

DETALHE: BANCADA A

1:30

*Bojos e Fogão instalados no eixo de cada recorte de bancada

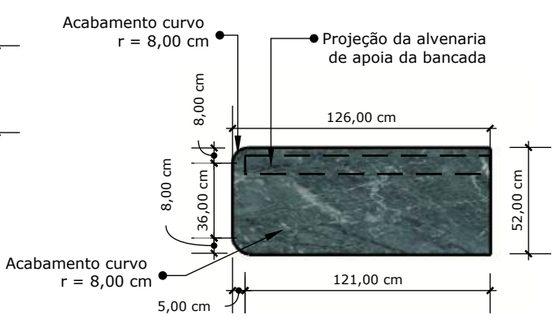


DETALHE: BANCADA C

1:30

OBSERVAÇÕES IMPORTANTES							
-ALGUMAS MEDIDAS ESTÃO COM VALORES APROXIMADOS.	REVISÃO	DATA	ANDAMENTO	**CLIENTE**	**FORMATO**	**DATA**	
-TODAS AS MEDIDAS DEVERÃO SER CONFERIDAS NO LOCAL.				CHARBEL	A3	OUT/2026	
-TODAS AS MEDIDAS ESTÃO EM CENTÍMETROS.	1	05/08	APRESENTAÇÃO ANTEPROJETO - 1/3	**CONTEÚDO**	**ESCALA**	**FOLHA**	
	2	26/08	APRESENTAÇÃO ANTEPROJETO - 2/3	DETALHAMENTO: COZINHA	1/50	15	
-EM CASO DE DÚVIDAS, CONSULTAR AS PROFISSIONAIS.	3	16/10	ENTREGA PROJETO EXECUTIVO				


MARIANA BORGES - ARQUITETURA & INTERIORES
BELO HORIZONTE - NOVA LIMA - BRASIL - (31) 98789-4636 - @marianaborges_arquiteta

"As ideias constantes do projeto, sua concepção e detalhamento constituem patrimônio da profissional como direito autoral, e somente poderão ser divulgados com a sua autorização."

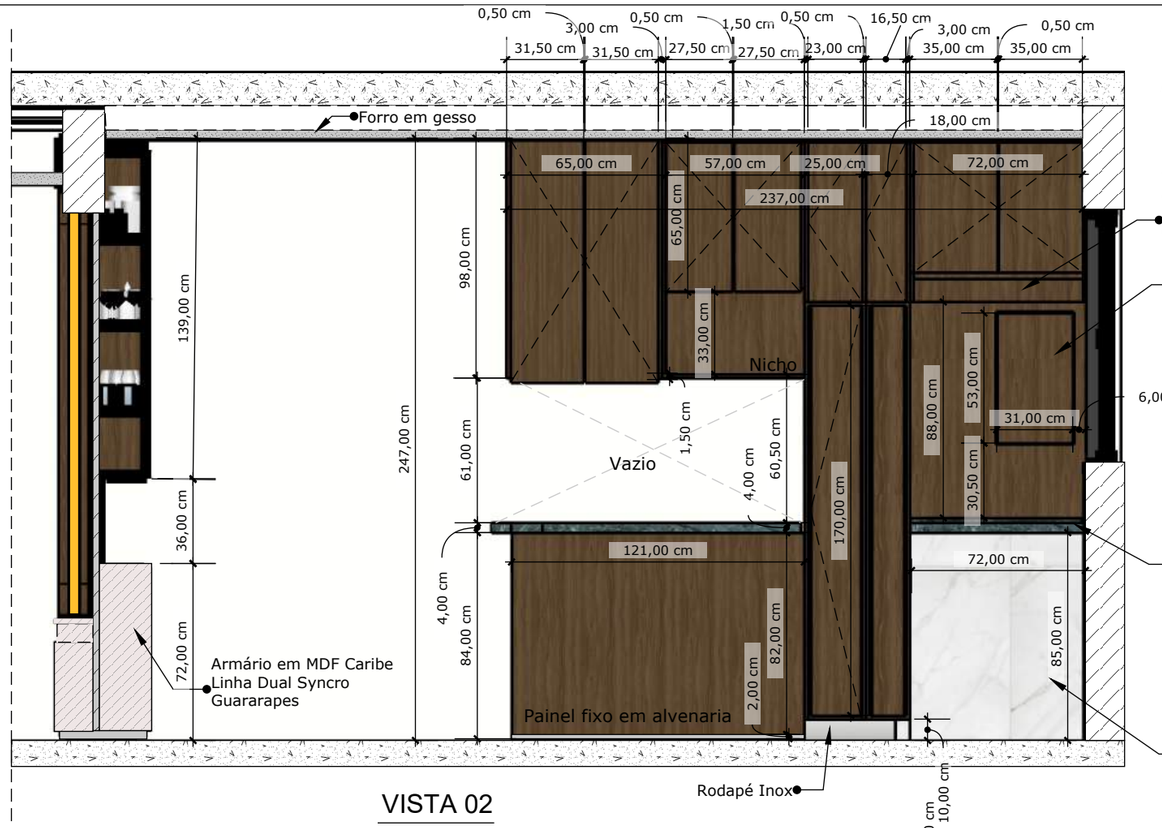

VISTA 02

ESC 1/25

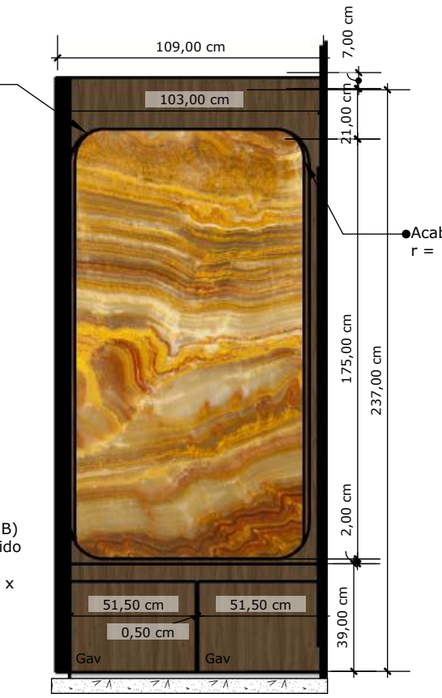

VISTA 04

ESC 1/25




PERSPECTIVA: DIVISÓRIA HALL

1:30




PERSPECTIVA: VISTA 02

1:30

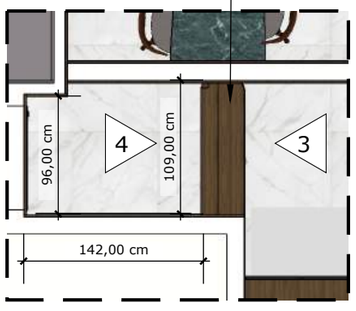


MAPA CHAVE: HALL & JANTAR

ESC 1/75

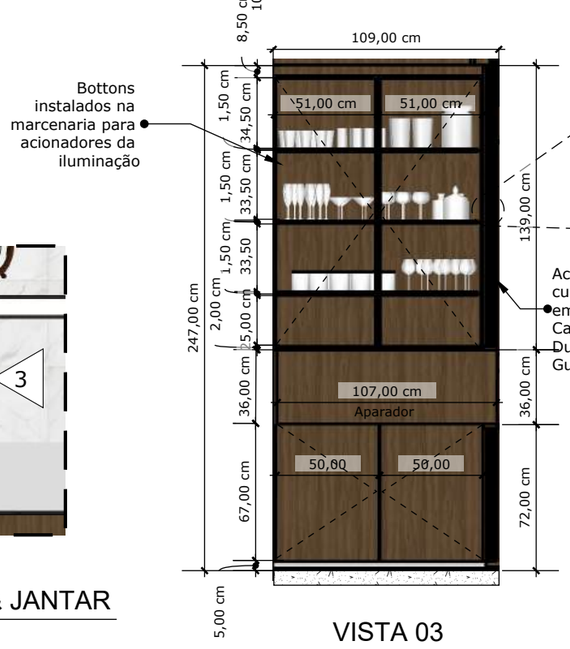


VISTA 03

ESC 1/25

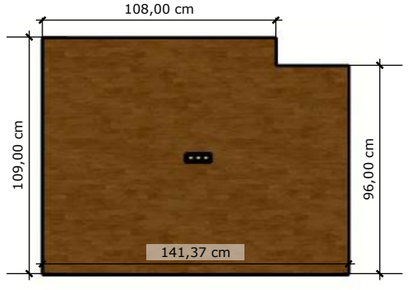

DETALHE: FORRO HALL

1:25

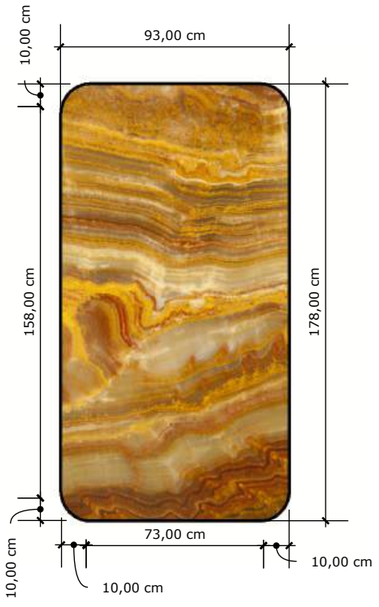

DETALHE: MÁRMORE HALL

1:25

OBSERVAÇÕES IMPORTANTES

-ALGUMAS MEDIDAS ESTÃO COM VALORES APROXIMADOS.

-TODAS AS MEDIDAS DEVERÃO SER CONFERIDAS NO LOCAL.

-TODAS AS MEDIDAS ESTÃO EM CENTÍMETROS.

-EM CASO DE DÚVIDAS, CONSULTAR AS PROFISSIONAIS.

REVISÃO	DATA	ANDAMENTO
1	05/08	APRESENTAÇÃO ANTEPROJETO - 1/3
2	26/08	APRESENTAÇÃO ANTEPROJETO - 2/3
3	16/10	ENTREGA PROJETO EXECUTIVO

CLIENTE
CHARBEL

FORMATO
A3

DATA
OUT/2026


CONTEÚDO
DETALHAMENTO: COZINHA, HALL & JANTAR

ESCALA
1/50

FOLHA
16


MARIANA BORGES - ARQUITETURA & INTERIORES
BELO HORIZONTE - NOVA LIMA - BRASIL - (31) 98789-4636 - @marianaborges_arquiteta

"As ideias constantes do projeto, sua concepção e detalhamento constituem patrimônio da profissional como direito autoral, e somente poderão ser divulgados com a sua autorização."

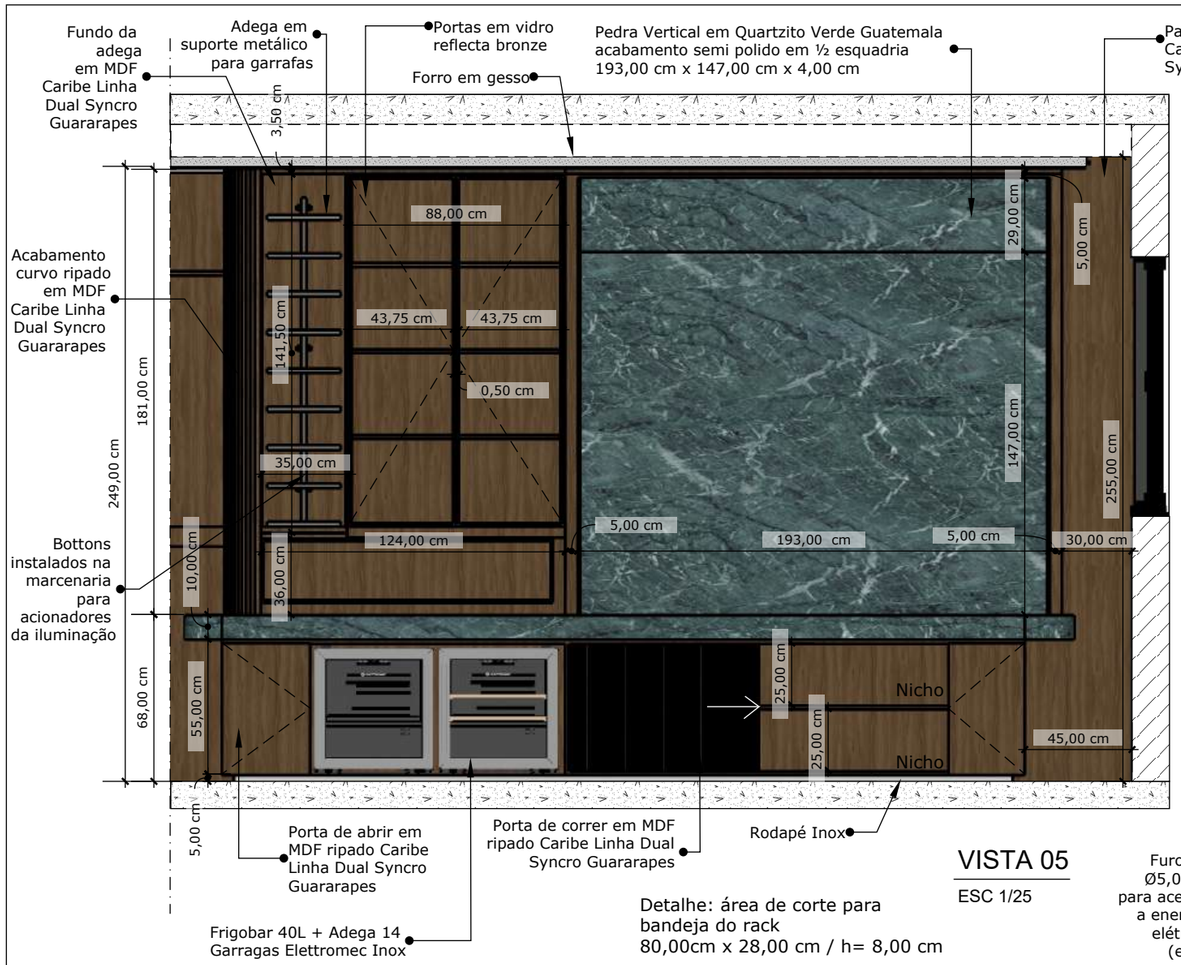


VISTA 05

ESC 1/25

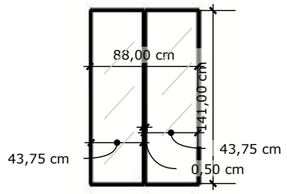


DETALHE: PORTAS DE VIDRO

ESC 1/50

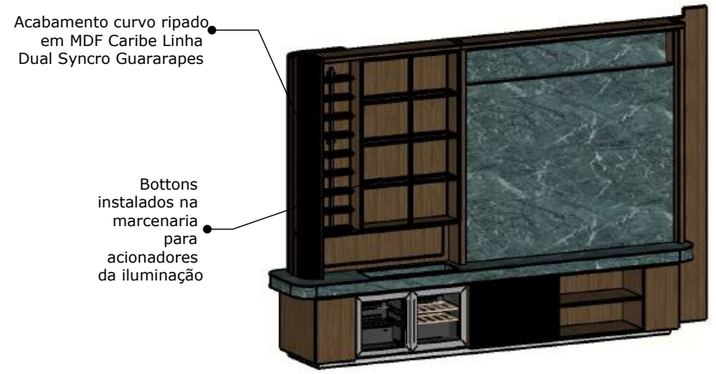


PERSPECTIVA:VISTA 05


ESC 1/30

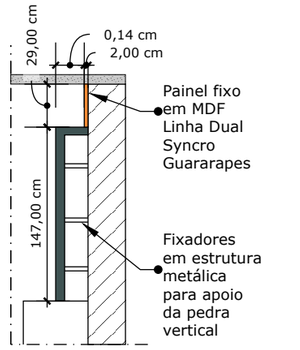



CORTE: PEDRA VERTICAL TV

ESC 1/50

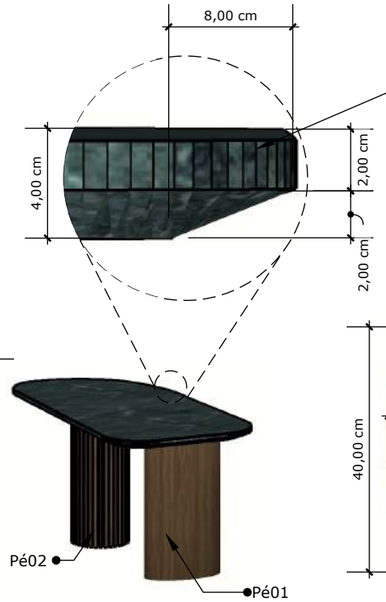

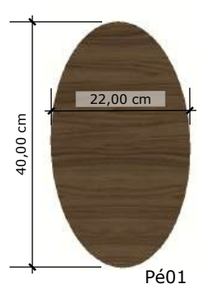

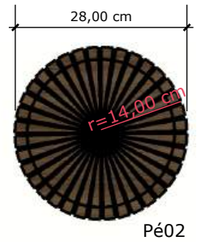


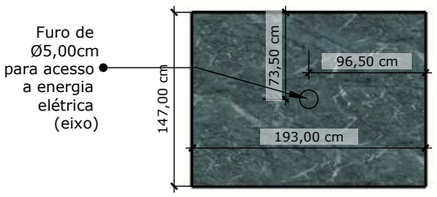


DETALHE: PEDRA VERTICAL TV

ESC 1/50


Detalhe: área de corte para bandeja do rack
80,00cm x 28,00 cm / h= 8,00 cm

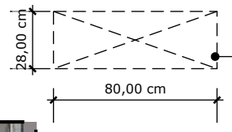

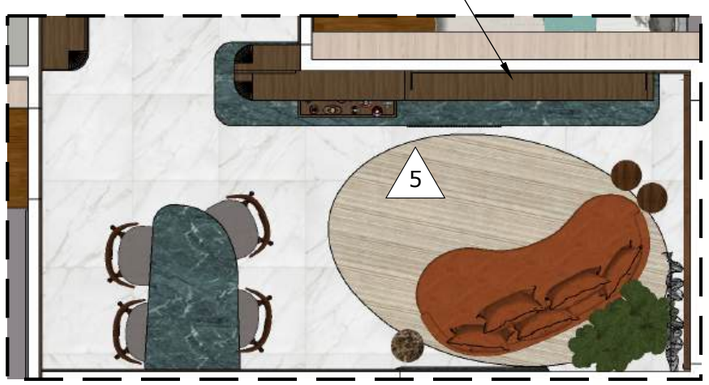

MAPA CHAVE: RACK & PAINEL TV

ESC 1/75

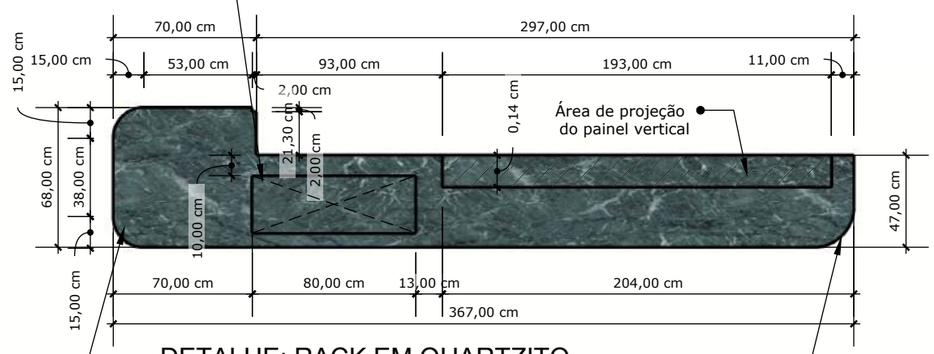



DETALHE: RACK EM QUARTZITO

ESC 1/25

PERSPECTIVA: MESA DE JANTAR

1:30

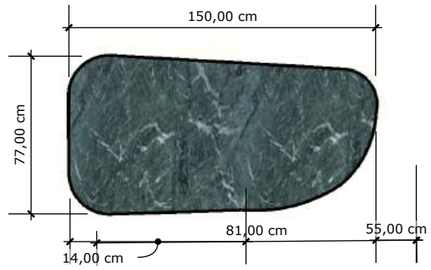

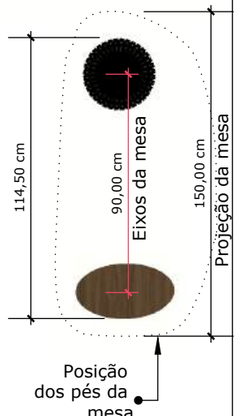

DETALHE: MESA DE JANTAR

1:30

OBSERVAÇÕES IMPORTANTES

-ALGUMAS MEDIDAS ESTÃO COM VALORES APROXIMADOS.

-TODAS AS MEDIDAS DEVERÃO SER CONFERIDAS NO LOCAL.

-TODAS AS MEDIDAS ESTÃO EM CENTÍMETROS.

-EM CASO DE DÚVIDAS, CONSULTAR AS PROFISSIONAIS.

REVISÃO	DATA	ANDAMENTO
1	05/08	APRESENTAÇÃO ANTEPROJETO - 1/3
2	26/08	APRESENTAÇÃO ANTEPROJETO - 2/3
3	16/10	ENTREGA PROJETO EXECUTIVO

CLIENTE
CHARBEL

FORMATO
A3

DATA
OUT/2026


CONTEÚDO
DETALHAMENTO: ESTAR & TV

ESCALA
1/50

FOLHA
17


MARIANA BORGES - ARQUITETURA & INTERIORES
BELO HORIZONTE - NOVA LIMA - BRASIL - (31) 98789-4636 - @marianaborges_arquiteta

"As ideias constantes do projeto, sua concepção e detalhamento constituem patrimônio da profissional como direito autoral, e somente poderão ser divulgados com a sua autorização."

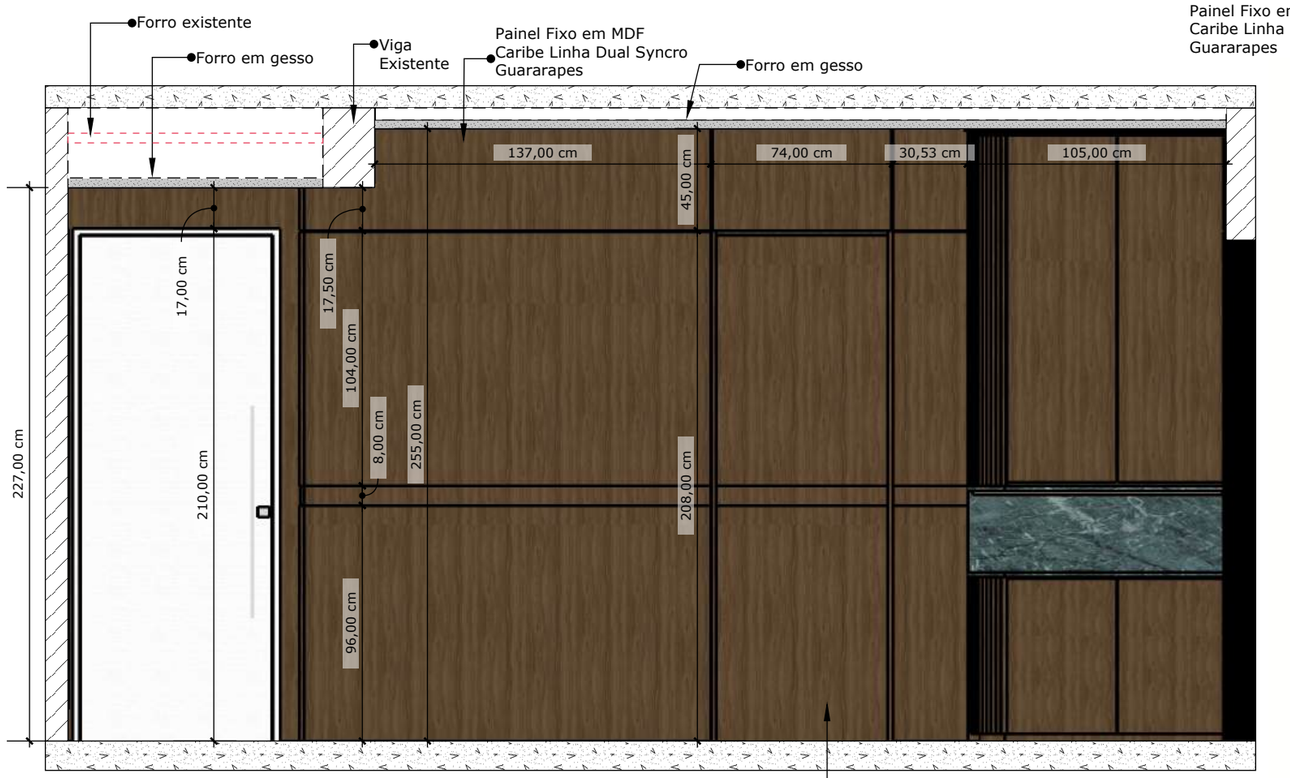


VISTA 05

ESC 1/25

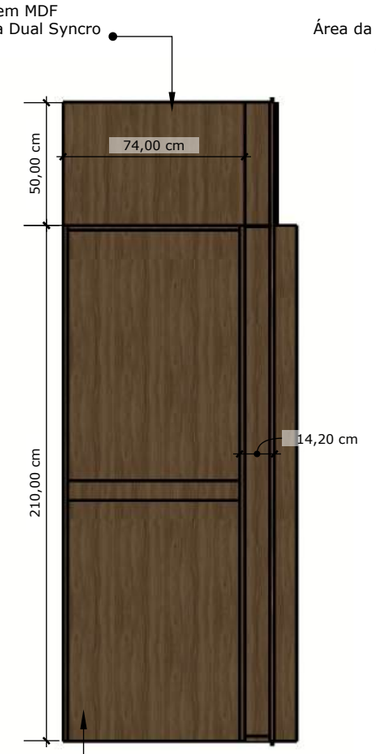

VISTA 08

ESC 1/25

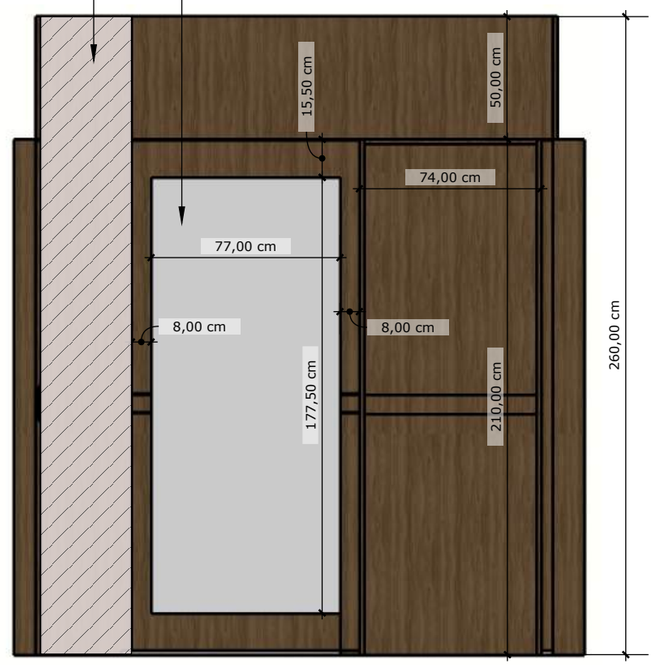

VISTA 07

ESC 1/25

PERSPECTIVA:VISTA 06

ESC 1/50


MAPA CHAVE: ACESSOS & CORREDOR

ESC 1/75




DETALHE:PAINEL ACESSO SUÍTE

ESC 1/30

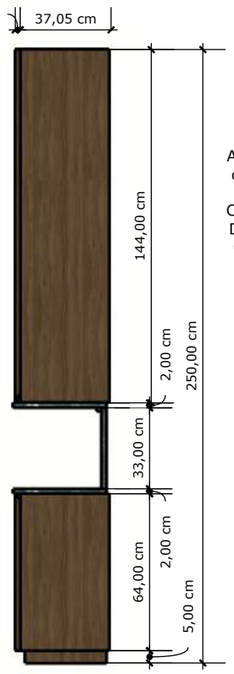

VISTA LATERAL: ARMÁRIO F

ESC 1/25

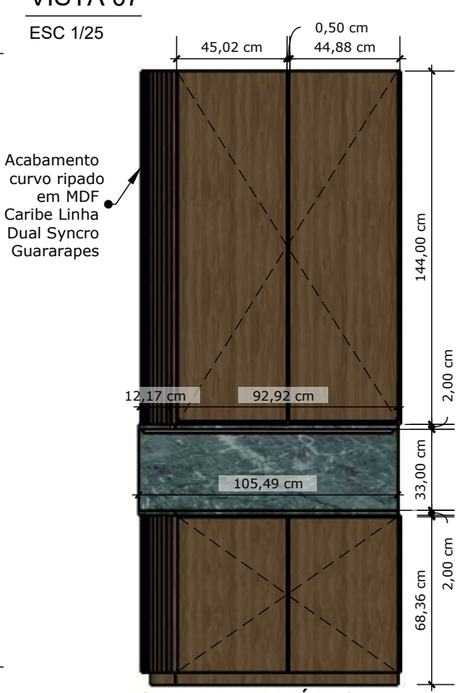

VISTA 06: ARMÁRIO F

ESC 1/25

OBSERVAÇÕES IMPORTANTES

-ALGUMAS MEDIDAS ESTÃO COM VALORES APROXIMADOS.

-TODAS AS MEDIDAS DEVERÃO SER CONFERIDAS NO LOCAL.

-TODAS AS MEDIDAS ESTÃO EM CENTÍMETROS.

-EM CASO DE DÚVIDAS, CONSULTAR AS PROFISSIONAIS.

REVISÃO	DATA	ANDAMENTO
1	05/08	APRESENTAÇÃO ANTEPROJETO - 1/3
2	26/08	APRESENTAÇÃO ANTEPROJETO - 2/3
3	16/10	ENTREGA PROJETO EXECUTIVO

CLIENTE

CHARBEL


CONTEÚDO

DETALHAMENTO: ACESSOS E CORREDOR

FORMATO	DATA
A3	OUT/2026
ESCALA	**FOLHA**
1/50	18

MARIANA BORGES - ARQUITETURA & INTERIORES
BELO HORIZONTE - NOVA LIMA - BRASIL - (31) 98789-4636 - @marianaborges_arquiteta

"As ideias constantes do projeto, sua concepção e detalhamento constituem patrimônio da profissional como direito autoral, e somente poderão ser divulgados com a sua autorização."

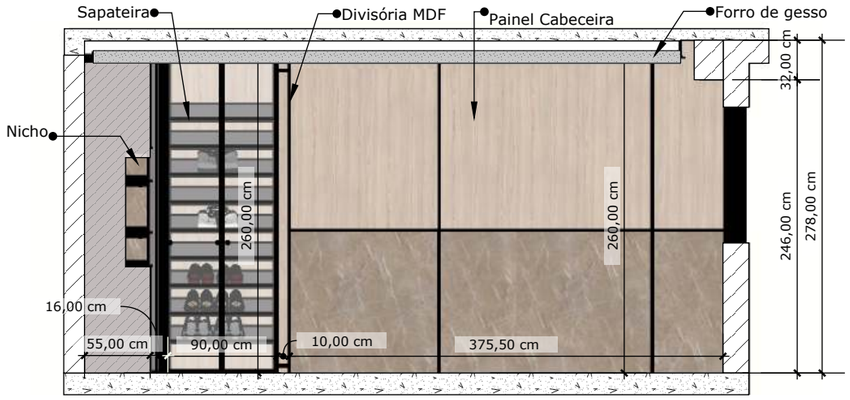


VISTA 10

ESC 1/50




MAPA CHAVE: SUÍTE

ESC 1/75

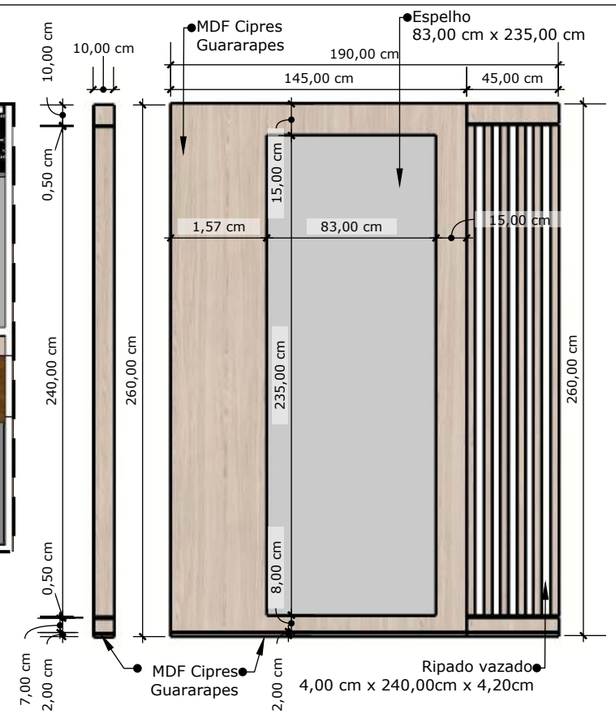


DETALHE: DIVISÓRIA MDF / VISTA 13

ESC 1/25

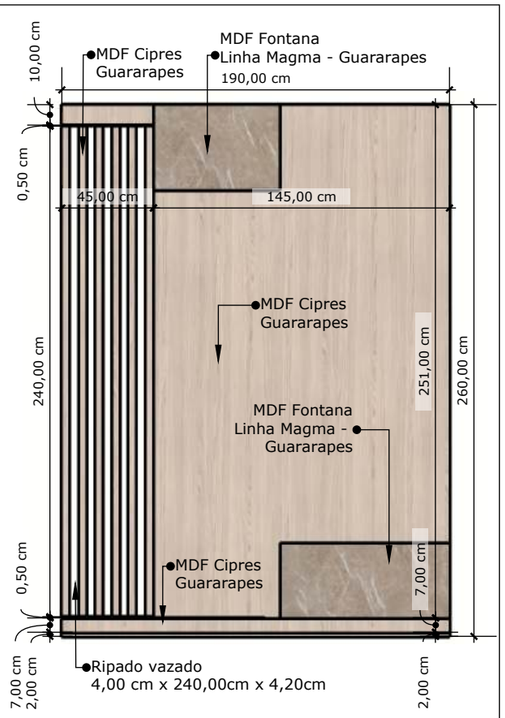


DETALHE: DIVISÓRIA MDF / VISTA 12

ESC 1/25

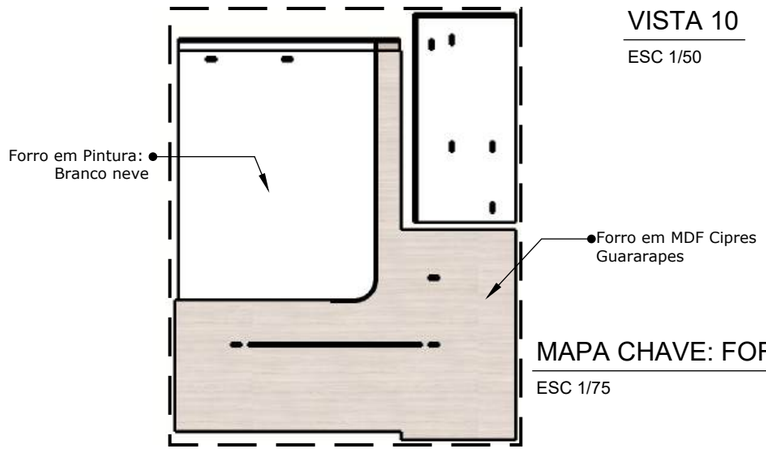


MAPA CHAVE: FORRO SUÍTE

ESC 1/75

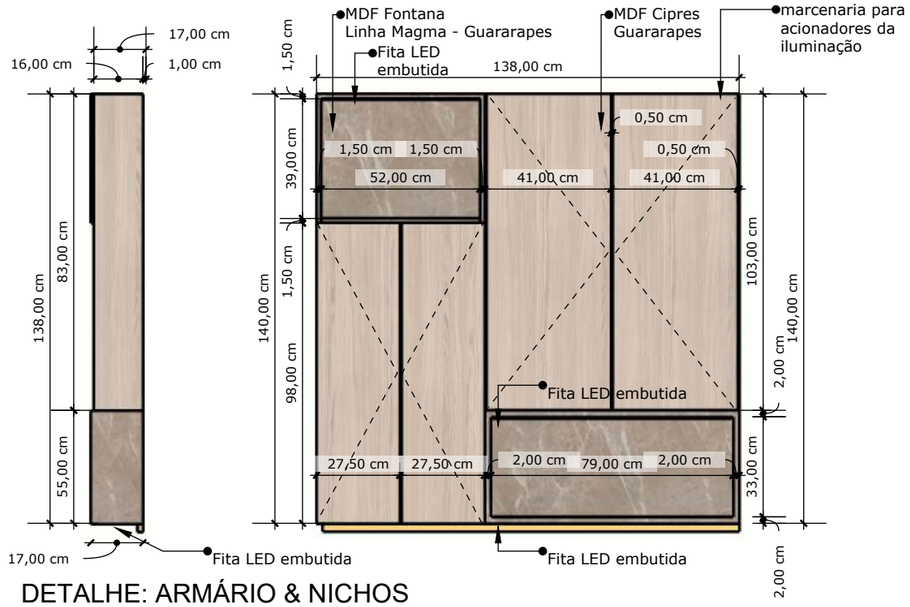


DETALHE: ARMÁRIO & NICHOS

ESC 1/25

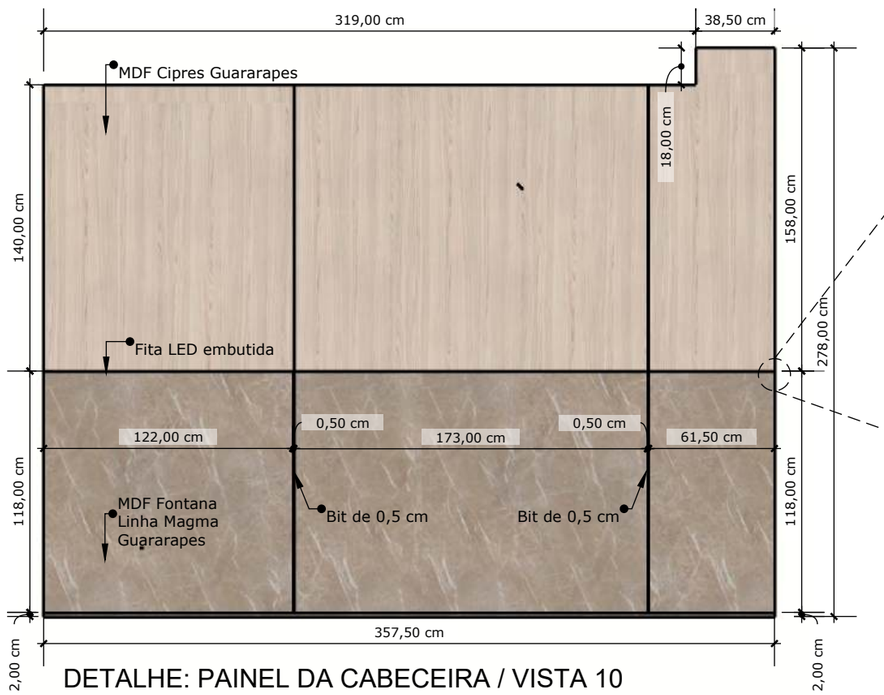

DETALHE: PAINEL DA CABECEIRA / VISTA 10

ESC 1/25

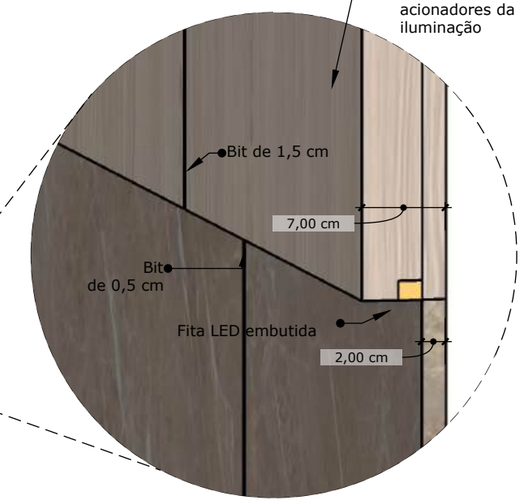

DETALHE: PAINEL DA CABECEIRA

ESC 1/5

OBSERVAÇÕES IMPORTANTES

-ALGUMAS MEDIDAS ESTÃO COM VALORES APROXIMADOS.

-TODAS AS MEDIDAS DEVERÃO SER CONFERIDAS NO LOCAL.

-TODAS AS MEDIDAS ESTÃO EM CENTÍMETROS.

-EM CASO DE DÚVIDAS, CONSULTAR AS PROFISSIONAIS.

REVISÃO	DATA	ANDAMENTO
1	05/08	APRESENTAÇÃO ANTEPROJETO - 1/3
2	26/08	APRESENTAÇÃO ANTEPROJETO - 2/3
3	16/10	ENTREGA PROJETO EXECUTIVO

CLIENTE
CHARBEL

FORMATO
A3

DATA
OUT/2026

CONTEÚDO
DETALHAMENTO: SUÍTE

ESCALA
1/50

FOLHA
19

MARIANA BORGES - ARQUITETURA & INTERIORES
BELO HORIZONTE - NOVA LIMA - BRASIL - (31) 98789-4636 - @marianaborges_arquiteta

"As ideias constantes do projeto, sua concepção e detalhamento constituem patrimônio da profissional como direito autoral, e somente poderão ser divulgados com a sua autorização."



DETALHE: ÁREA CENTRAL DO PAINEL

ESC 1/25




DETALHE: PRATELEIRA DO PAINEL

ESC 1/25

DETALHE: SAPATEIRA


ESC 1/25

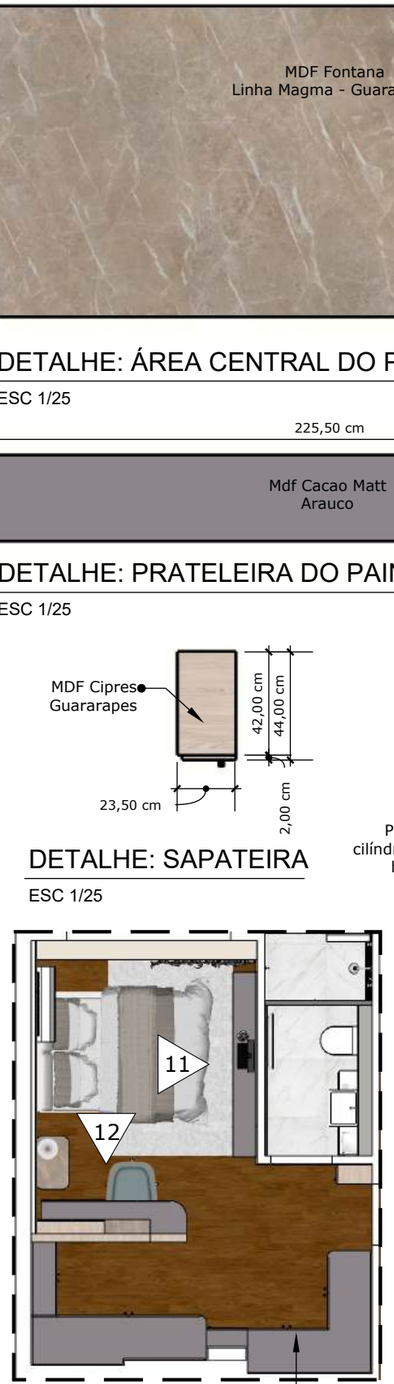

MAPA CHAVE: SUÍTE


ESC 1/75

Toda a iluminação da marcenaria será disponibilizada por rede elétrica através do forro

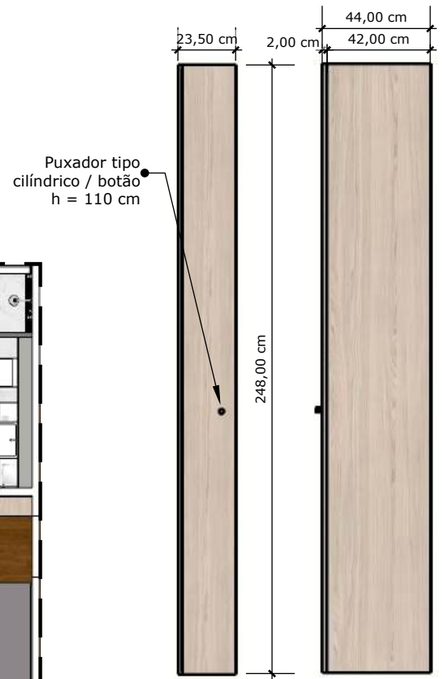


DETALHE: SAPATEIRA

ESC 1/25

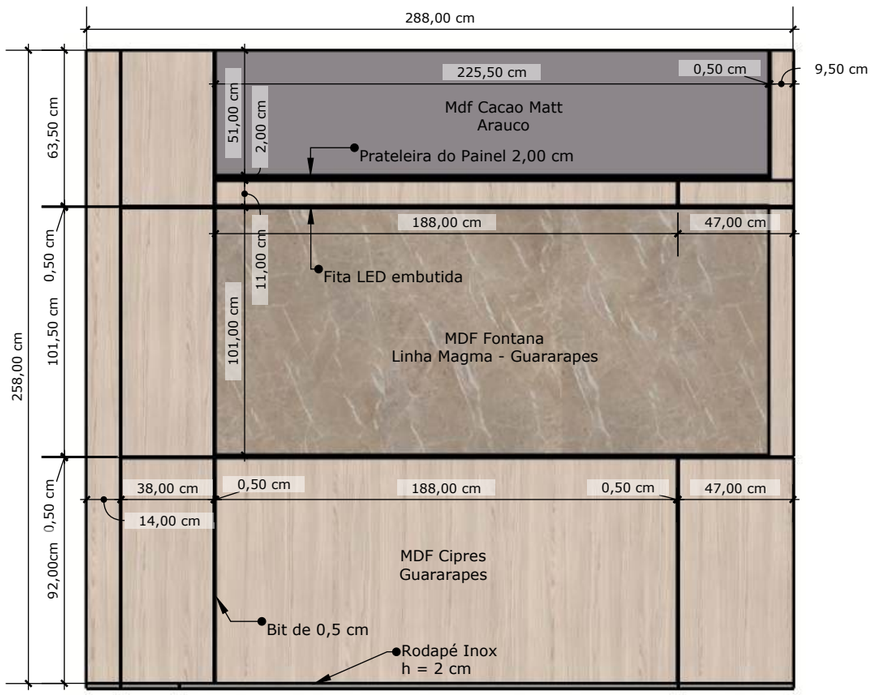


AMPLIAÇÃO: PAINEL / VISTA 11

ESC 1/25

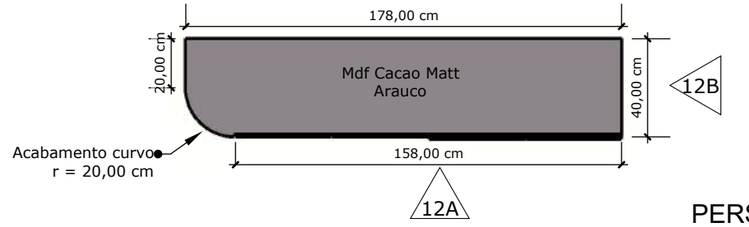


DETALHE: PLANTA BAIXA DA BANCADA

ESC 1/25

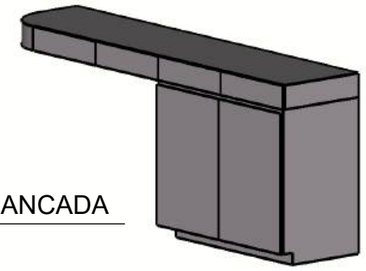


PERSPECTIVA: BANCADA

ESC 1/25

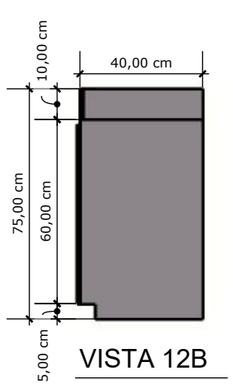


VISTA 12B

ESC 1/25

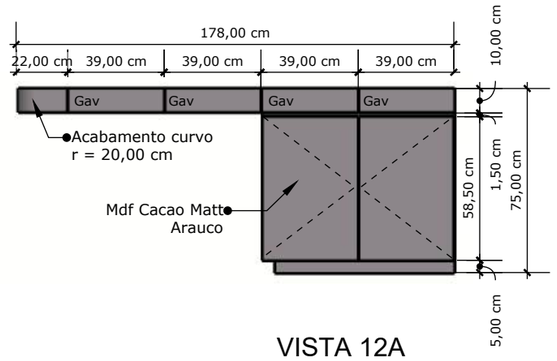


VISTA 12A

ESC 1/25

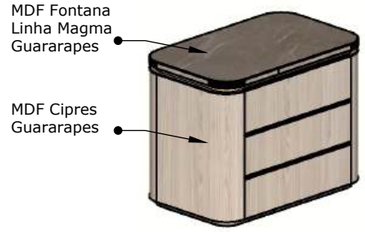


DETALHE: MESA DE CABECEIRA

ESC 1/25

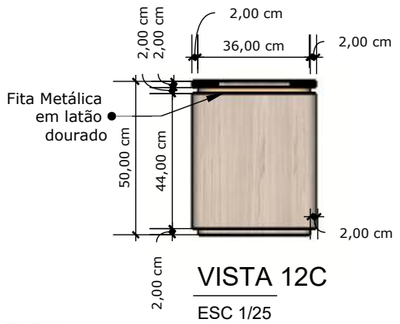


VISTA 12C

ESC 1/25

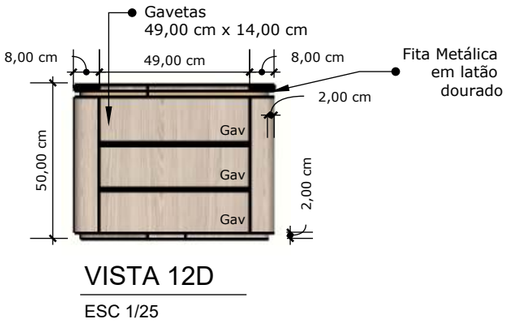

VISTA 12D

ESC 1/25

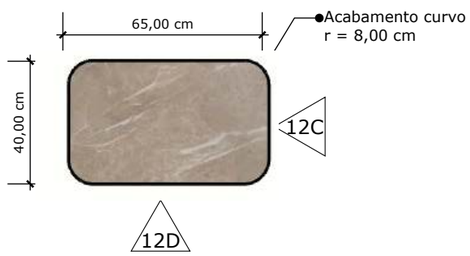

PLANTA: MESA DE CABECEIRA

ESC 1/25

OBSERVAÇÕES IMPORTANTES

-ALGUMAS MEDIDAS ESTÃO COM VALORES APROXIMADOS.

-TODAS AS MEDIDAS DEVERÃO SER CONFERIDAS NO LOCAL.

-TODAS AS MEDIDAS ESTÃO EM CENTÍMETROS.

-EM CASO DÚVIDAS, CONSULTAR AS PROFISSIONAIS.

REVISÃO	DATA	ANDAMENTO
1	05/08	APRESENTAÇÃO ANTEPROJETO - 1/3
2	26/08	APRESENTAÇÃO ANTEPROJETO - 2/3
3	16/10	ENTREGA PROJETO EXECUTIVO

CLIENTE
CHARBEL


CONTEÚDO
DETALHAMENTO: SUÍTE

FORMATO	DATA
A3	OUT/2026

ESCALA	FOLHA
1/50	20


MARIANA BORGES - ARQUITETURA & INTERIORES
BELO HORIZONTE - NOVA LIMA - BRASIL - (31) 98789-4636 - @marianaborges_arquiteta

"As ideias constantes do projeto, sua concepção e detalhamento constituem patrimônio da profissional como direito autoral, e somente poderão ser divulgados com a sua autorização."

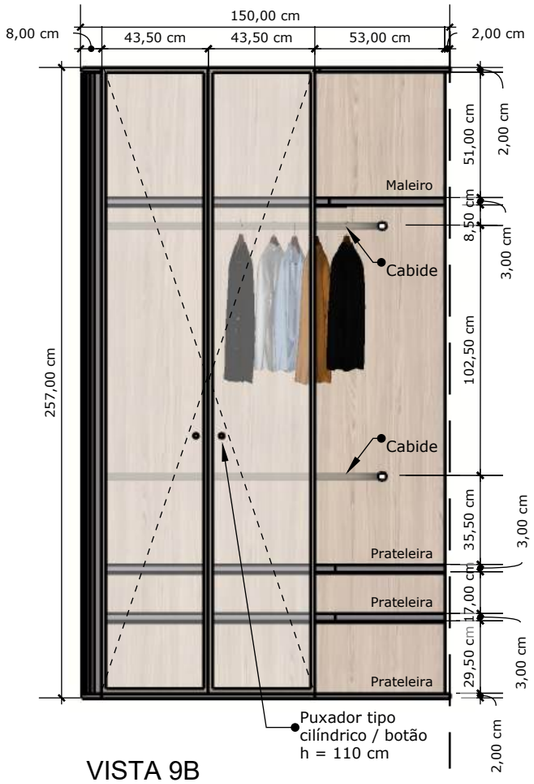

VISTA 9B


ESC 1/25

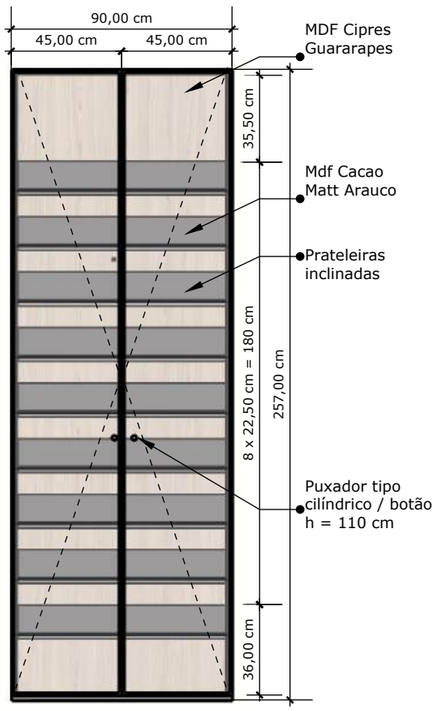

***Medidas relativas ao fundo da prateleira**

VISTA 9C

ESC 1/25

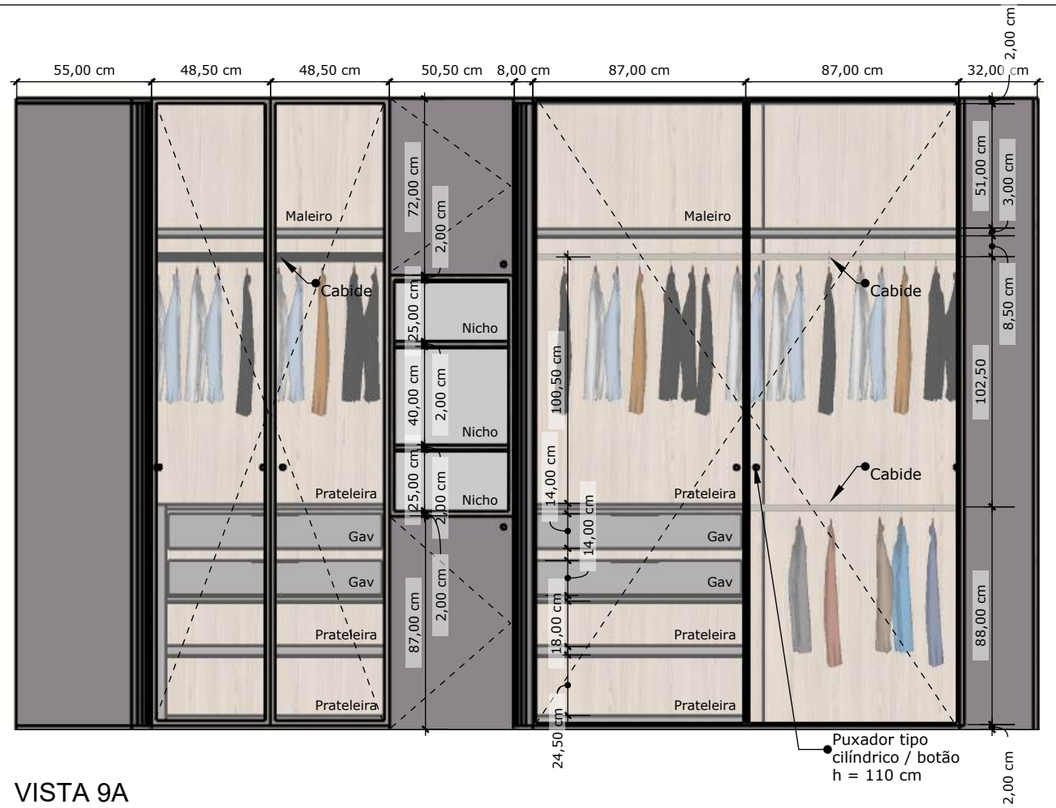


VISTA 9A

ESC 1/25



MAPA CHAVE: SUÍTE

ESC 1/75

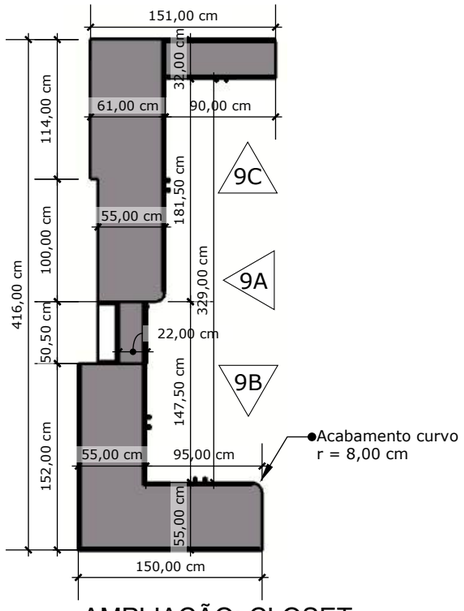

AMPLIAÇÃO: CLOSET

ESC 1/50



PERSPECTIVA: CLOSET

ESC 1/50



PERSPECTIVA: CLOSET

ESC 1/50

OBSERVAÇÕES IMPORTANTES

-ALGUMAS MEDIDAS ESTÃO COM VALORES APROXIMADOS.

-TODAS AS MEDIDAS DEVERÃO SER CONFERIDAS NO LOCAL.

-TODAS AS MEDIDAS ESTÃO EM CENTÍMETROS.

-EM CASO DE DÚVIDAS, CONSULTAR AS PROFISSIONAIS.

REVISÃO	DATA	ANDAMENTO
1	05/08	APRESENTAÇÃO ANTEPROJETO - 1/3
2	26/08	APRESENTAÇÃO ANTEPROJETO - 2/3
3	16/10	ENTREGA PROJETO EXECUTIVO

CLIENTE
CHARBEL

FORMATO
A3

DATA
OUT/2026


CONTEÚDO
DETALHAMENTO: SUÍTE

ESCALA
1/50

FOLHA
21


MARIANA BORGES - ARQUITETURA & INTERIORES
BELO HORIZONTE - NOVA LIMA - BRASIL - (31) 98789-4636 - @marianaborges_arquiteta

"As ideias constantes do projeto, sua concepção e detalhamento constituem patrimônio da profissional como direito autoral, e somente poderão ser divulgados com a sua autorização."

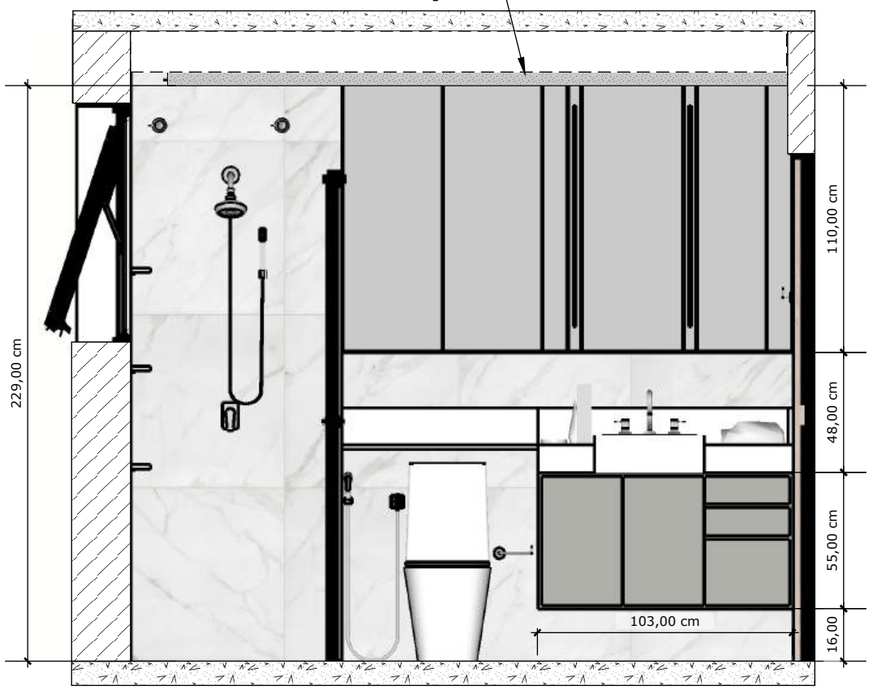


VISTA 15

ESC 1/25

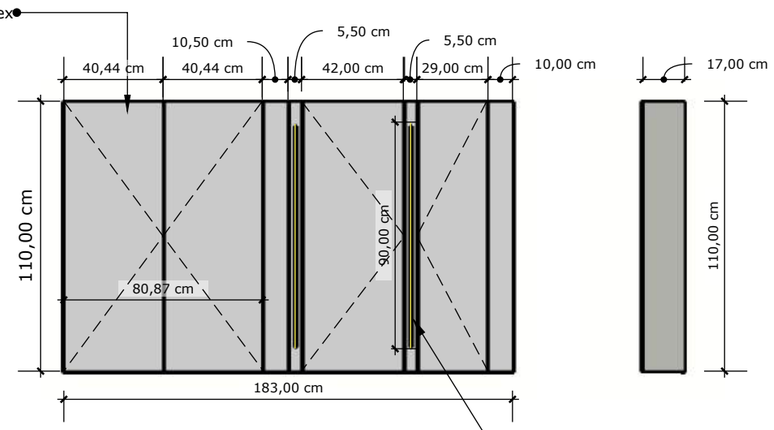


DETALHE: ARMÁRIO SUPERIOR

ESC 1/25

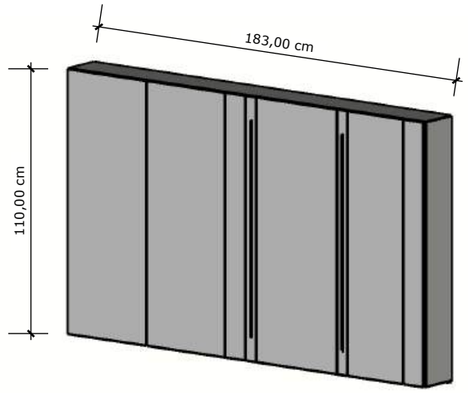


PERSPECTIVA: ARMÁRIO SUPERIOR

ESC 1/25

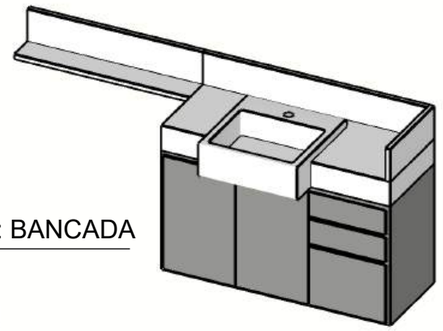

PERSPECTIVA: BANCADA

ESC 1/20

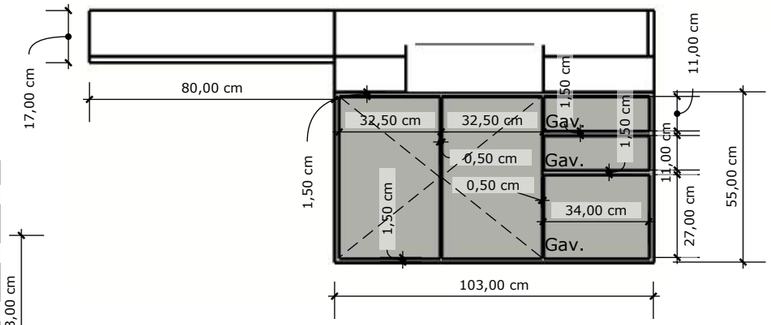


VISTA FRONTAL: ARMÁRIO INFERIOR

ESC 1/20




MAPA CHAVE: SUÍTE

ESC 1/75

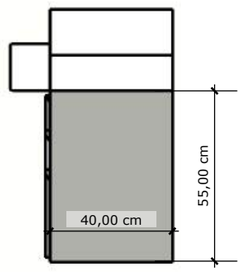


DETALHE: ARMÁRIO INFERIOR

ESC 1/20

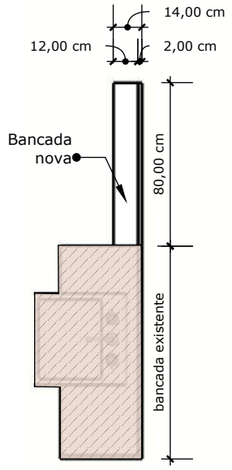

DETALHE: BANCADA

ESC 1/25

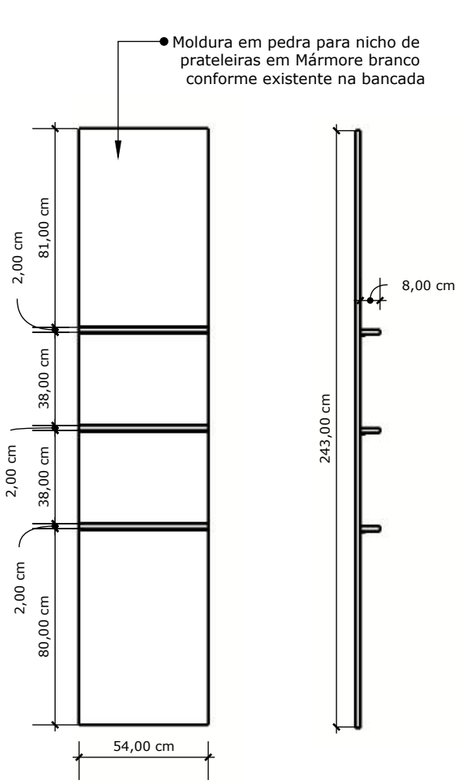

DETALHE: NICHO BOX

ESC 1/25

OBSERVAÇÕES IMPORTANTES

-ALGUMAS MEDIDAS ESTÃO COM VALORES APROXIMADOS.

-TODAS AS MEDIDAS DEVERÃO SER CONFERIDAS NO LOCAL.

-TODAS AS MEDIDAS ESTÃO EM CENTÍMETROS.

-EM CASO DE DÚVIDAS, CONSULTAR AS PROFISSIONAIS.

REVISÃO	DATA	ANDAMENTO
1	05/08	APRESENTAÇÃO ANTEPROJETO - 1/3
2	26/08	APRESENTAÇÃO ANTEPROJETO - 2/3
3	16/10	ENTREGA PROJETO EXECUTIVO

CLIENTE
CHARBEL

FORMATO
A3

DATA
OUT/2026


CONTEÚDO
DETALHAMENTO: BANHO SUÍTE

ESCALA
1/50

FOLHA
22


MARIANA BORGES - ARQUITETURA & INTERIORES
BELO HORIZONTE - NOVA LIMA - BRASIL - (31) 98789-4636 - @marianaborges_arquiteta

"As ideias constantes do projeto, sua concepção e detalhamento constituem patrimônio da profissional como direito autoral, e somente poderão ser divulgados com a sua autorização."

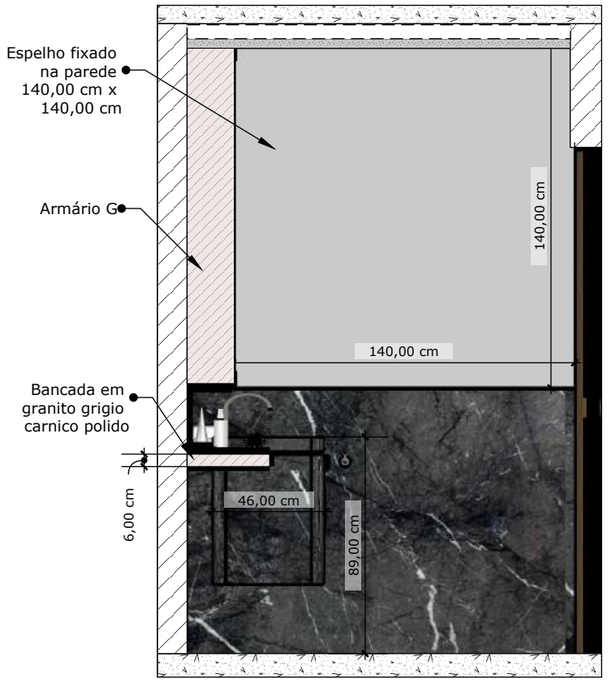


VISTA 16


ESC 1/25

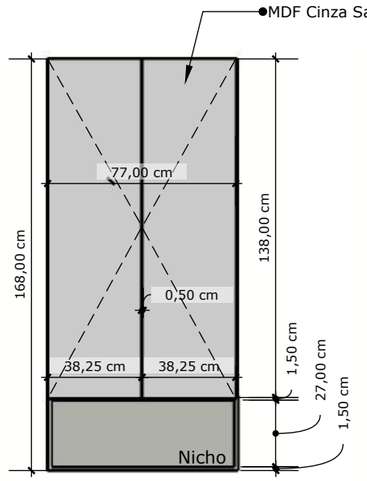

DETALHE: ARMÁRIO "H"


ESC 1/25

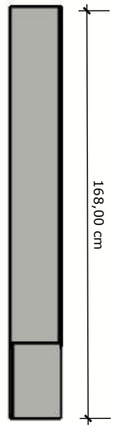


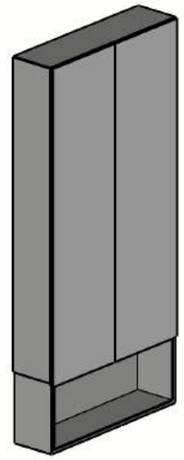

PERSPECTIVA: ARMÁRIO "H"

ESC 1/25

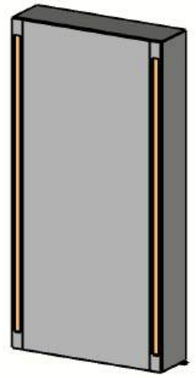

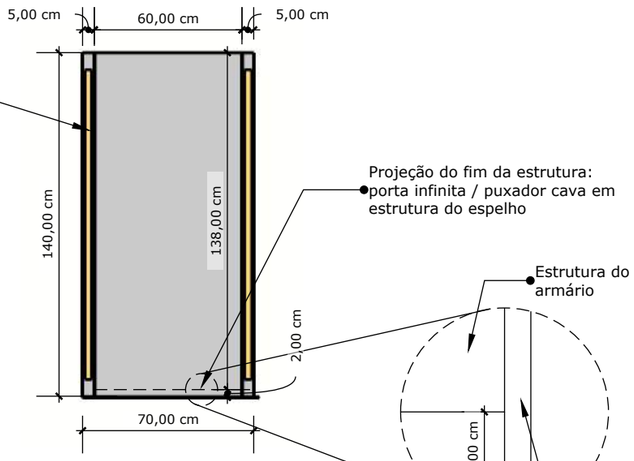

DETALHE: ARMÁRIO "G"

ESC 1/25


DETALHE: PUXADOR

ESC 1/25



PERSPECTIVA: CUBA ESCULPIDA

ESC 1/25

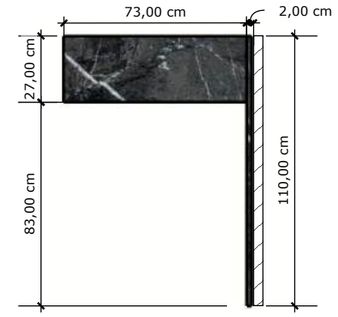


DETALHE: RODAPAREDE

ESC 1/25

PERSPECTIVA: ARMÁRIO "G"


ESC 1/25

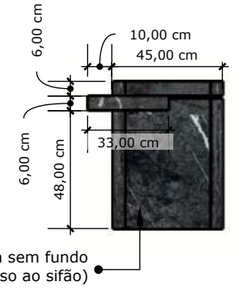




DETALHE: CUBA ESCULPIDA

ESC 1/25

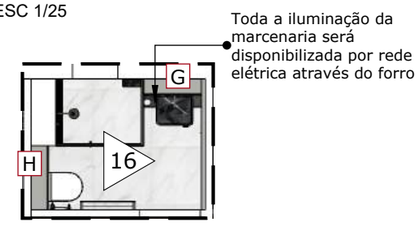


MAPA CHAVE: BANHEIRO SOCIAL

ESC 1/75

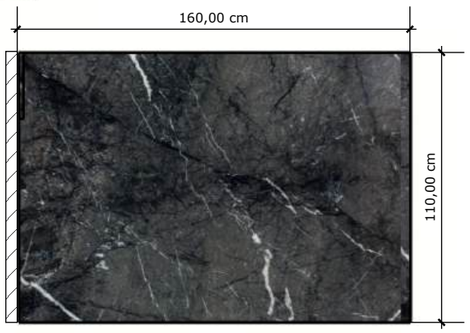


DETALHE: RODAPAREDE / VISTA 16

ESC 1/25

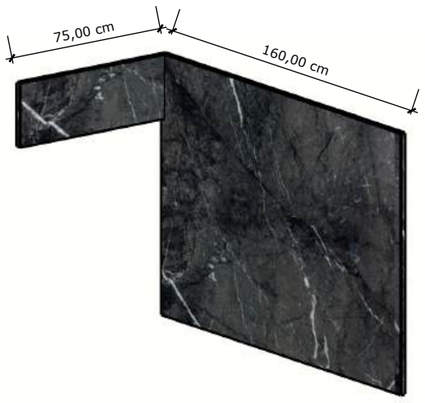

PERSPECTIVA: RODAPAREDE

ESC 1/25

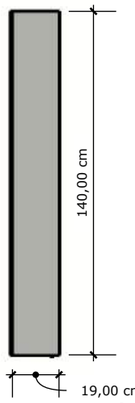

DETALHE: ARMÁRIO "G"

ESC 1/25

DETALHE: PRATELEIRAS EM MÁRMORE

ESC 1/25

OBSERVAÇÕES IMPORTANTES

-ALGUMAS MEDIDAS ESTÃO COM VALORES APROXIMADOS.

-TODAS AS MEDIDAS DEVERÃO SER CONFERIDAS NO LOCAL.

-TODAS AS MEDIDAS ESTÃO EM CENTÍMETROS.

-EM CASO DE DÚVIDAS, CONSULTAR AS PROFISSIONAIS.

REVISÃO	DATA	ANDAMENTO
1	05/08	APRESENTAÇÃO ANTEPROJETO - 1/3
2	26/08	APRESENTAÇÃO ANTEPROJETO - 2/3
3	16/10	ENTREGA PROJETO EXECUTIVO

CLIENTE
CHARBEL

FORMATO
A3

DATA
OUT/2026


CONTEÚDO
DETALHAMENTO: BANHEIRO SOCIAL

ESCALA
1/50

FOLHA
23


MARIANA BORGES - ARQUITETURA & INTERIORES
BELO HORIZONTE - NOVA LIMA - BRASIL - (31) 98789-4636 - @marianaborges_arquiteta

"As ideias constantes do projeto, sua concepção e detalhamento constituem patrimônio da profissional como direito autoral, e somente poderão ser divulgados com a sua autorização."

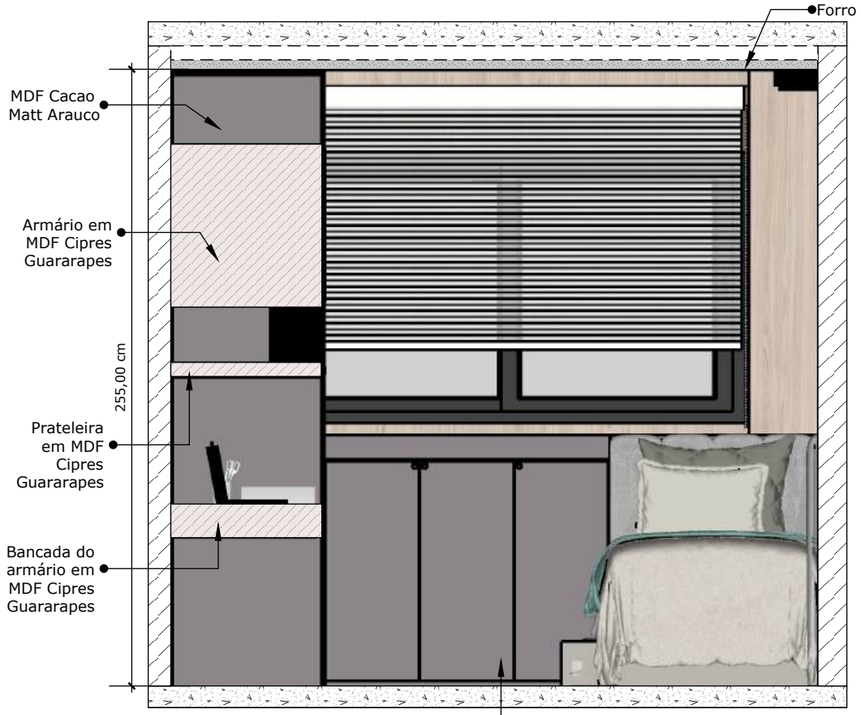

VISTA 17

ESC 1/25

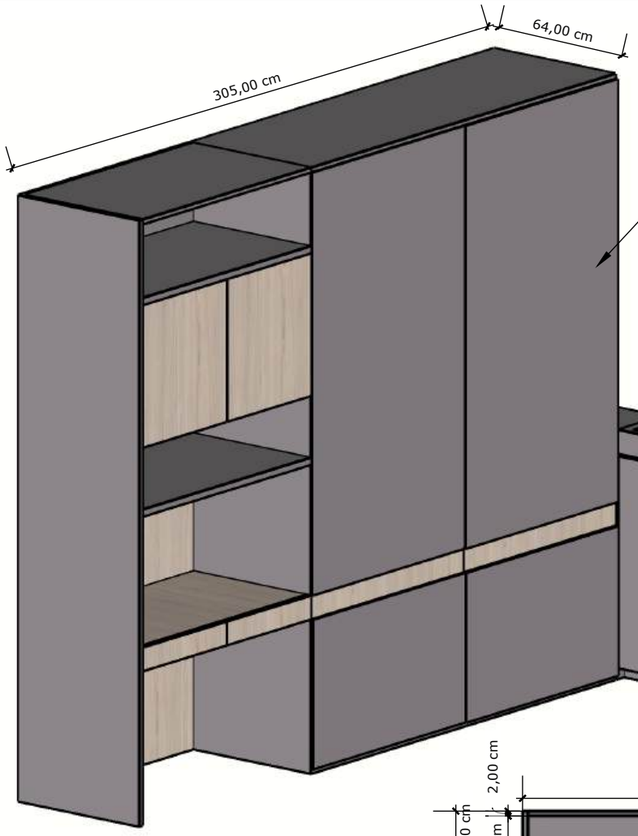


PERSPECTIVA: ARMÁRIO QUARTO

ESC 1/25

DETALHE: ARMÁRIO QUARTO / VISTA 17

ESC 1/25

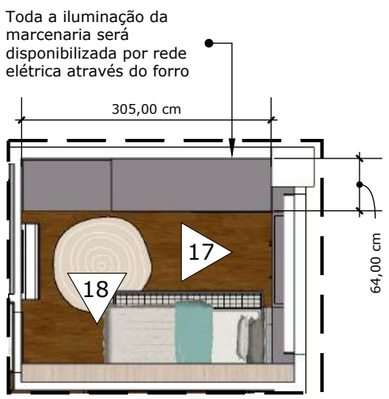

MAPA CHAVE: SUÍTE

ESC 1/75



DETALHE: ARMÁRIO QUARTO

ESC 1/25

OBSERVAÇÕES IMPORTANTES

-ALGUMAS MEDIDAS ESTÃO COM VALORES APROXIMADOS.

-TODAS AS MEDIDAS DEVERÃO SER CONFERIDAS NO LOCAL.

-TODAS AS MEDIDAS ESTÃO EM CENTÍMETROS.

-EM CASO DE DÚVIDAS, CONSULTAR AS PROFISSIONAIS.

REVISÃO	DATA	ANDAMENTO
1	05/08	APRESENTAÇÃO ANTEPROJETO - 1/3
2	26/08	APRESENTAÇÃO ANTEPROJETO - 2/3
3	16/10	ENTREGA PROJETO EXECUTIVO

CLIENTE

CHARBEL

CONTEÚDO


DETALHAMENTO: QUARTO

FORMATO	DATA
A3	OUT/2026

ESCALA	FOLHA
1/50	24


MARIANA BORGES - ARQUITETURA & INTERIORES
BELO HORIZONTE - NOVA LIMA - BRASIL - (31) 98789-4636 - @marianaborges_arquiteta

"As ideias constantes do projeto, sua concepção e detalhamento constituem patrimônio da profissional como direito autoral, e somente poderão ser divulgados com a sua autorização."

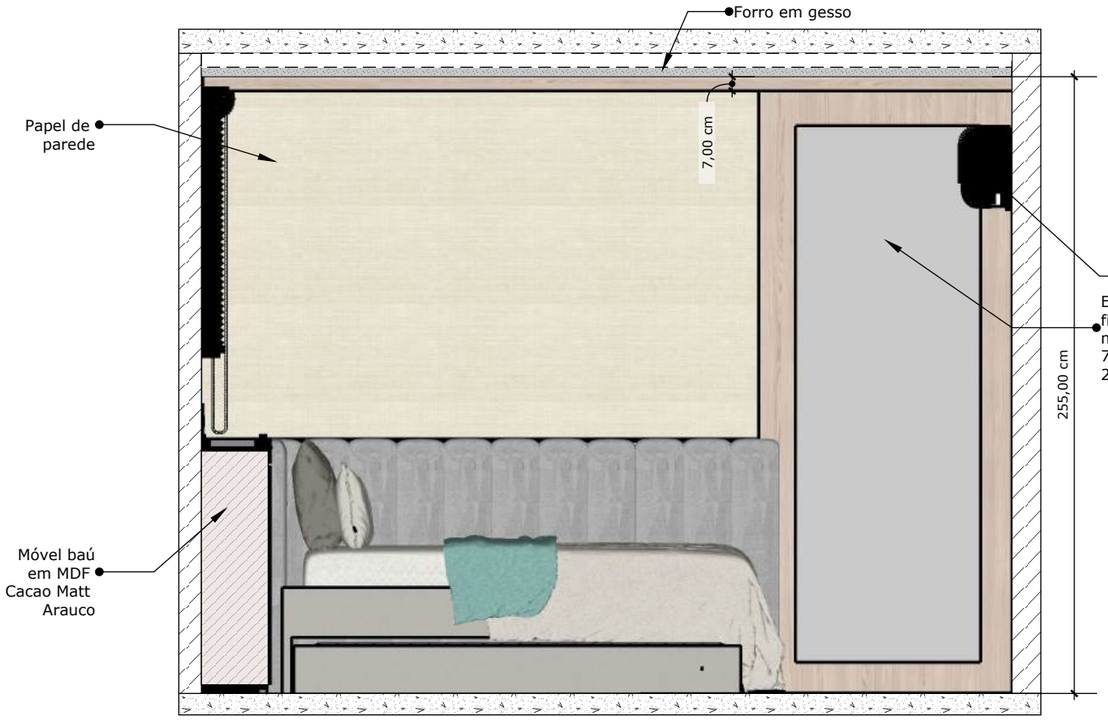

VISTA 17

ESC 1/25

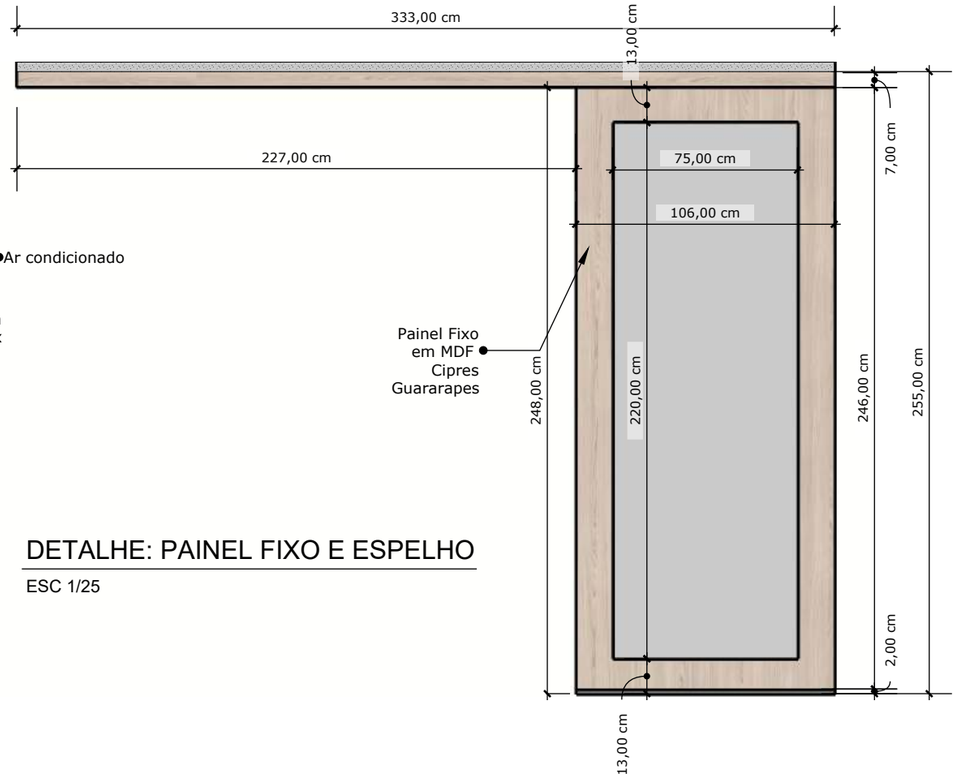

DETALHE: PAINEL FIXO E ESPELHO

ESC 1/25

DETALHE: REVESTIMENTO POR BAIXO DA VIGA

ESC 1/25

MAPA CHAVE: QUARTO

ESC 1/75

OBSERVAÇÕES IMPORTANTES	
	-ALGUMAS MEDIDAS ESTÃO COM VALORES APROXIMADOS.
	-TODAS AS MEDIDAS DEVERÃO SER CONFERIDAS NO LOCAL.
	-TODAS AS MEDIDAS ESTÃO EM CENTÍMETROS.
	-EM CASO DE DÚVIDAS, CONSULTAR AS PROFISSIONAIS.

REVISÃO	DATA	ANDAMENTO
1	05/08	APRESENTAÇÃO ANTEPROJETO - 1/3
2	26/08	APRESENTAÇÃO ANTEPROJETO - 2/3
3	16/10	ENTREGA PROJETO EXECUTIVO

CLIENTE
CHARBEL

CONTEÚDO
DETALHAMENTO: QUARTO

FORMATO	DATA
A3	OUT/2026
ESCALA	**FOLHA**
1/50	25

MARIANA BORGES - ARQUITETURA & INTERIORES
BELO HORIZONTE - NOVA LIMA - BRASIL - (31) 98789-4636 - @marianaborges_arquiteta

"As ideias constantes do projeto, sua concepção e detalhamento constituem patrimônio da profissional como direito autoral, e somente poderão ser divulgados com a sua autorização."