
LEGENDA ACABAMENTOS	
PISO	
1	Deck em madeira Cumaru, réguas de 10cm
2	Piso intertravado, modelo a definir
3	Piso em pedra a definir
4	Piso Cimenticio a definir
5	Azulejo tipo Hijau, 20x20cm
6	Porcelanato tipo Travertino, Acetinado, 120x120cm
7	Porcelanato Portobello Anima di Marmo Acetinado 120x120cm
8	Piso Vinilico a definir
9	Piso Seixos a definir
10	Porcelanato tipo cimento queimado, Acetinado, 90x90cm
11	Mármore Bege Bahia Escovado
RODAPÉ	
1	Rodapé h=15cm em Porcelanato tipo Travertino, Acetinado
2	Rodapé h=15cm em Poliestireno, com friso, na cor Fendi, Santa Luzia
2	Rodapé h=15cm em Porcelanato tipo cimento queimado, acetinado
SOLEIRA /FILETE E ACABAMENTO DE PEITORIL	
1	Soleira/Filete em Mármore Bege Bahia Levigado
2	Soleira/Filete em Mármore Bege Bahia Escovado
3	Acabamento Peitoril em Mármore Bege Bahia Escovado
4	Soleira em Granito Marrom Imperial Polido
PAREDE	
1	Pintura externa na cor cinza a definir
2	Pintura Efeito Velvet na cor Recado de Amor, Coral
3	Pintura na cor Papel Picado, Suvinil
4	Pintura na cor Papel Picado, Suvinil
5	Ecogranito, Linha Grattano Linoe, Branco Geada
6	Pedra Moledo Branca
7	Porcelanato tipo Travertino, Acetinado, 120x120cm
8	Revestimento Branco Retificado Acetinado, 30x60cm
9	Porcelanato Portobello Anima di Marmo Acetinado 120x120cm
10	Porcelanato Incesa Marmo Blue 60x120cm
11	Porcelanato Ceusa Confete PK 100x100cm
12	Papel de parede modelo 1 a definir
13	Papel de parede modelo 2 a definir
14	Papel de parede modelo 3 a definir
15	Madeira Cumaru, réguas de 10cm
16	Azulejo tipo Hijau, 20x20cm
TETO/FORRO	
1	Teto/Forro em madeira existente
2	Teto/Forro pintado em efeito velvet na cor Recado de Amor, Coral
3	Teto/Forro pintado na cor Branco Neve

Sentido de assentamento


Rodapé h=15cm em Porcelanato tipo Travertino, Acetinado

Rodapé h=15cm em Poliestireno, com friso, na cor Fendi, Santa Luzia

Rodapé h=15cm em Porcelanato tipo cimento queimado, acetinado

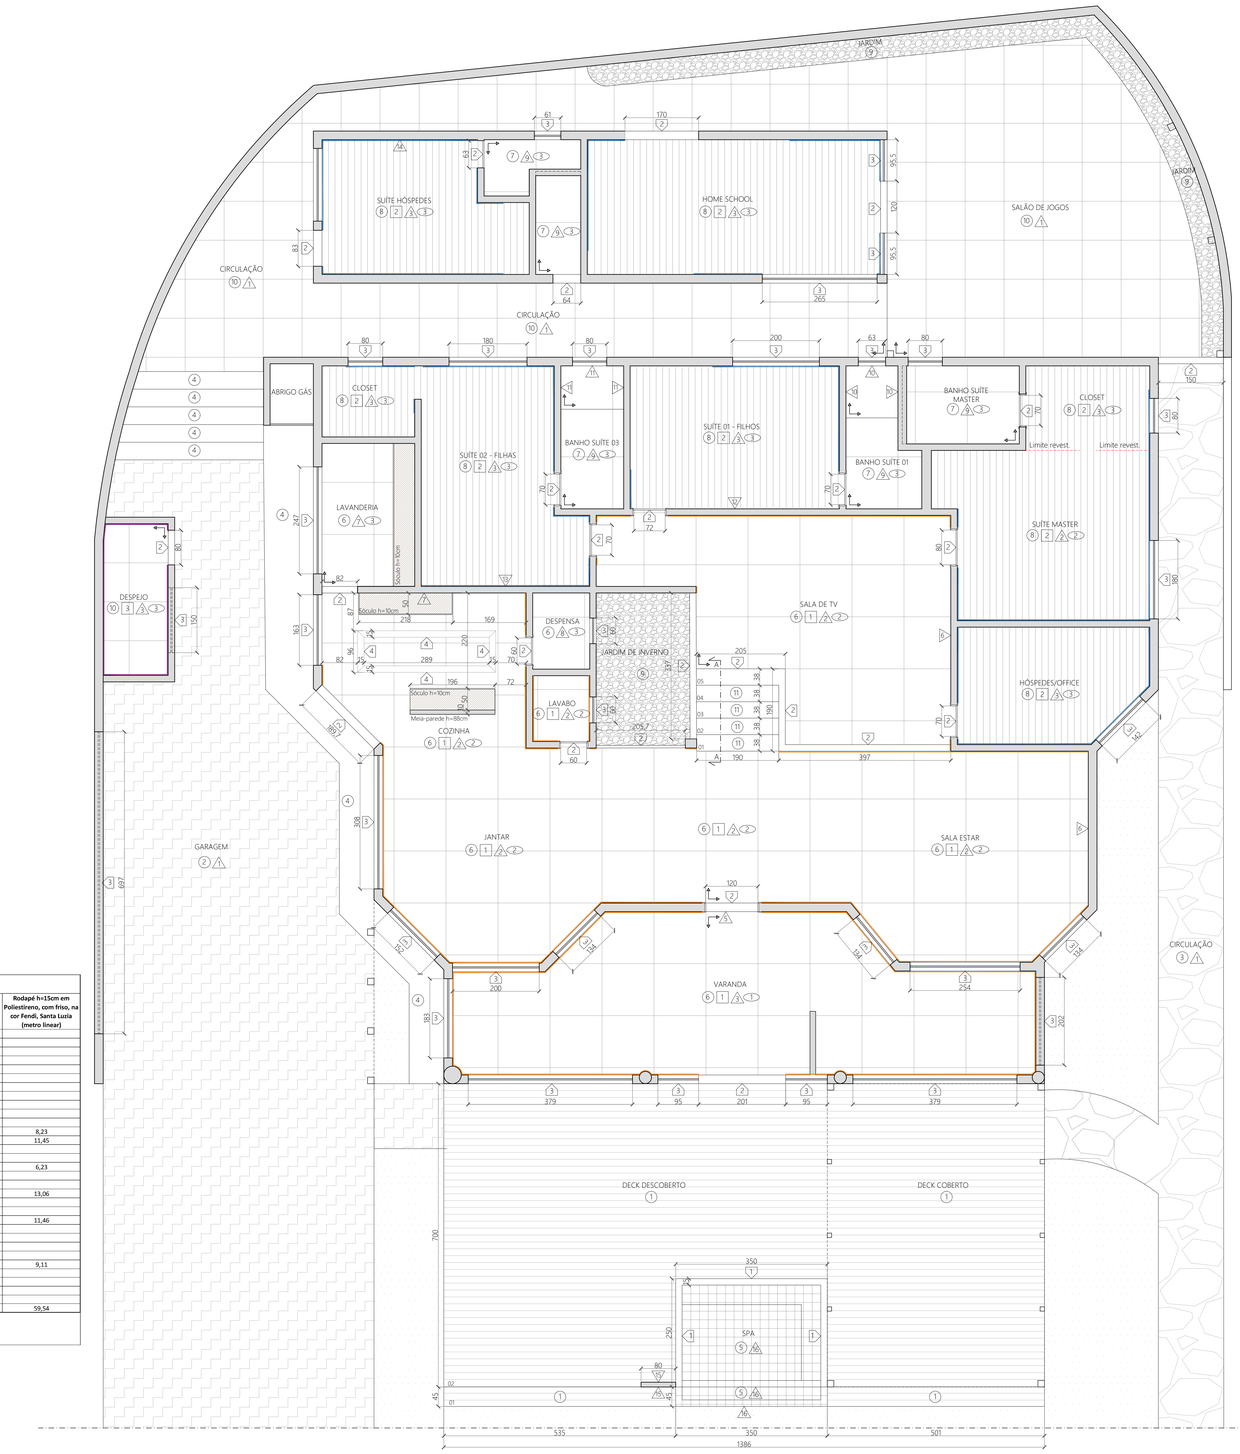

PLANTA DE ACABAMENTOS
ESC.: 1/50

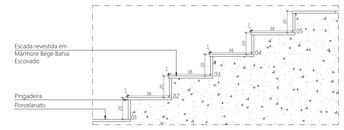

DETALHE 02 - CORTE AA
ESCADA
Esc.: 1/10

QUANTITATIVO DE ACABAMENTOS - REVESTIMENTOS

	Porcelanato tipo Travertino, Acetinado, 120x120cm (m²)	Porcelanato Portobello Anima di Marmo Acetinado 120x120cm (m²)	Piso Vinilico a definir (m²)	Porcelanato tipo cimento queimado Acetinado, 90x90cm (m²)	Azulejo tipo Hijau, 20x20cm (m²)	Ecogranito, Linha Grattano Linoe, Branco Geada (m²)	Revestimento Branco Retificado Acetinado, 30x60cm (m²)	Pedra Moledo Branca (m²)	Porcelanato Incesa Marmo Blue 60x120cm (m²)	Porcelanato Ceusa Confete PK 100x100cm (m²)	Rodapé h=15cm em Poliestireno, com friso, na cor Fendi, Santa Luzia (metro linear)
VARANDA - Piso e Rodapé	45,76										
VARANDA - Paredes						15,30					
SALA DE ESTAR, JANTAR E COZINHA - Piso e Rodapé	86,9										
SALA DE ESTAR, JANTAR E COZINHA - Paredes	13,25							13,43			
SALA DE TV - Piso e Rodapé	33,62										
SALA DE TV - Paredes								8,6			
LAVANDERIA - Piso	5,41										
LAVANDERIA - Paredes	37,1										
LAVABO - Piso e Rodapé	2,55										
DESPENSA - Piso	2,32										
DESPENSA - Paredes							21,74				
HÓSPEDES/OFFICE - Piso e Rodapé			11,12								8,23
SUÍTE MASTER - Piso e Rodapé			23,92								11,45
BANHO SUÍTE MASTER - Piso		4,68									
BANHO SUITE MASTER - Paredes		22,75									
SUÍTE 01 - FILHOS - Piso e Rodapé			16,02								6,23
BANHO SUÍTE 01 FILHOS - Piso		4,7									
BANHO SUITE 01 FILHOS - Paredes		16,4							9,9		
SUÍTE 02 FILHAS E CLOSET - Piso e Rodapé			20,67								13,06
BANHO SUÍTE 02 FILHAS - Piso		4,79									
BANHO SUITE 02 FILHAS - Paredes		15,17								9,4	
ANEXO SUÍTE HÓSPEDES - Piso e Rodapé			13,22								11,46
ANEXO BANHO SUÍTE HÓSPEDES - Piso		2,16									
ANEXO BANHO SUÍTE HÓSPEDES - Paredes		17,05									
ANEXO BANHO SOCIAL - Piso		2,37									
ANEXO BANHO SOCIAL - Paredes		16,2									
ANEXO HOME SCHOOL - Piso e Rodapé			21,05								9,11
ANEXO JOGOS - Piso				64,02							
ANEXO CIRCULAÇÃO EXTERNA - Piso				37,38							
SPA					19						
DESPEJO				6,62							
TOTAL	226,91	106,27	106	108,02	19	15,3	21,74	22,03	9,9	9,4	59,54

Observações:
1. O quantitativo não contempla porcentagem de perda, a taxa de perda deverá ser acrescida aos valores no momento do orçamento e/ou compra;
2. Não foram consideradas no quantitativo as metragens de soleiras, revestimentos em granitos e de itens de marmoraria;
3. Todas as medidas e metragens deverão ser conferidas no local.

LUIZA PACHECO ARQUITETURA
Luiza Pacheco
CAU: A69902-6
(31) 98885-1403
luiza@luizapacheco.com.br
www.luizapacheco.com.br

Todas as medidas devem ser conferidas no local antes da execução;
Cotas em centímetros (salvo onde há informação de uso de outras medidas);
Todos os direitos autorais reservados ao escritório;
Em caso de dúvidas ou necessidade de alterações durante a execução, contatar o escritório de arquitetura.

CLIENTE: Gustavo Raposo
ENDEREÇO: Condomínio Vale dos Pinhais, Nova Lima, MG

EXECUTIVO
PLANTA DE ACABAMENTOS

Revisão: 00
Março, 2026

07/75

Formato: A0