
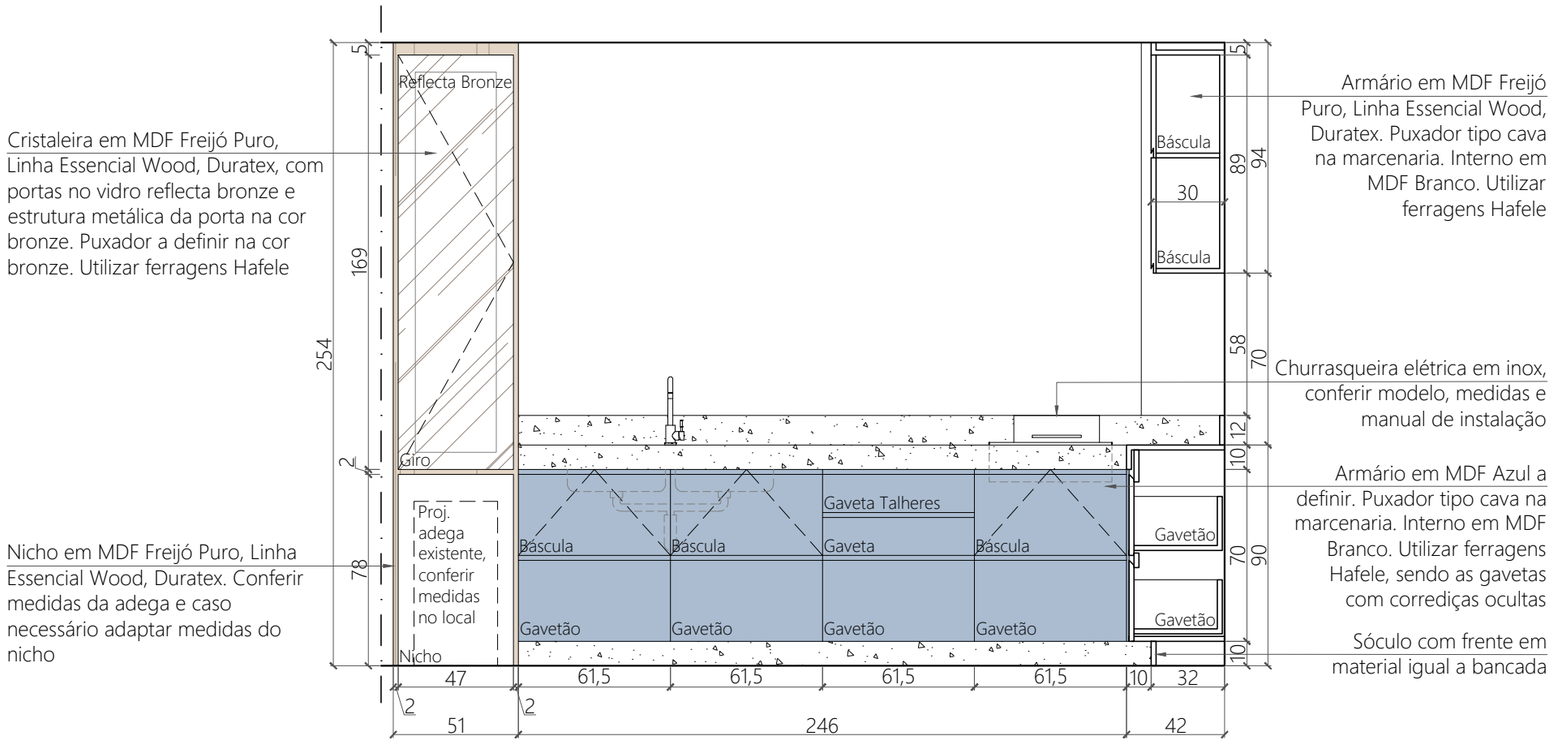


GOURMET
ELEVAÇÃO A
VISTA EXTERNA ARMÁRIO
Esc.: 1/25

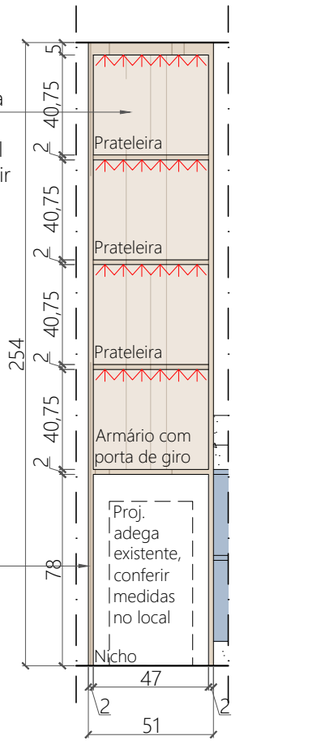

GOURMET
ELEVAÇÃO A
VISTA INTERNA ARMÁRIO
Esc.: 1/25

LUIZA PACHECO ARQUITETURA
Luiza Pacheco
CAU: A69992-6
(31) 98885-1403
luiza@luizapacheco.com.br
www.luizapacheco.com.br

Todas as medidas devem ser conferidas no local antes da execução;
Cotas em centímetros (salvo onde há informação de uso de outras medidas);
Todos os direitos autorais reservados ao escritório;
Em caso de dúvidas ou necessidade de alterações durante a execução, contatar o escritório de arquitetura.

CLIENTE: Haverson Soares
ENDEREÇO: Rua Jatobás, 125 - Residencial Árvores - Alphaville - Nova Lima/MG

EXECUTIVO
GOURMET - ELEVAÇÃO

Revisão: 00
Outubro, 2026