



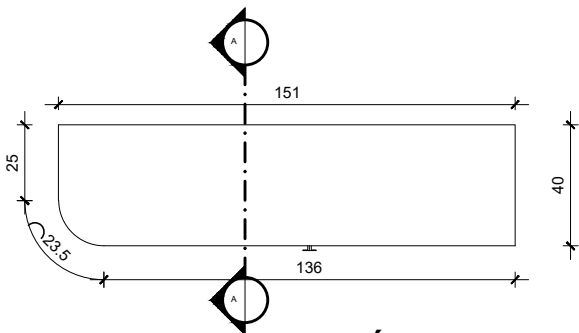


PLANTA - ARMÁRIO SAPATEIRA

ESCALA 1:25

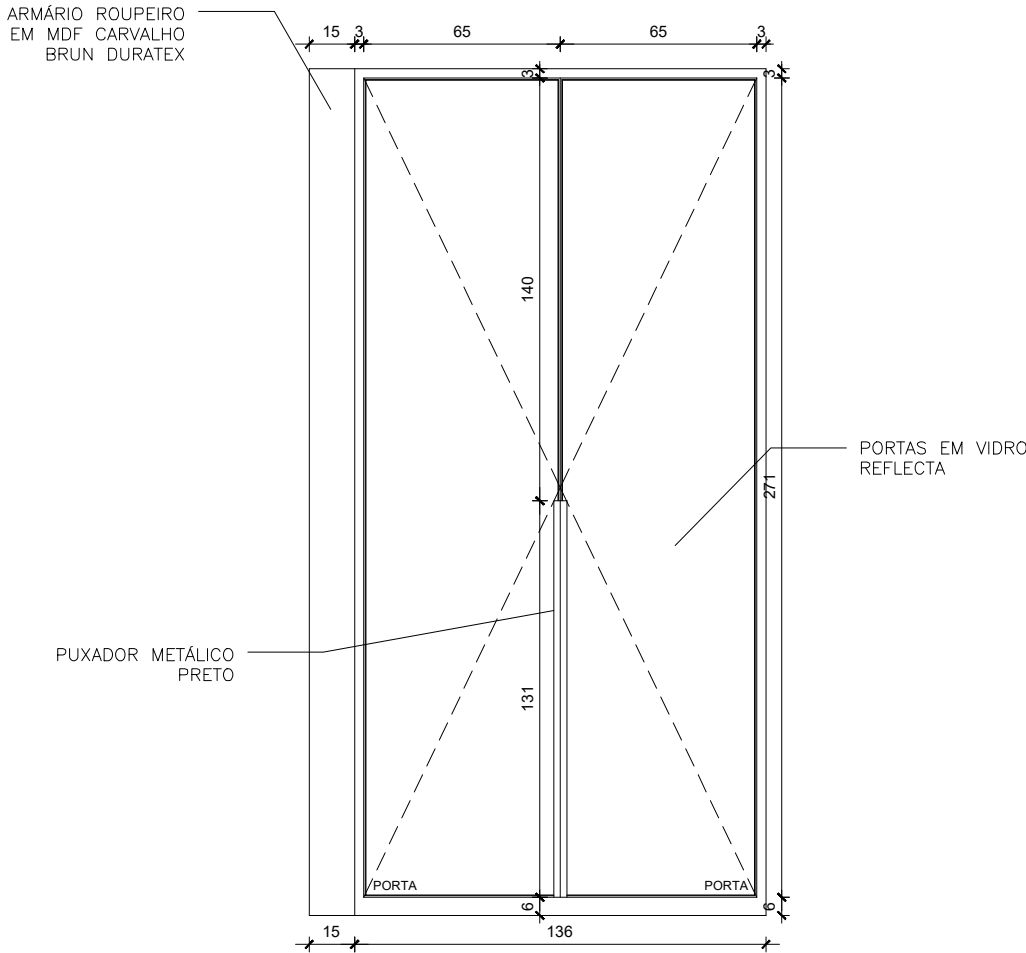


ELEVAÇÃO FRONTAL - ARMÁRIO ROUPEIRO

ESCALA 1:25

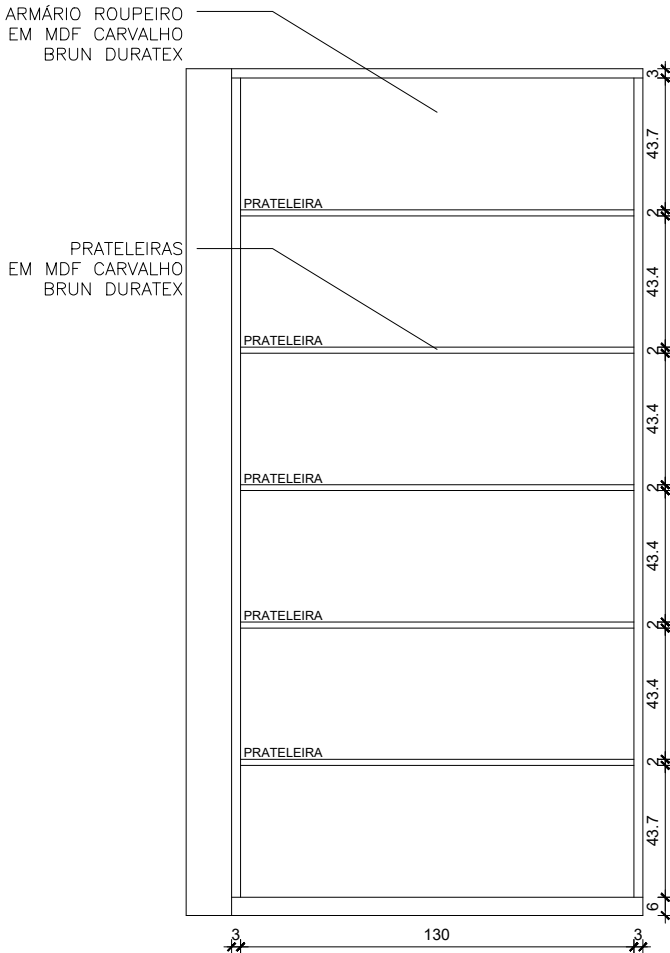


ELEVAÇÃO FRONTAL INTERNO - ARMÁRIO ROUPEIRO

ESCALA 1:25

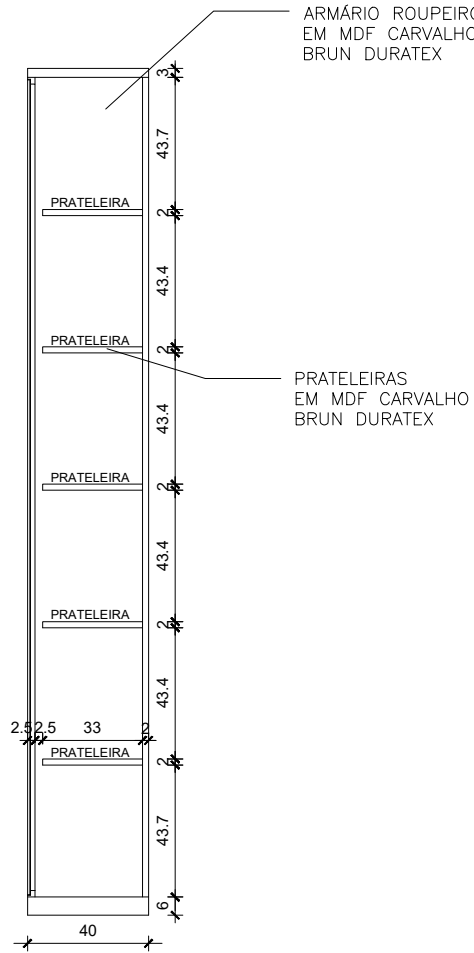


CORTE AA - ARMÁRIO ROUPEIRO

ESCALA 1:25

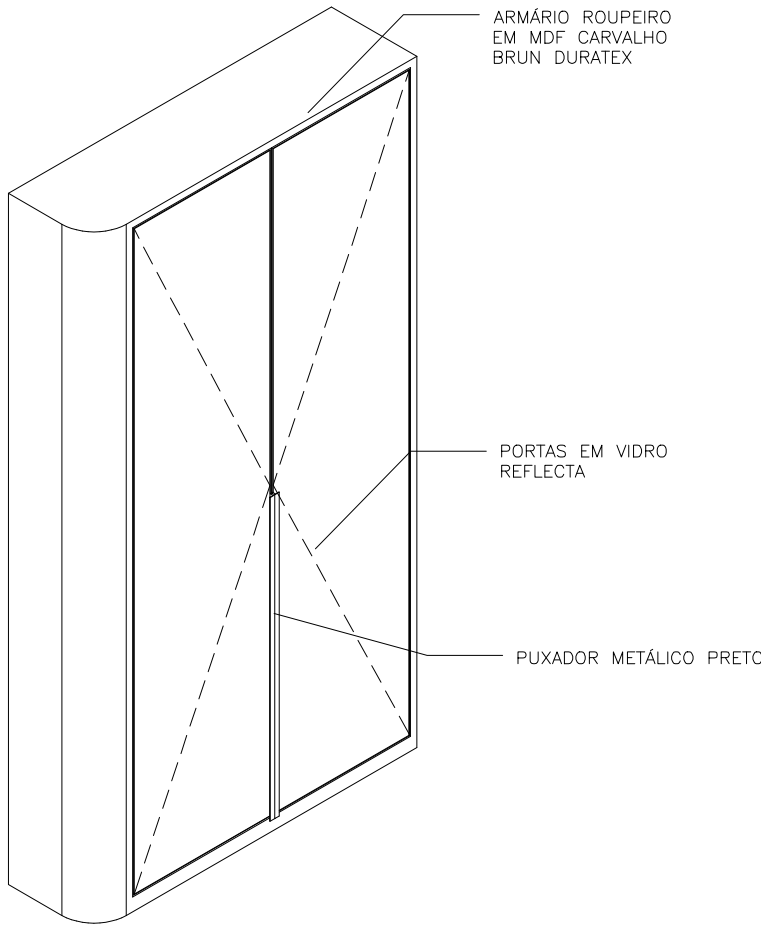

ISOMÉTRICA - ARMÁRIO ROUPEIRO


ESCALA 1:25

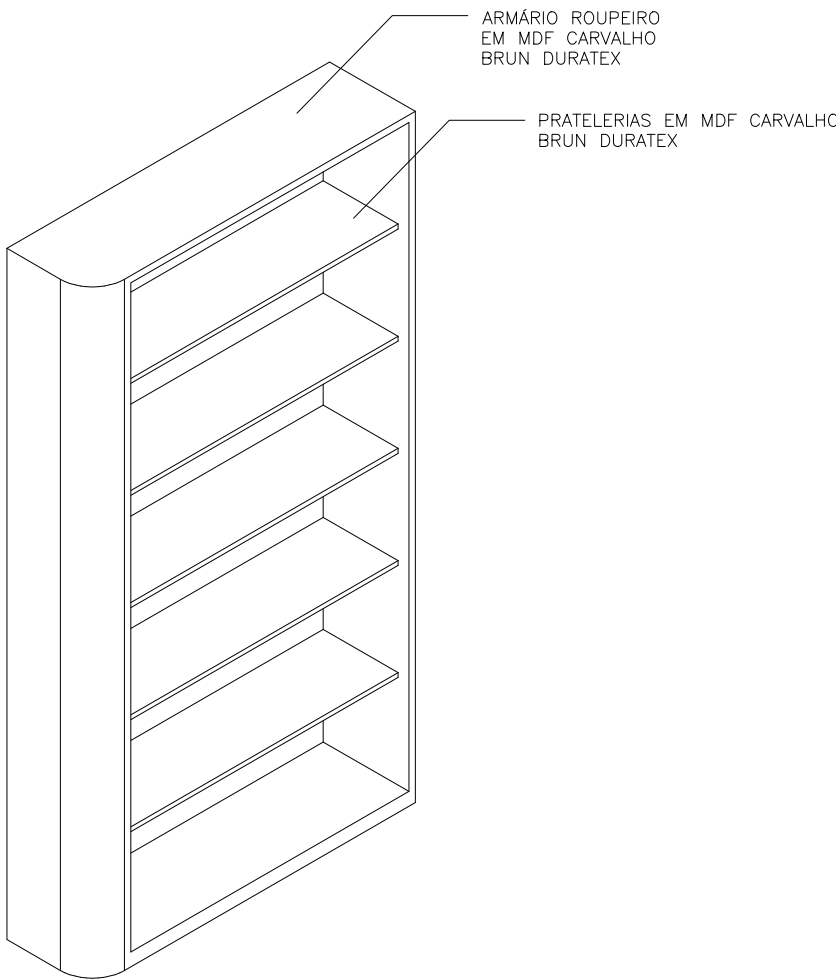


ISOMÉTRICA INTERNO - ARMÁRIO ROUPEIRO

ESCALA 1:25


	TÍTULO:	
	DETALHAMENTO SUÍTE	
	RT:	PRANCHA 22
	ARQUIVO:	DATA: 07/2026
CONTEÚDO: ARMARIO ROUPEIRO SUITE		

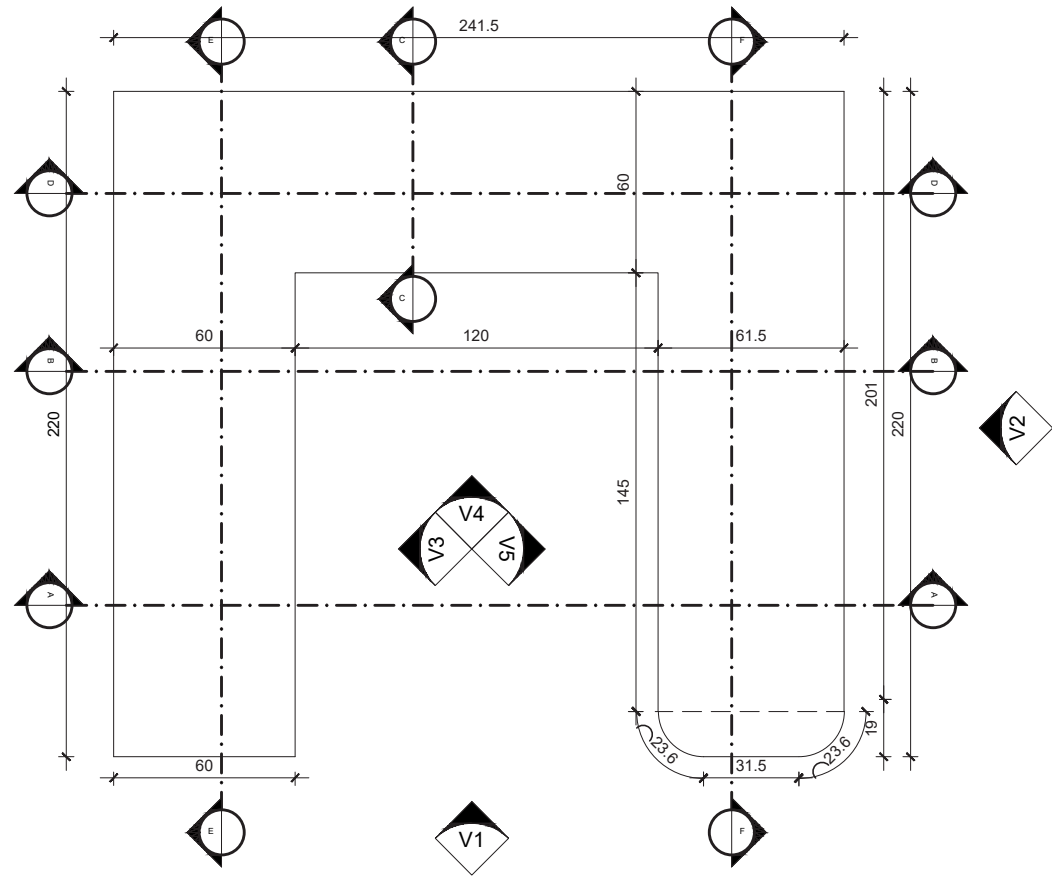


PLANTA - CLOSET
ESCALA 1:25

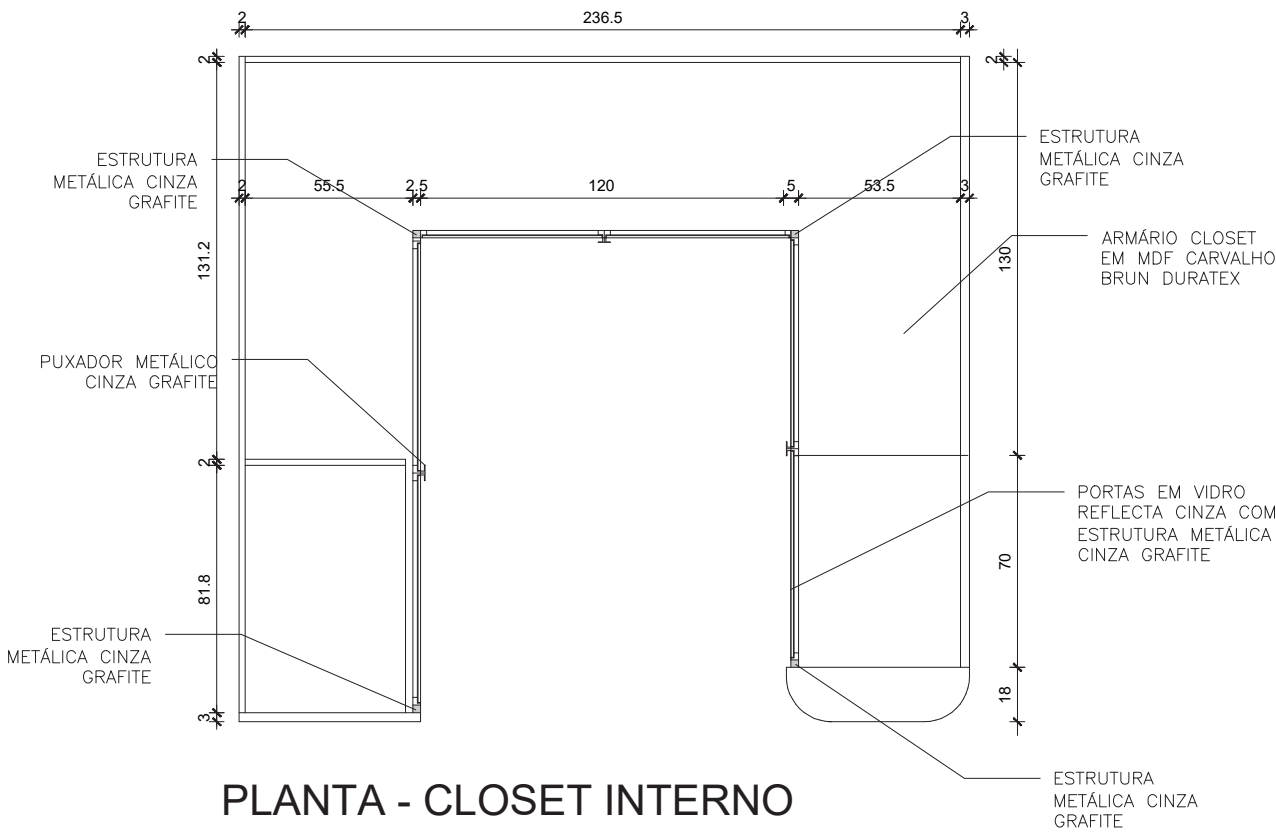


PLANTA - CLOSET INTERNO
ESCALA 1:25

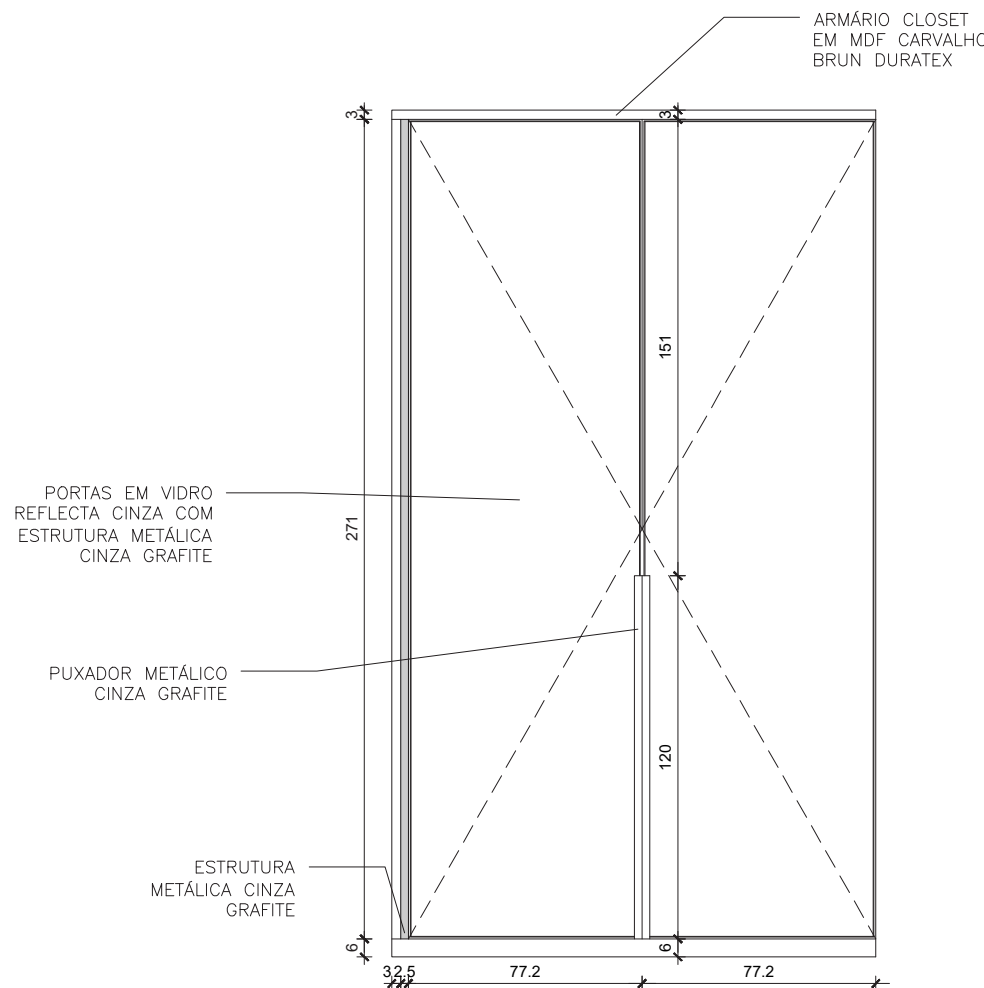


ELEVAÇÃO V3
ESCALA 1:25

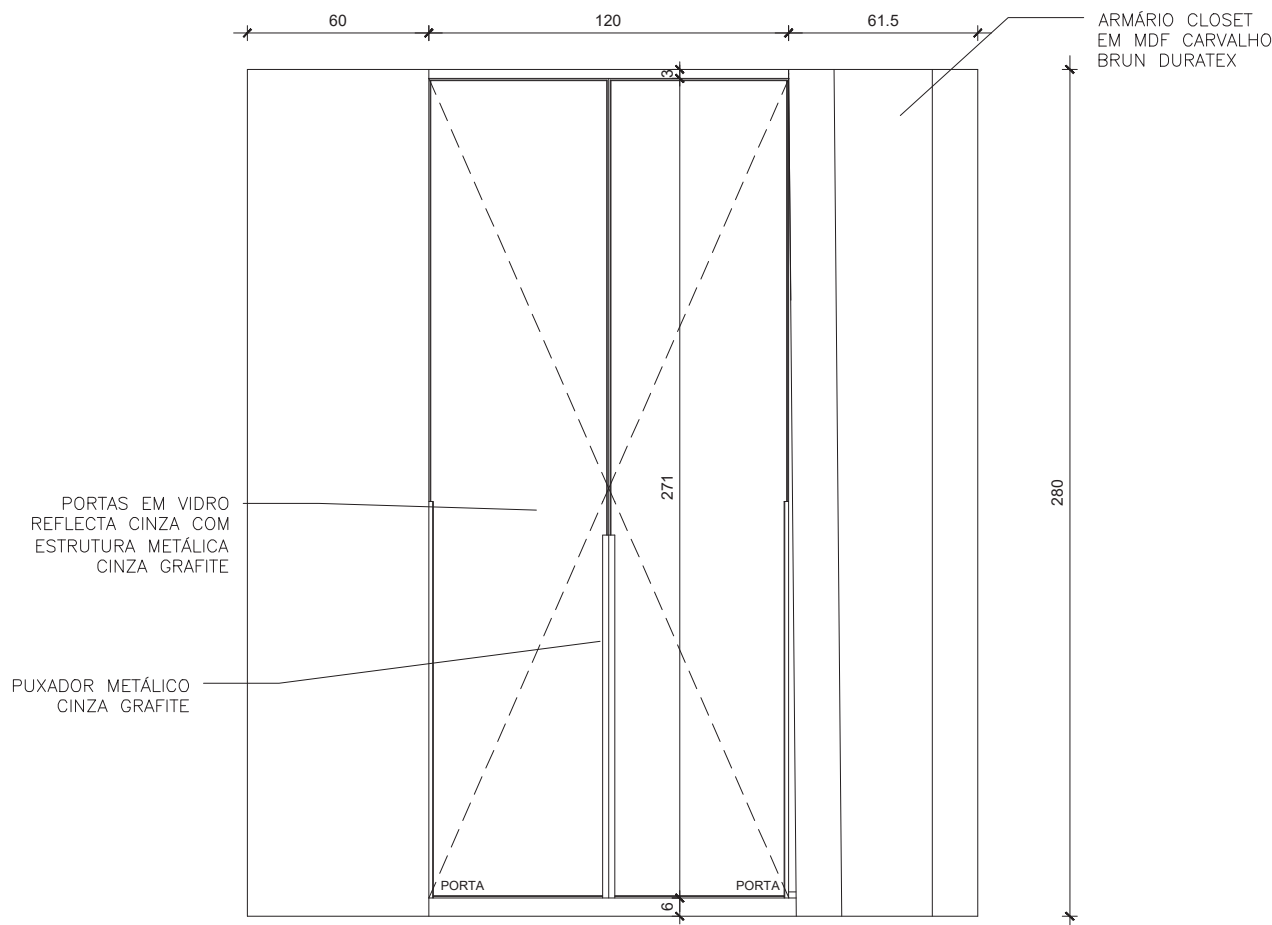

ELEVAÇÃO V1
ESCALA 1:25

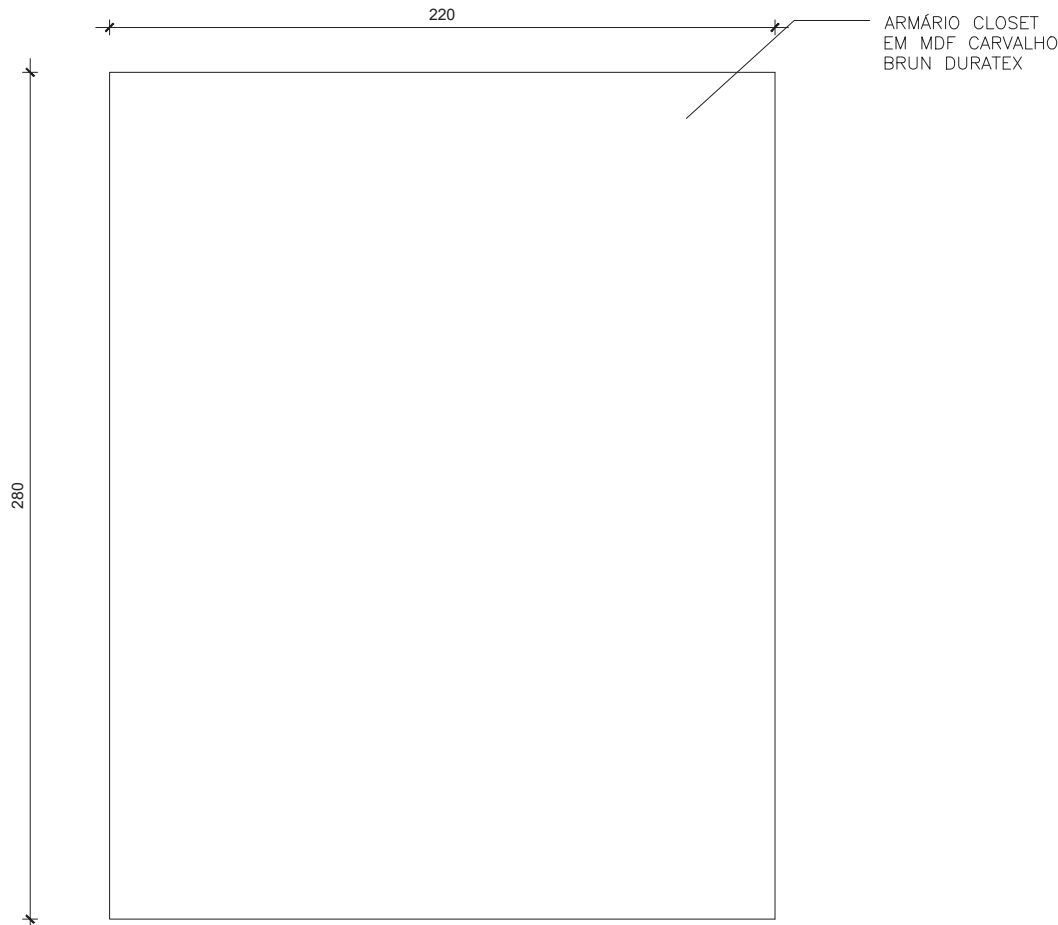


ELEVAÇÃO V2
ESCALA 1:25

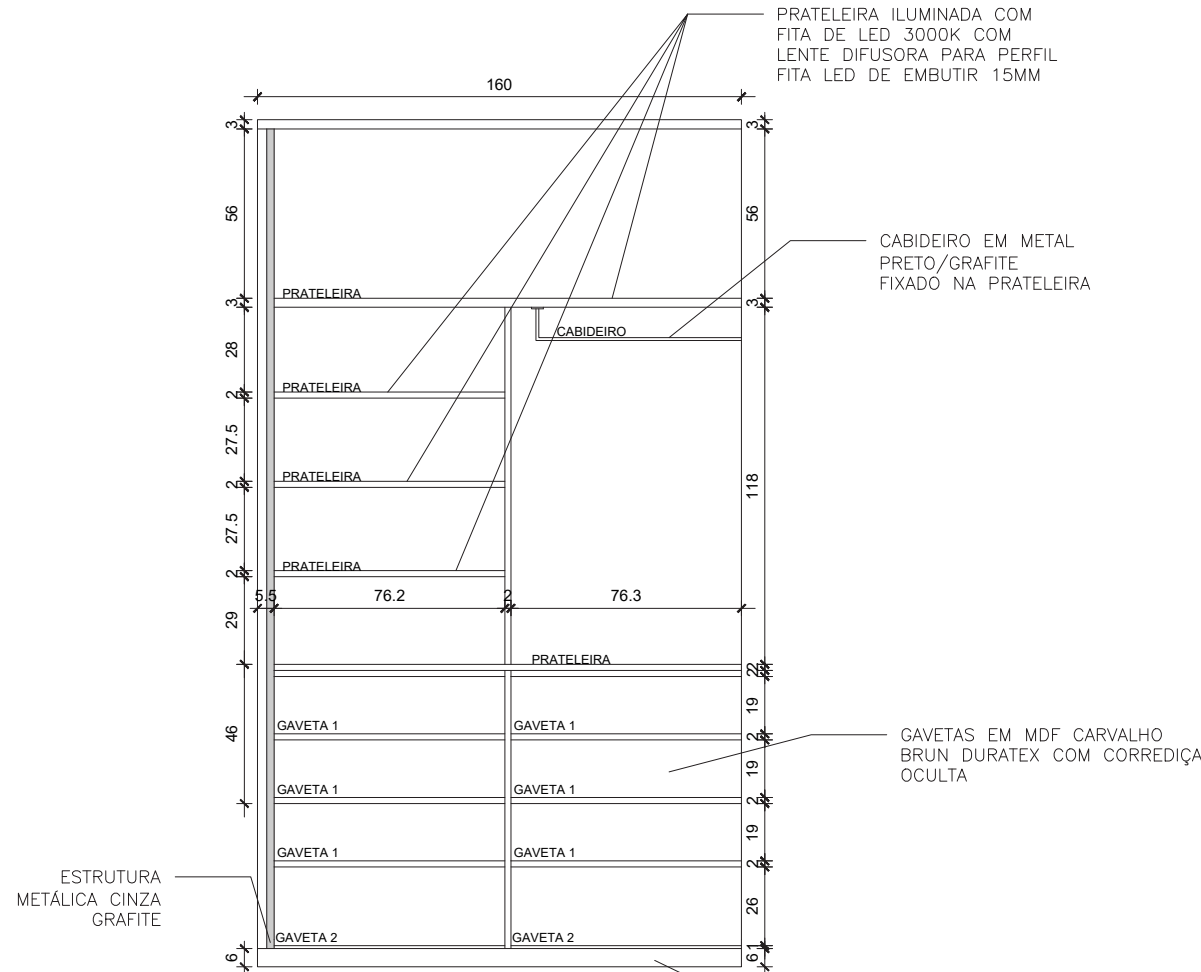


ELEVAÇÃO V3 - INTERNO
ESCALA 1:25


	TÍTULO:	
	DETALHAMENTO SUÍTE	
	RT:	PRANCHA 23
	ARQUIVO:	DATA: 07/2026
	CONTEÚDO: ARMARIO CLOSET PLANTAS, ELEVAÇÕES V1 V2 E V3	

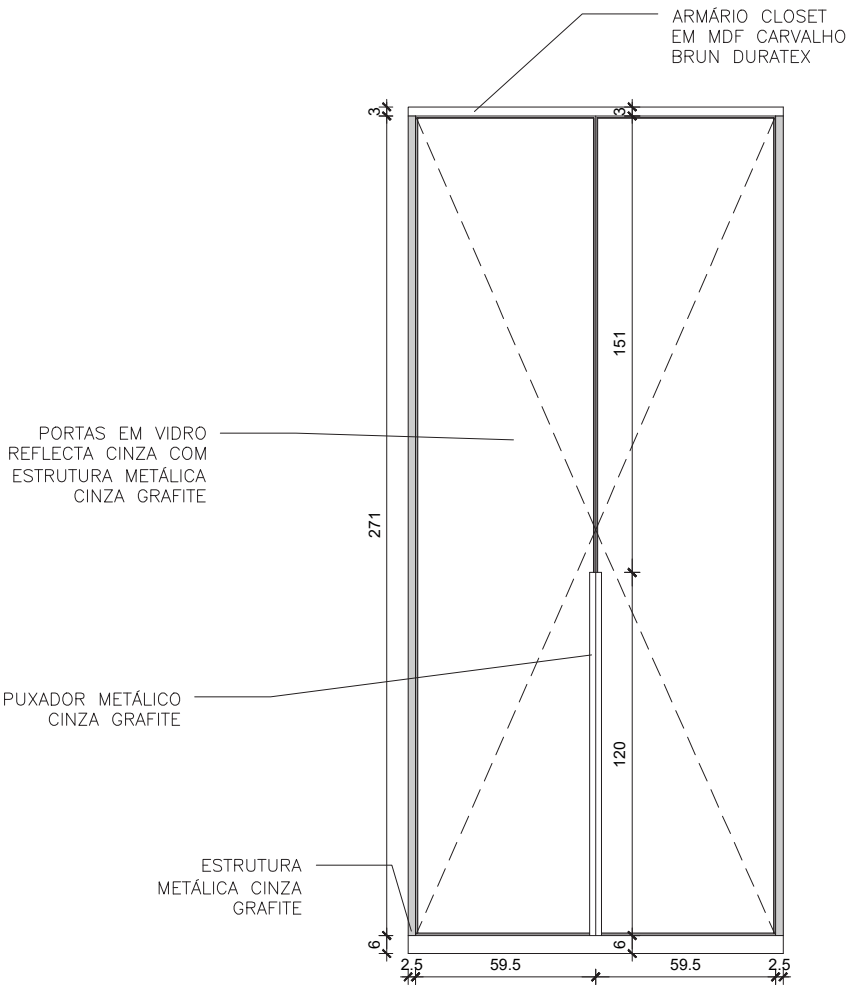


ELEVAÇÃO V4
ESCALA 1:25

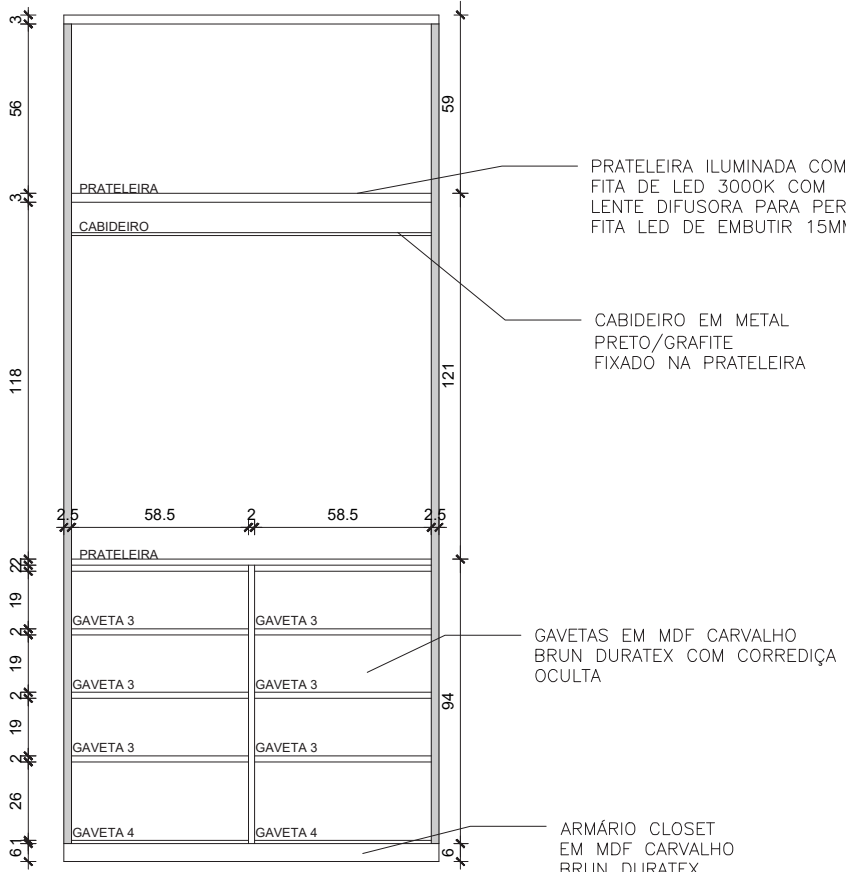


ELEVAÇÃO V4 - INTERNO
ESCALA 1:25

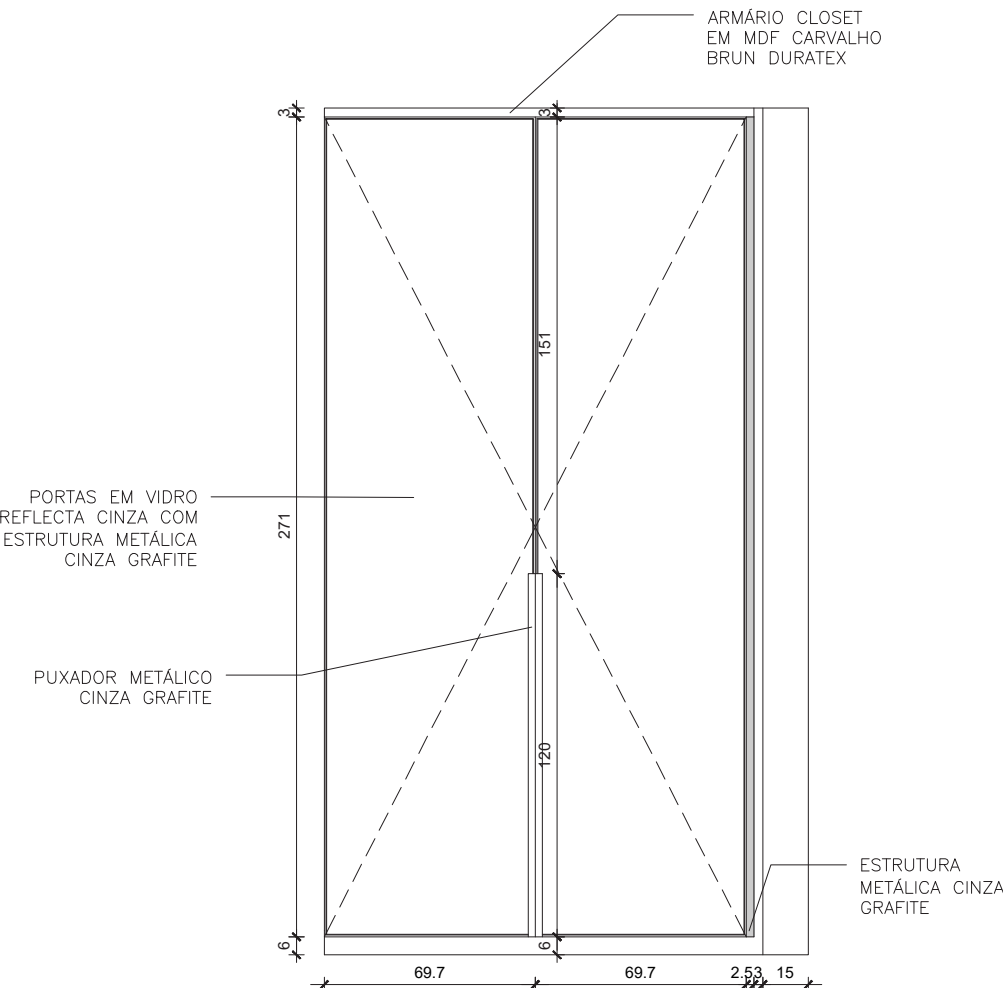


ELEVAÇÃO V5
ESCALA 1:25

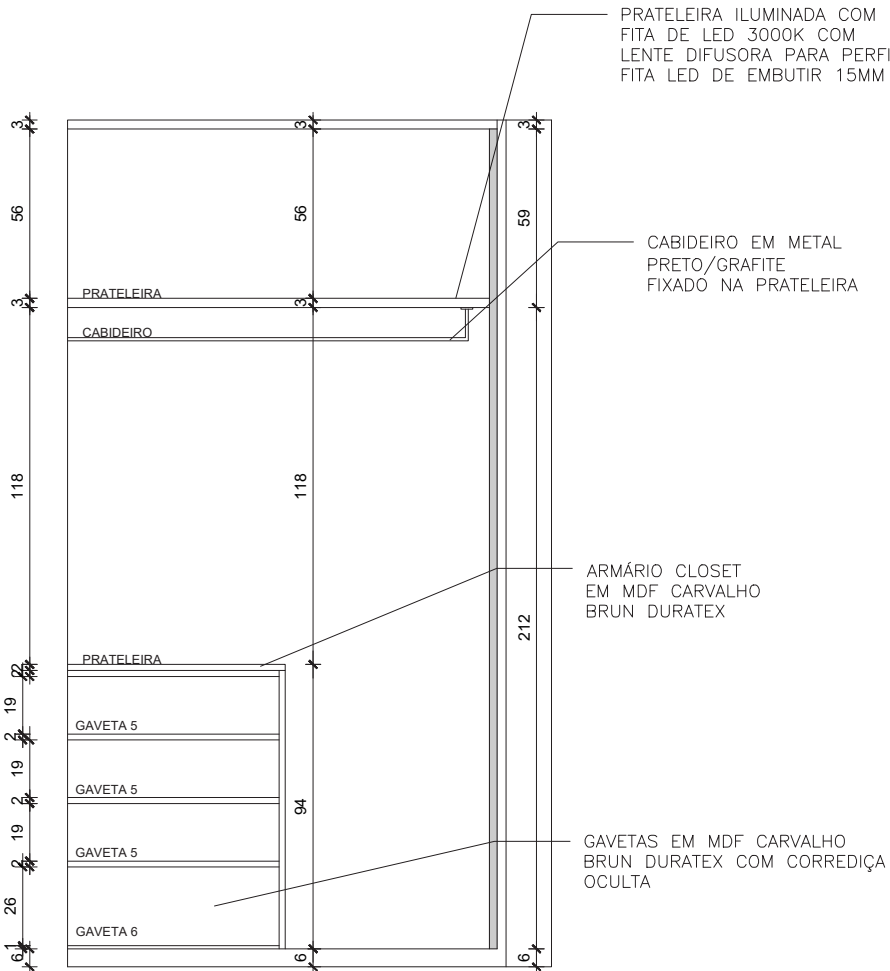


ELEVAÇÃO V5 - INTERNO
ESCALA 1:25

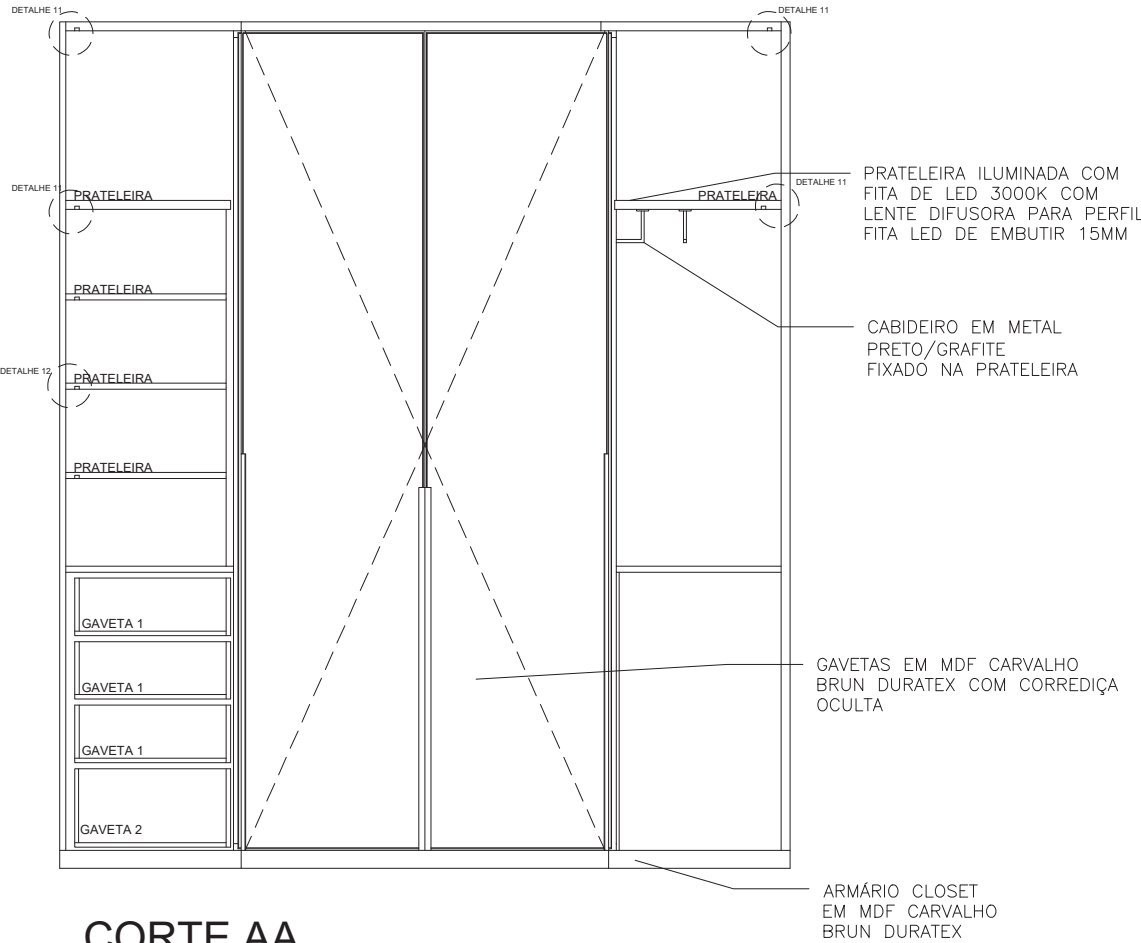


CORTE AA
ESCALA 1:25

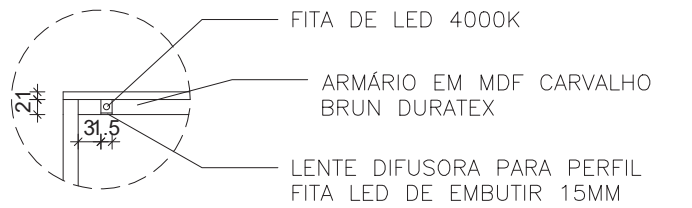

DETALHE 11 - FITA DE LED CLOSET
ESCALA 1:10

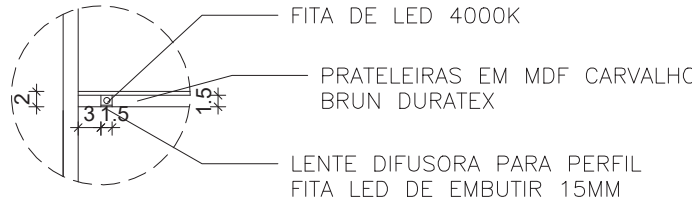

DETALHE 12 - FITA DE LED PRATELEIRAS
ESCALA 1:10

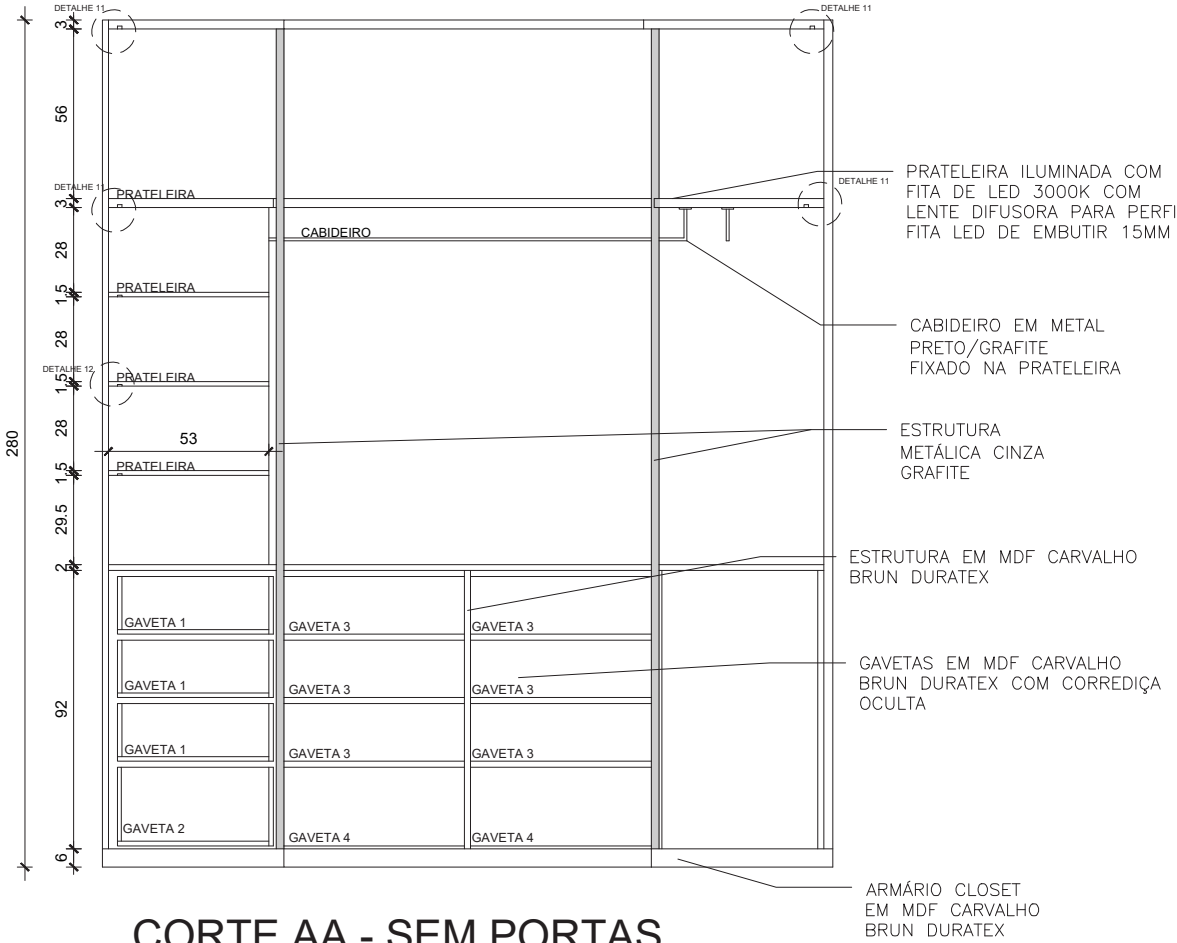

CORTE AA - SEM PORTAS
ESCALA 1:25

	TÍTULO:	
	DETALHAMENTO SUÍTE	
	RT:	PRANCHA 24
	ARQUIVO:	DATA: 07/2026
	CONTEÚDO: ARMARIO CLOSET ELEVAÇÕES V4 E V5 CORTE AA, DETALHES 11E 12	