
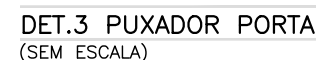


IMAGEM REFERENTE A
ETAPA DE
ANTEPROJETO
PREVALECE PROJETO
EXECUTIVO

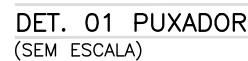



- CONSIDERAR DOBRADIÇAS E CORREDIÇAS COM AMORTECIMENTO
- VERIFICAR LOCAÇÕES DAS FITAS LED, TOMADAS E INTERRUPTORES NOS MÓVEIS;
- ARMÁRIOS INTERNOS EM MDF BRANCO, EXTERNO SEQUIPEER INDICAÇÃO OU 3D;
- CONSULTAR MANUAIS DE INSTALAÇÃO PARA TODOS OS EQUIPAMENTOS;
- CONFERIR MEDIDAS/NÍVEIS EM OBRA ANTES DE EXECUTAR O PROJETO

DATA: | R02
NOV/2025

83

ARQUITETA RESPONSÁVEL : GIULIA SIMONETTI
CAU: A145599-0

ARQUITETA RESPONSÁVEL : GIULIA SIMONETTI
CAU: A145599-0

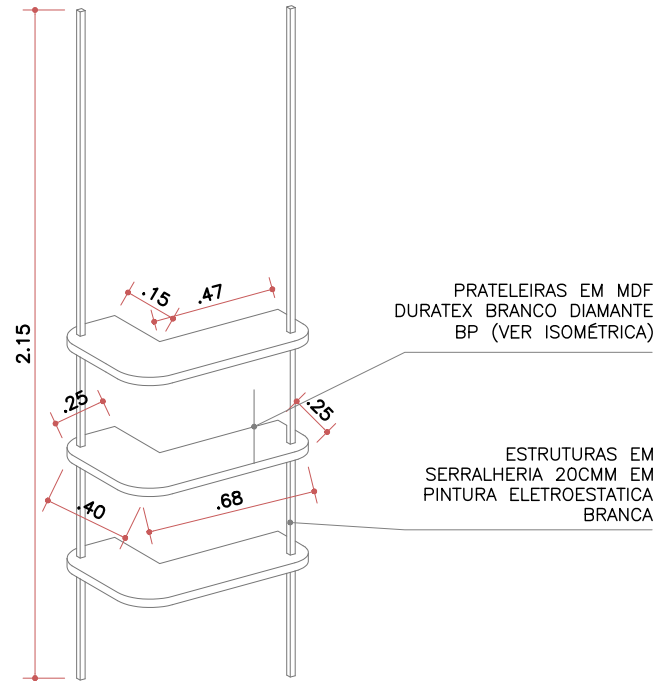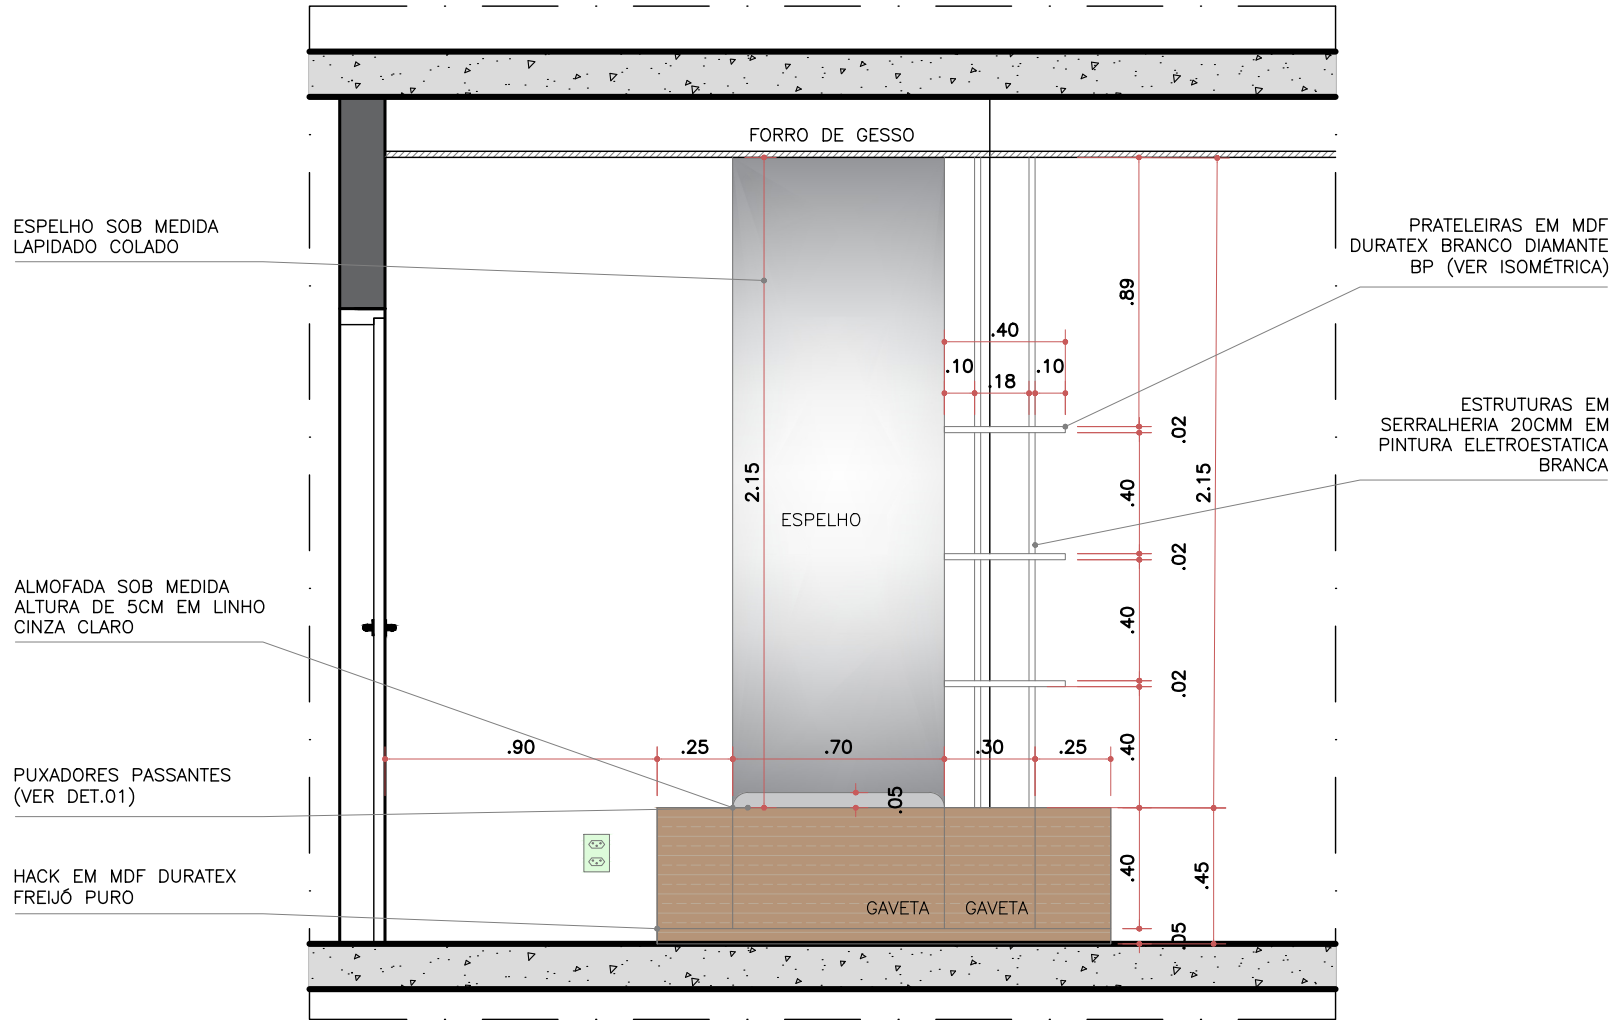

ISOMETRICA PRATELEIRA S/ESCALA

VISTA 02 LIVING – TV
ESC. 1:25

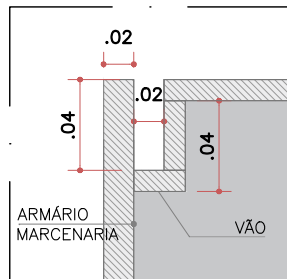


IMAGEM 3D LIVING
S/ ESCALA

IMAGEM REFERENTE A
ETAPA DE
ANTEPROJETO
PREVALECE PROJETO
EXECUTIVO



MDF DURATEX FREIJÓ
PURO



DET. 01 PUXADOR
(SEM ESCALA)

NOTA DE MARCENARIA

- CONSIDERAR DOBRADIÇAS E CORREDIÇAS COM AMORTECIMENTO
- VERIFICAR LOCAÇÕES DAS FITAS LED, TOMADAS E INTERRUPTORES NOS MÓVEIS;
- ARMÁRIOS INTERNOS EM MDF BRANCO, EXTERNO SEGUIR INDICAÇÃO OU 3D;
- CONSULTAR MANUAIS DE INSTALAÇÃO PARA TODOS OS EQUIPAMENTOS;
- CONFERIR MEDIDAS/NIVEIS EM OBRA ANTES DE EXECUTAR O PROJETO

CLIENTE: LUCAS E ANA

ÁREA:
168,61 M²

ESCALA:
INDICADA

DATA:
NOV/2025

R02

LOCAL:
BELO HORIZONTE - BR

CONTEÚDO:
MARCENARIA LIVING

PROJETO EXECUTIVO : BRUNO SORIANO
CAU: A227819-0


PRANCHA:

43

83

ARQUITETA RESPONSÁVEL : GIULIA SIMONETTI
CAU: A145599-0

SGhaus
.arq

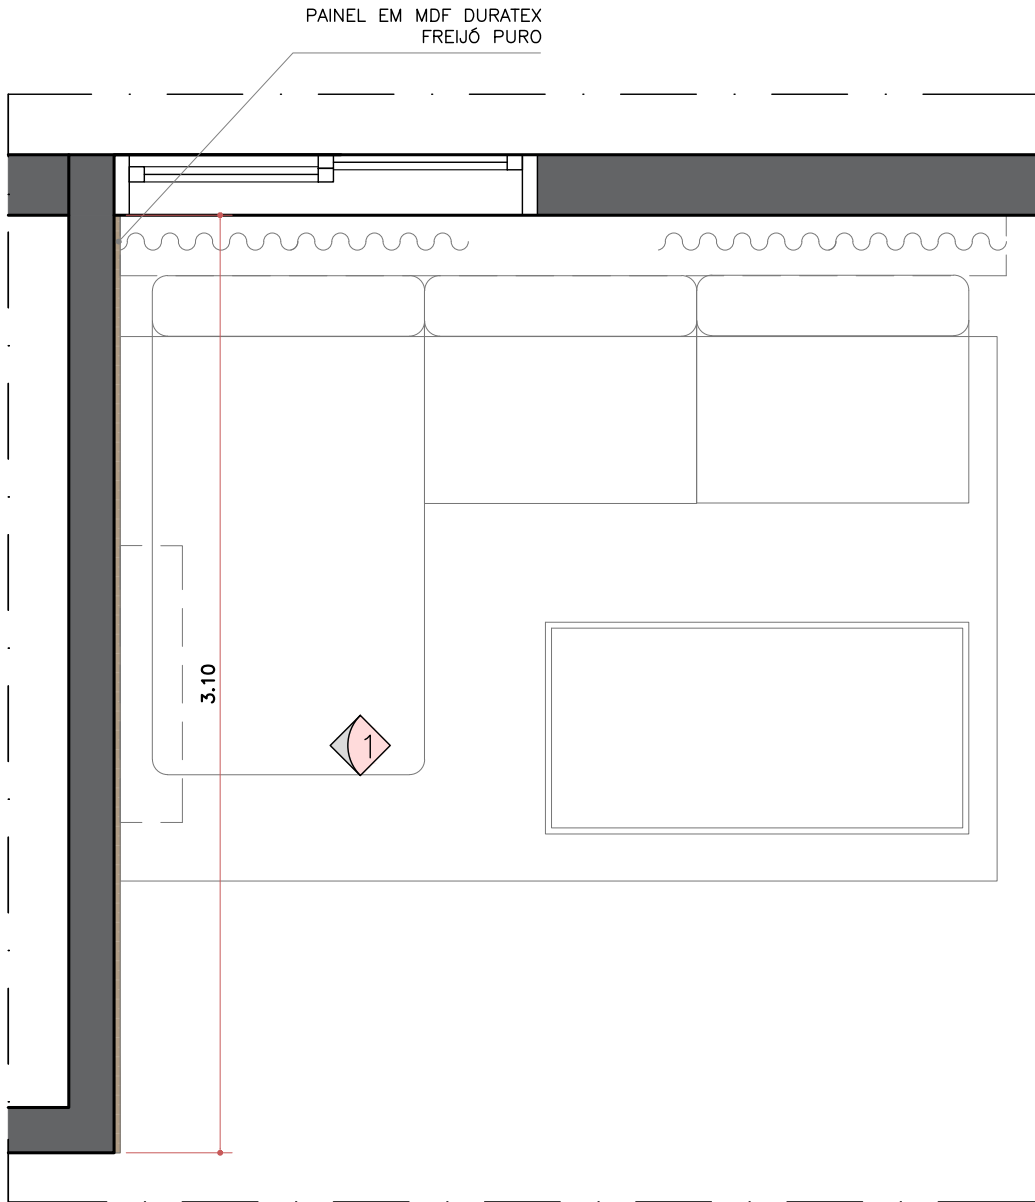


PLANTA LIVING – SOFÁ
ESC. 1:25



IMAGEM 3D LIVING
S/ ESCALA

IMAGEM REFERENTE A
ETAPA DE
ANTEPROJETO
PREVALECE PROJETO
EXECUTIVO

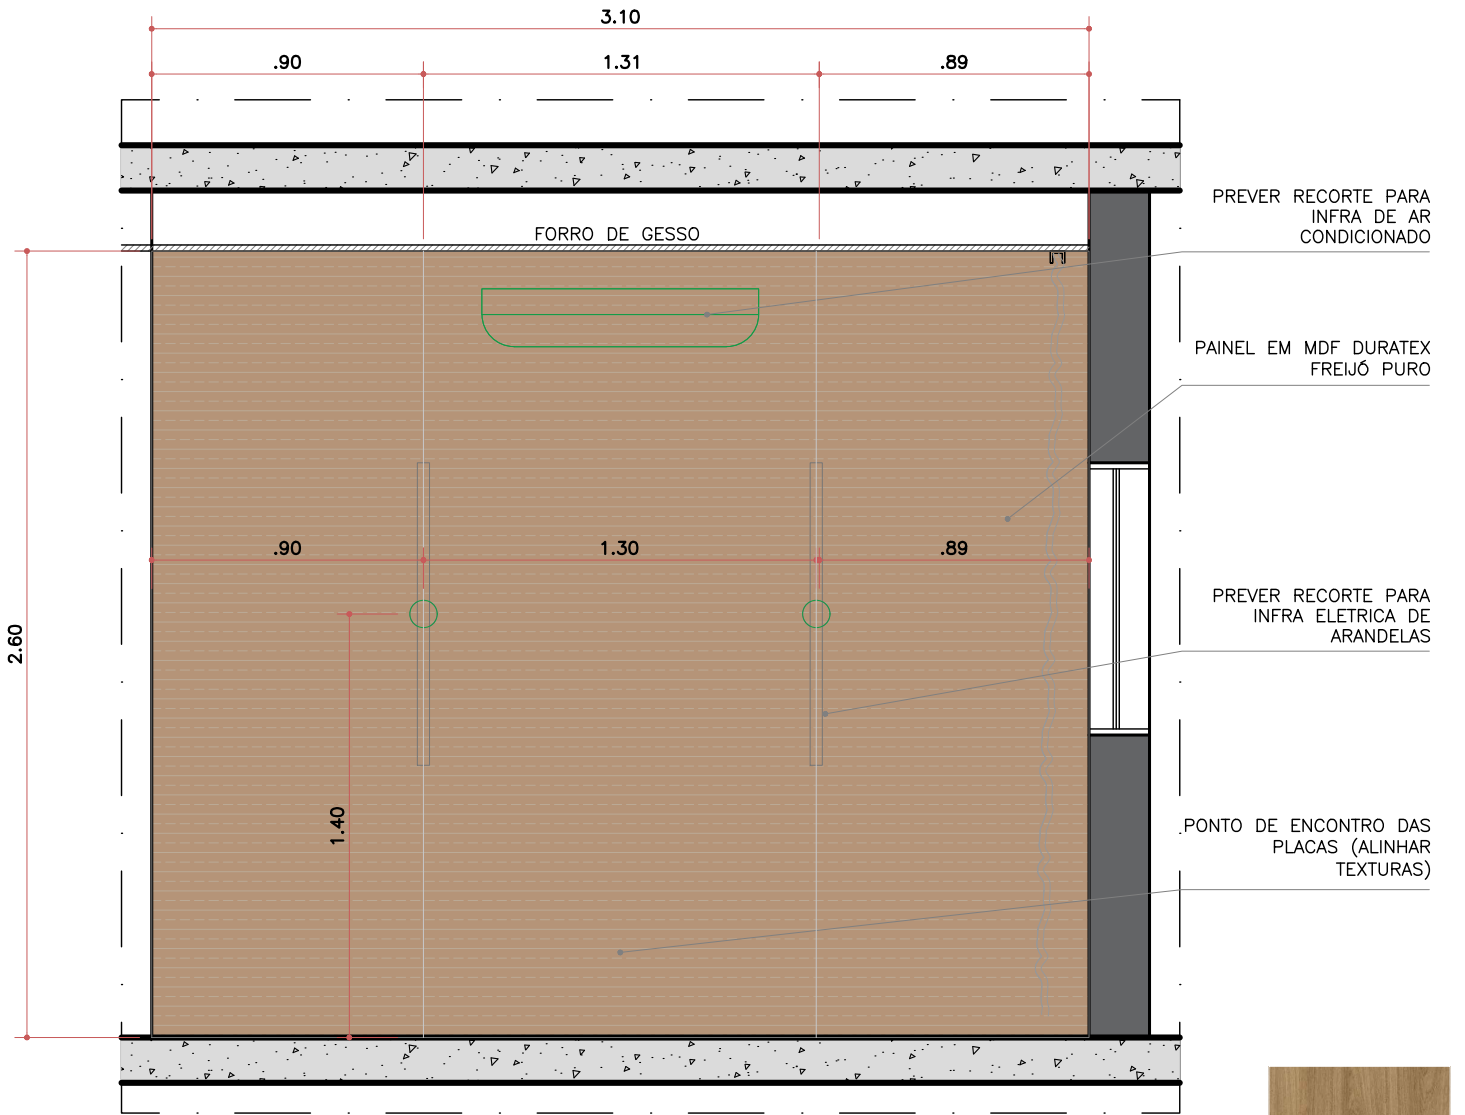

VISTA 01 LIVING – SOFÁ
ESC. 1:25



MDF DURATEX FREIJÓ
PURO

NOTA DE MARCENARIA

- CONSIDERAR DOBRADIÇAS E CORREDIÇAS COM AMORTECIMENTO
- VERIFICAR LOCAÇÕES DAS FITAS LED, TOMADAS E INTERRUPTORES NOS MÓVEIS;
- ARMÁRIOS INTERNOS EM MDF BRANCO, EXTERNO SEGUIR INDICAÇÃO OU 3D;
- CONSULTAR MANUAIS DE INSTALAÇÃO PARA TODOS OS EQUIPAMENTOS;
- CONFERIR MEDIDAS/NÍVEIS EM OBRA ANTES DE EXECUTAR O PROJETO

CLIENTE: LUCAS E ANA

ÁREA:
168,61 M²

ESCALA:
INDICADA

DATA:
NOV/2025

R02

LOCAL:
BELO HORIZONTE - BR

CONTEÚDO:
MARCENARIA LIVING

PROJETO EXECUTIVO : BRUNO SORIANO
CAU: A227819-0

PRANCHA:

44

83

ARQUITETA RESPONSÁVEL : GIULIA SIMONETTI
CAU: A145599-0

