
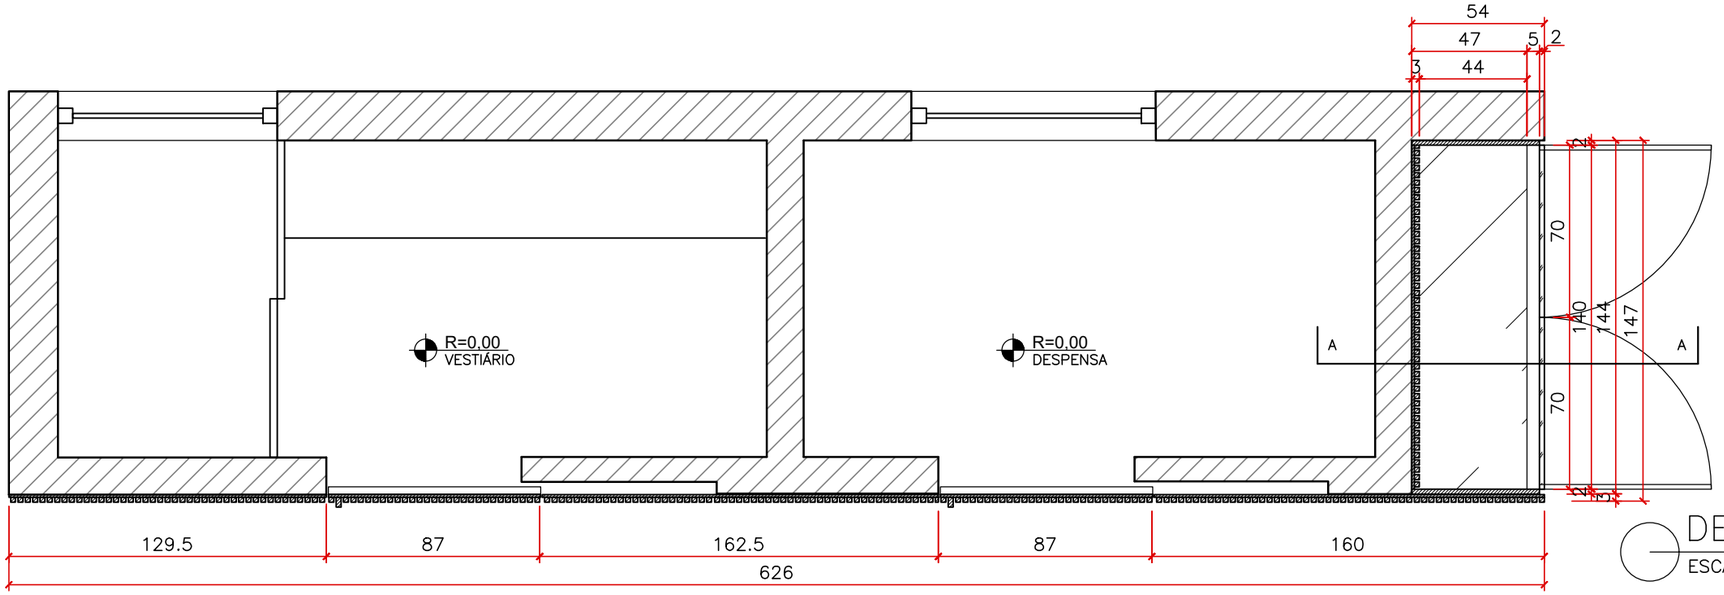



PLANTA PAINEL RIPADO E CRISTALEIRA

ESCALA 1:25

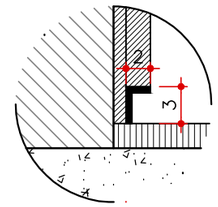


DET.CORTE RODAPÉ PAINEL

ESCALA 1:5

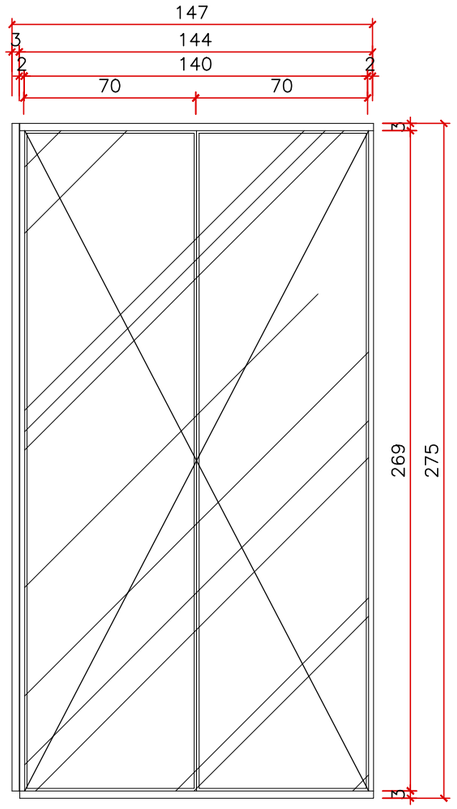


ELEVAÇÃO CRISTALEIRA FECHADA

ESCALA 1:25

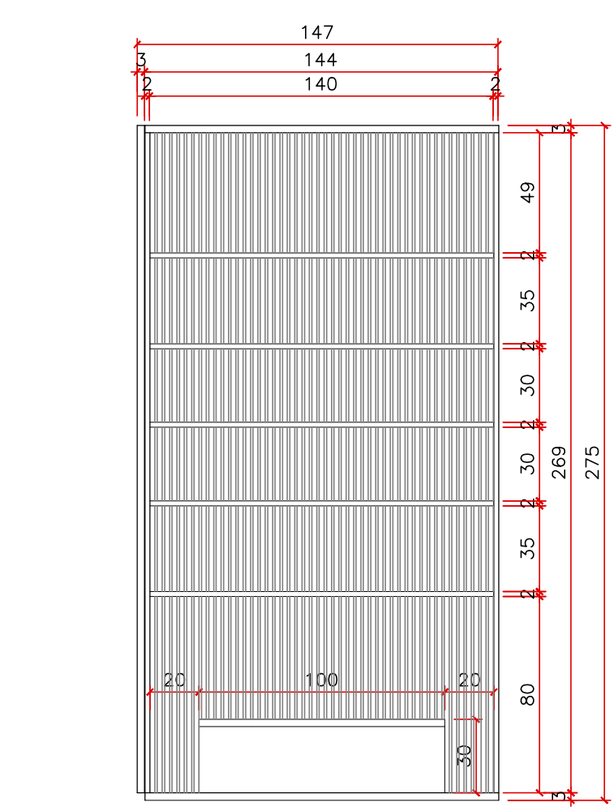

ELEVAÇÃO CRISTALEIRA ABERTA

ESCALA 1:25

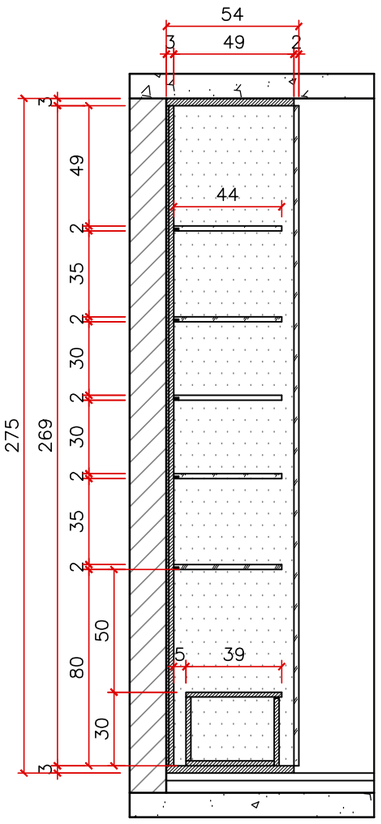

CORTE AA CRISTALEIRA

ESCALA 1:25

A3