
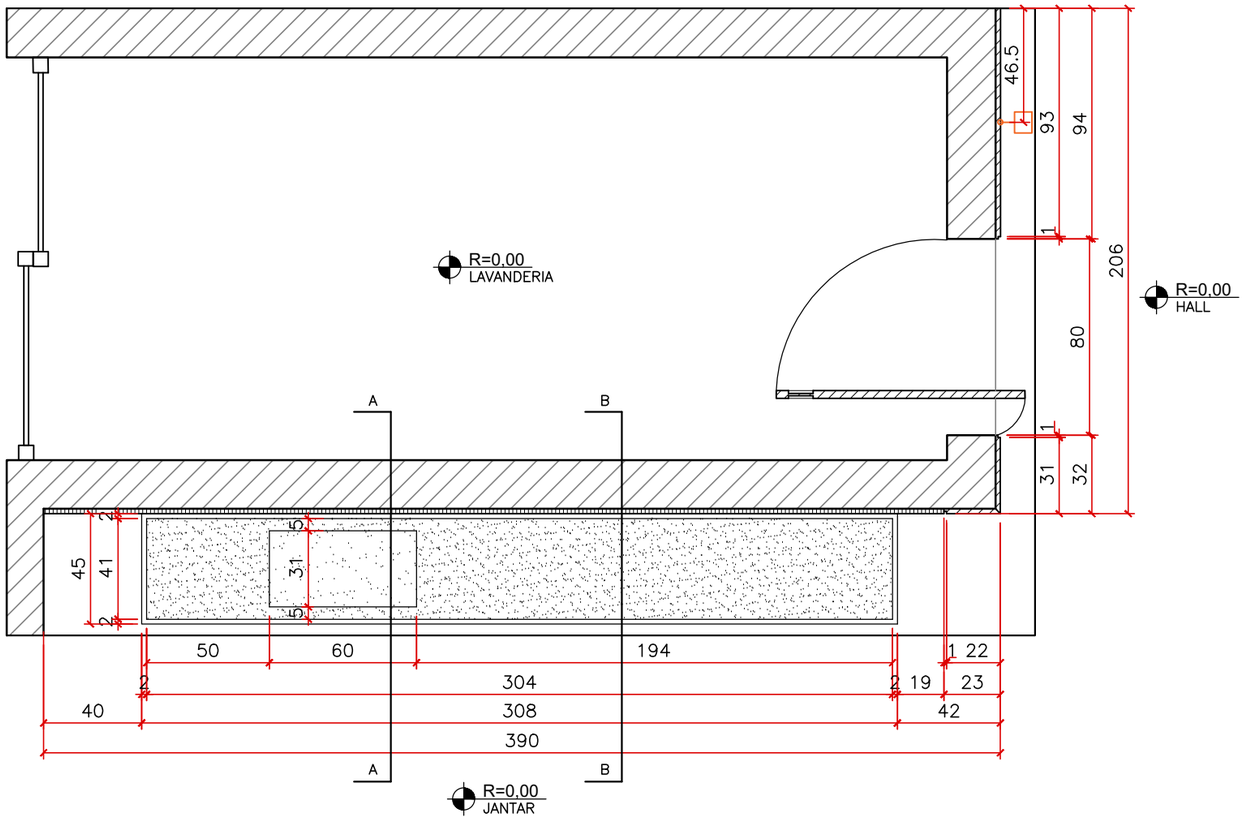



PLANTA APARADOR E PAINEL JANTAR E PAINEL HALL

ESCALA 1:25

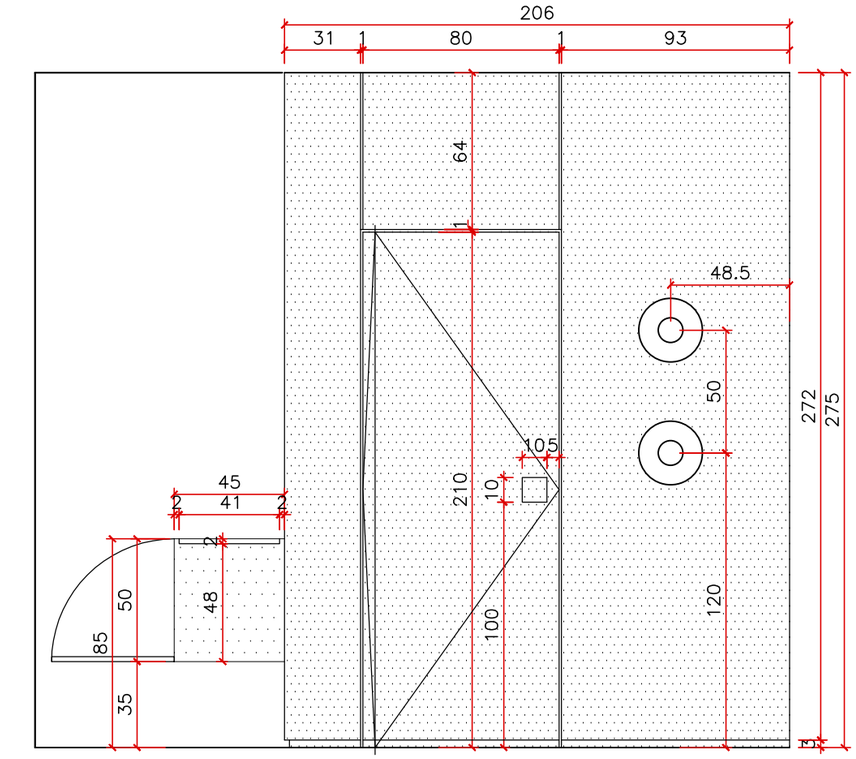


PAINEL HALL

ESCALA 1:25

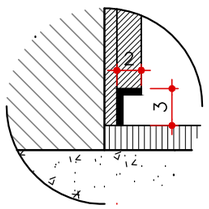


DET.CORTE RODAPÉ PAINEL

ESCALA 1:5

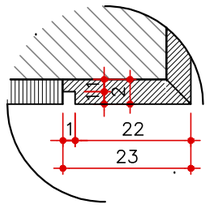

DET.PLANTA BIT PAINEL

SEM ESCALA

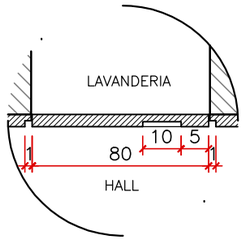

DET.PLANTA BIT LATERAL PUXADOR PORTA

SEM ESCALA

A3