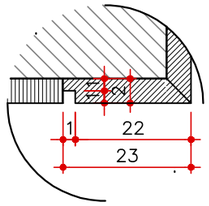


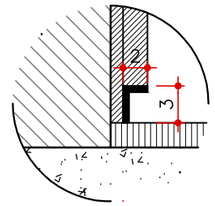

DET.PLANTA PAINEL RIPADO

ESCALA 1:5



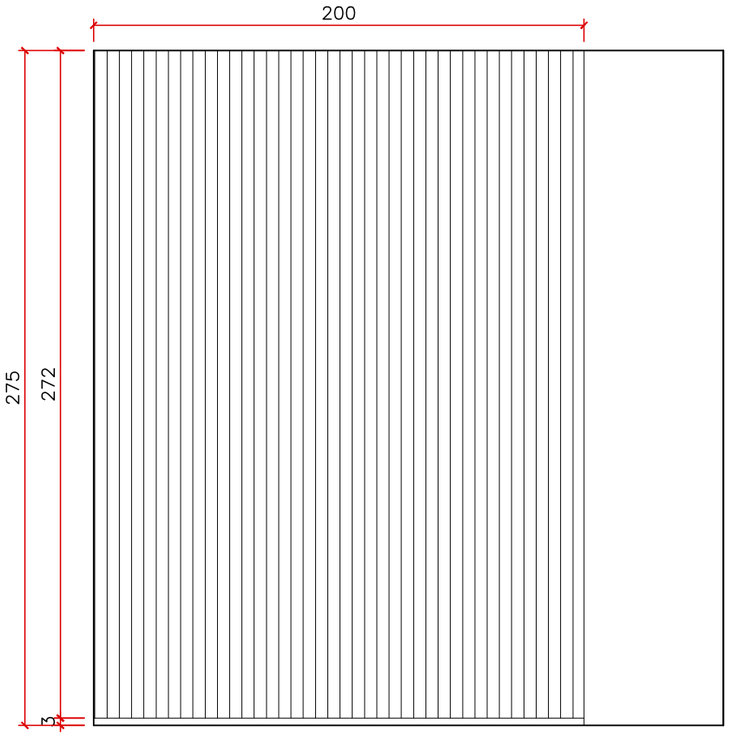

DET.PLANTA BIT PAINEL

SEM ESCALA



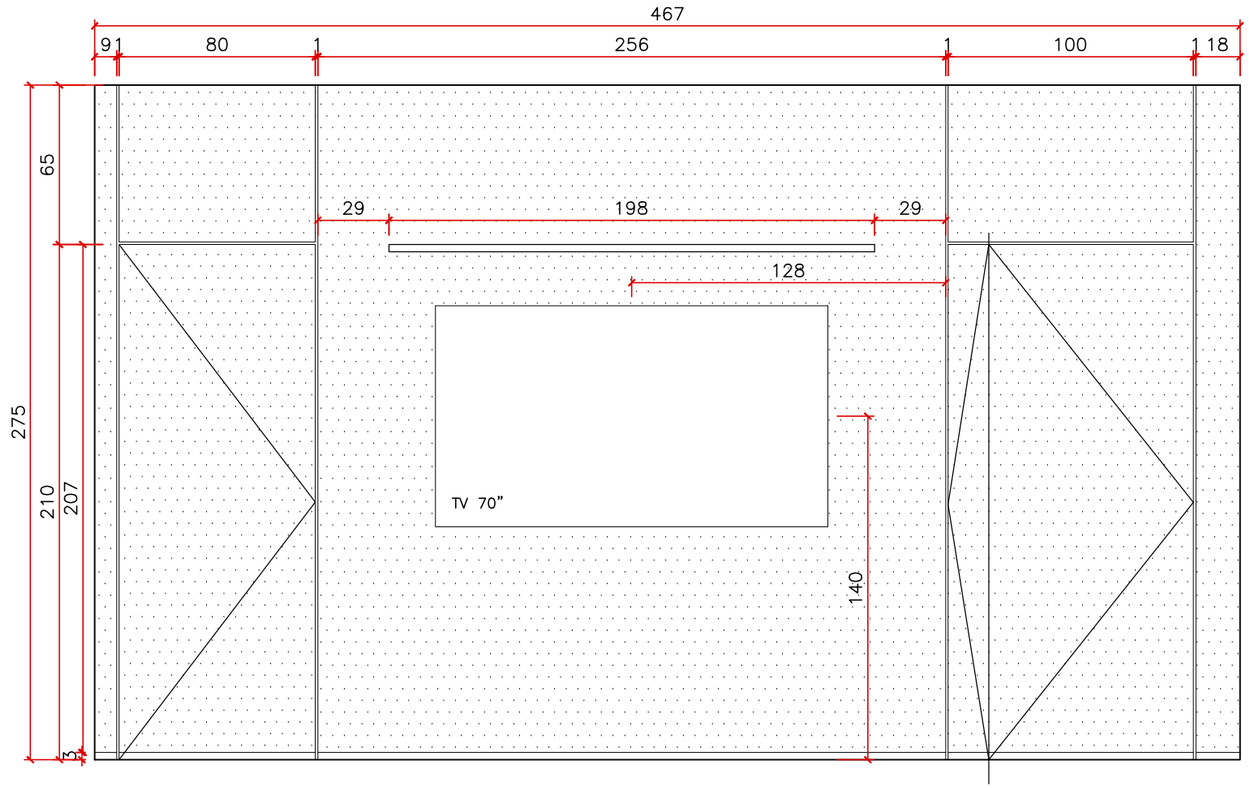

DET.CORTE RODAPÉ PAINEL

ESCALA 1:5




ELEV.01 SUÍTE MASTER

ESCALA 1:25




ELEV.02 SUÍTE MASTER

ESCALA 1:25

LEGENDA DE ACABAMENTOS:

MDF AMADEIRADO A DEFINIR

RIPADO EM MDF AMADEIRADO A DEFINIR

A3