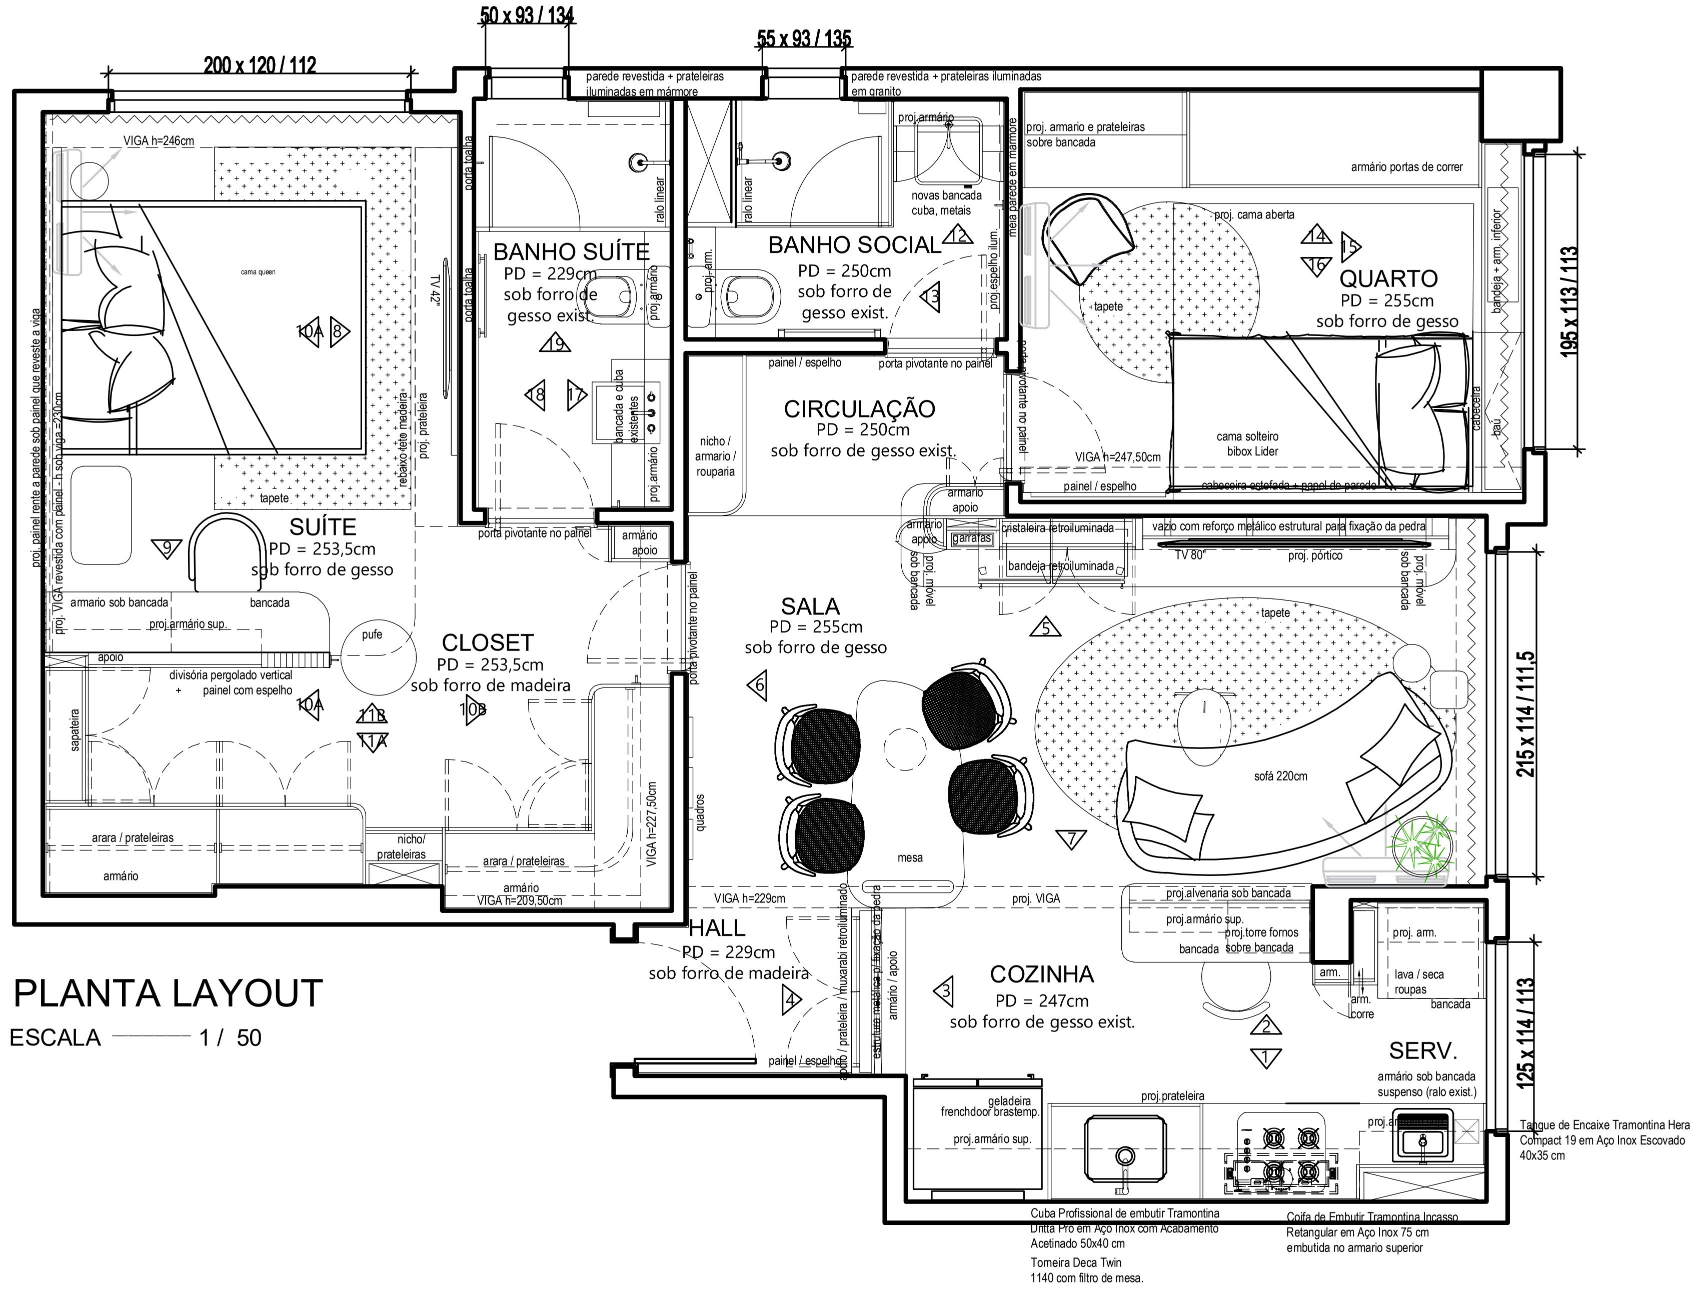
200 x 120 / 112
50 x 93 / 134
55 x 93 / 135
195 x 113 / 113
215 x 114 / 111,5
125 x 114 / 113
parede revestida + prateleiras iluminadas em mármore
parede revestida + prateleiras iluminadas em granito
VIGA h=246cm
cama queen
TV 42"
10A
8
rebaixo teto madeira
proj. prateleira
tapete
SUÍTE
PD = 253,5cm
sob forro de gesso
9
proj. painel rente a parede sob painel que reveste a viga
proj. VIGA revestida com painel - h sob viga =230cm
armario sob bancada
bancada
proj.armário sup.
apoio
pufe
divisória pergolado vertical + painel com espelho
10A
11B
11A
10B
CLOSET
PD = 253,5cm
sob forro de madeira
sapateira
arara / prateleiras
armário
nicho/ prateleiras
arara / prateleiras
armário
VIGA h=209,50cm
VIGA h=227,50cm
quadros
porta toalha
porta toalha
ralo linear
BANHO SUÍTE
PD = 229cm
sob forro de gesso exist.
proj.armário
19
18
17
bancada e cuba existentes
proj.armário
porta pivotante no painel
armário apoio
ralo linear
proj. arm.
BANHO SOCIAL
PD = 250cm
sob forro de gesso exist.
12
13
proj.armário
novas bancada cuba, metais
proj.espelho ilum.
meia parede em mármore
painel / espelho
porta pivotante no painel
CIRCULAÇÃO
PD = 250cm
sob forro de gesso exist.
nicho / armario / roupparia
porta pivotante no painel
proj. armario e prateleiras sobre bancada
armário portas de correr
proj. cama aberta
tapete
14
15
16
QUARTO
PD = 255cm
sob forro de gesso
bandeja + arm. inferior
cabeceira
baú
cama solteiro bibox Lider
VIGA h=247,50cm
painel / espelho
cabeceira estofada + papel de parede
armario apoio
armário apoio
garrafas
cristaleira retroiluminada
bandeja retroiluminada
proj. móvel sob bancada
vazio com reforço metálico estrutural para fixação da pedra
TV 80"
proj. pórtico
proj. móvel sob bancada
SALA
PD = 255cm
sob forro de gesso
porta pivotante no painel
5
6
tapete
sofá 220cm
mesa
7
VIGA h=229cm
proj. VIGA
HALL
PD = 229cm
sob forro de madeira
4
apoio / prateleira / muxarabi retroiluminado
estrutura metálica p/ fixação da pedra
armário / apoio
painel / espelho
proj.alvenaria sob bancada
proj.armário sup.
proj.torre fornos sobre bancada
bancada
COZINHA
PD = 247cm
sob forro de gesso exist.
3
2
1
arm.
arm. corre
proj. arm.
lava / seca roupas
bancada
SERV.
armário sob bancada suspenso (ralo exist.)
geladeira frenchdoor brastemp.
proj.armário sup.
proj.prateleira
proj.armário sup.
Tanque de Encaixe Tramontina Hera Compact 19 em Aço Inox Escovado 40x35 cm
Cuba Profissional de embutir Tramontina Dritta Pro em Aço Inox com Acabamento Acetinado 50x40 cm
Tomeira Deca Twin 1140 com filtro de mesa.
Coifa de Embutir Tramontina Incasso Retangular em Aço Inox 75 cm embutida no armario superior

PLANTA LAYOUT

ESCALA ——— 1 / 50

OBS.:- ALGUMAS MEDIDAS ESTÃO COM VALORES APROXIMADOS.	REVISÃO	DATA	MODIFICAÇÕES	CLIENTE	FORMATO	DATA
- TODAS AS MEDIDAS DEVERÃO SER CONFERIDAS NO LOCAL.	3	05/08	Apresentação Anteprojeto - subetapa 1/3	CHARBEL CHELALA	A3	OUT/2026
- EM CASO DE DÚVIDAS, CONSULTAR A PROFISSIONAL.	2	26/08	Apresentação Anteprojeto - subetapa 2/3	CONTEÚDO	ESCALA	FOLHA
- AS MEDIDAS ESTÃO EM CENTÍMETROS.	1	16/10	Entrega projeto executivo	LAYOUT	1/50	02

MARIANA BORGES - ARQUITETURA & INTERIORES
BELO HORIZONTE - NOVA LIMA - BRASIL - (31) 98789.4636 - ● @marianaborges_arquiteta

"As ideias constantes do projeto, sua concepção e detalhamento constituem patrimônio da profissional como direito autoral e somente poderão ser divulgadas com a sua autorização."