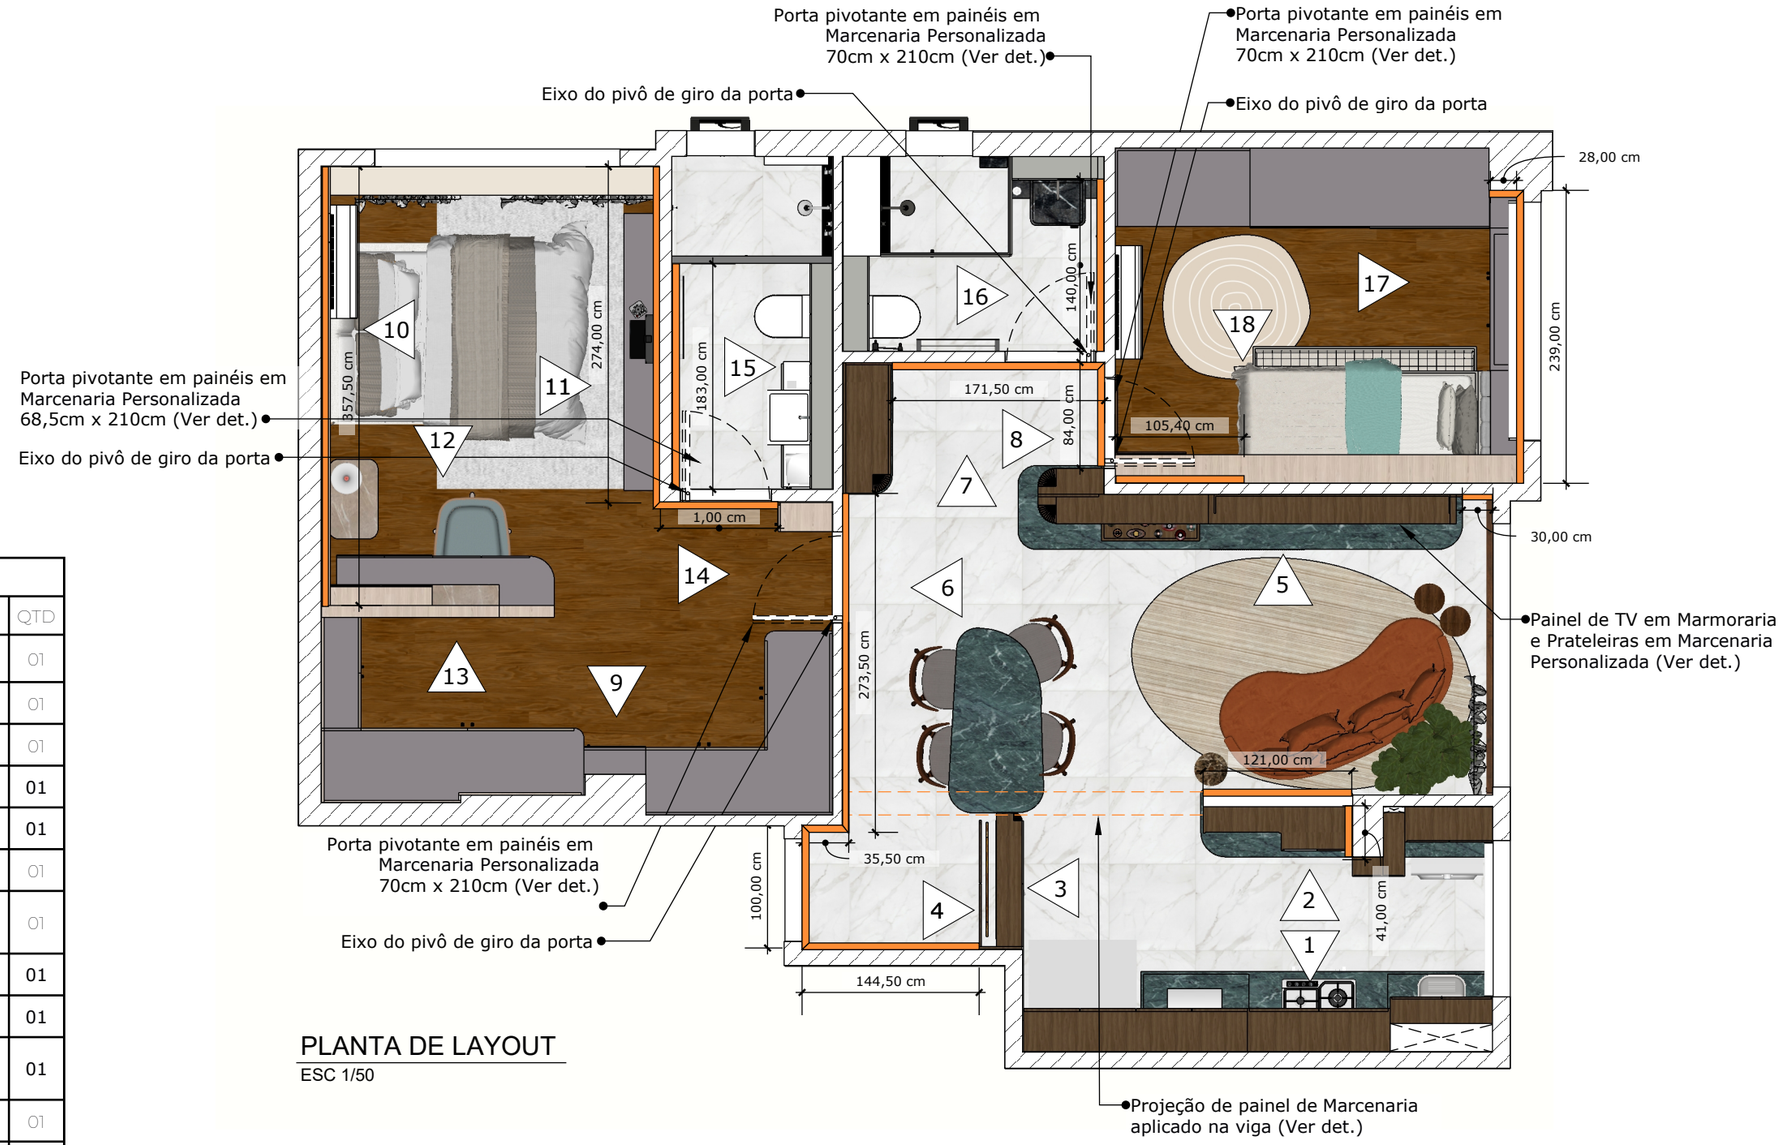


PLANTA DE LAYOUT

ESC 1/50

LEGENDA:

Painéis em MDF fixados na parede. (ver det.)

LISTA DE OBJETOS		
LETRA	DESCRIÇÃO	QTD
A	Marmoraria Personalizada: Bancada em Mármore Verde Guatemala (Ver det.)	01
B	Armários superiores e inferiores em marcenaria personalizada: (Ver det.)	01
C	Marmoraria Personalizada:Bancada em Mármore Verde Guatemala (Ver det.)	01
D	Marcenaria Personalizada: (Ver det.)	01
E	Marmoraria Personalizada:Bancada em Mármore Verde Guatemala (Ver det.)	01
F	Marcenaria Personalizada: (Ver det.)	01
G	Marmoraria Personalizada: Painel em Mármore Onix (Ver det.)	01
H	Marcenaria Personalizada: (Ver det.)	01
I	Marmoraria Personalizada: Mesa em Mármore Verde Guatemala (Ver det.)	01
J	Marmoraria Personalizada:Bancada em Mármore Verde Guatemala (Ver det.)	01
K	Marcenaria Personalizada: (Ver det.)	01
L	Marmoraria Personalizada:Bancada em Mármore Verde Guatemala (Ver det.)	01
M	Marcenaria Personalizada: (Ver det.)	01
N	Marmoraria Personalizada: Bancada em Mármore Griogio Carnio (Ver det.)	01
O	Marcenaria Personalizada: (Ver det.)	01
P	Marcenaria Personalizada: (Ver det.)	01
Q	Marcenaria Personalizada: (Ver det.)	01

OBSERVAÇÕES IMPORTANTES

-ALGUMAS MEDIDAS ESTÃO COM VALORES APROXIMADOS.

-TODAS AS MEDIDAS DEVERÃO SER CONFERIDAS NO LOCAL.

-TODAS AS MEDIDAS ESTÃO EM CENTÍMETROS.

-EM CASO DE DÚVIDAS, CONSULTAR AS PROFISSIONAIS.

REVISÃO	DATA	ANDAMENTO
1	05/08	APRESENTAÇÃO ANTEPROJETO - 1/3
2	26/08	APRESENTAÇÃO ANTEPROJETO - 2/3
3	16/10	ENTREGA PROJETO EXECUTIVO

CLIENTE
CHARBEL

FORMATO
A3

DATA
OUT/2026

CONTEÚDO
PLANTA DE LAYOUT

ESCALA
1/50

FOLHA
12

MARIANA BORGES - ARQUITETURA & INTERIORES
BELO HORIZONTE - NOVA LIMA - BRASIL - (31) 98789-4636 - @marianaborges_arquiteta

"As ideias constantes do projeto, sua concepção e detalhamento constituem patrimônio da profissional como direito autoral, e somente poderão ser divulgados com a sua autorização."

LISTA DE MARMORARIA		
LETRA	DESCRIÇÃO	QTD
A	Bancada em Marmoraria Personalizada Verde Guatemala com cubas embutidas (Ver det.)	01
B	Bancada de apoio em Marmoraria Personalizada Verde Guatemala (Ver det.)	01
C	Bancada de lanche em Marmoraria Personalizada Verde Guatemala (Ver det.)	01
D	Painel Retroiluminado em Marmoraria Personalizada Onix (Ver det.)	01
E	Tampo de Mesa Orgânica em Marmoraria Personalizada Verde Guatemala (Ver det.)	01
F	Painel de Tv + Aparador em Marmoraria Personalizada Verde Guatemala (Ver det.)	01
G	Nicho em Marmoraria Personalizada Verde Guatemala (Ver det.)	01
H	Bancada com Cuba Esculpida em Mármore Grigio Carnico + Prateleiras (Ver det.)	01



PLANTA DE MARMORARIA

ESC 1/50

OBSERVAÇÕES IMPORTANTES

-ALGUMAS MEDIDAS ESTÃO COM VALORES APROXIMADOS.

-TODAS AS MEDIDAS DEVERÃO SER CONFERIDAS NO LOCAL.

-TODAS AS MEDIDAS ESTÃO EM CENTÍMETROS.

-EM CASO DE DÚVIDAS, CONSULTAR AS PROFISSIONAIS.

REVISÃO	DATA	ANDAMENTO
3	05/08	APRESENTAÇÃO ANTEPROJETO - 1/3
2	26/08	APRESENTAÇÃO ANTEPROJETO - 2/3
3	16/10	ENTREGA PROJETO EXECUTIVO

CLIENTE
CHARBEL

FORMATO
A3

DATA
OUT/2026

CONTEÚDO
PLANTA DE MARMORARIA

ESCALA
1/50

FOLHA
13


MARIANA BORGES - ARQUITETURA & INTERIORES
BELO HORIZONTE - NOVA LIMA - BRASIL - (31) 98789-4636 - @marianaborges_arquiteta

"As ideias constantes do projeto, sua concepção e detalhamento constituem patrimônio da profissional como direito autoral, e somente poderão ser divulgados com a sua autorização."

LEGENDA:

Painéis em MDF fixados na parede. (ver det.)

LISTA DE MARCENARIA		
LETRA	DESCRIÇÃO	QTD
A	Bancada em Marmoraria Personalizada Verde Guatemala com cubas embutidas (Ver det.)	01
B	Bancada de apoio em Marmoraria Personalizada Verde Guatemala (Ver det.)	01
C	Bancada de lanche em Marmoraria Personalizada Verde Guatemala (Ver det.)	01
D	Painel Retroiluminado em Marmoraria Personalizada Onix (Ver det.)	01
E	Tampo de Mesa Orgânica em Marmoraria Personalizada Verde Guatemala (Ver det.)	01
F	Painel de Tv + Aparador em Marmoraria Personalizada Verde Guatemala (Ver det.)	01
G	Nicho em Marmoraria Personalizada Verde Guatemala (Ver det.)	01
H	Bancada com Cuba Esculpida em Mármore Grigio Carnico + Prateleiras (Ver det.)	01

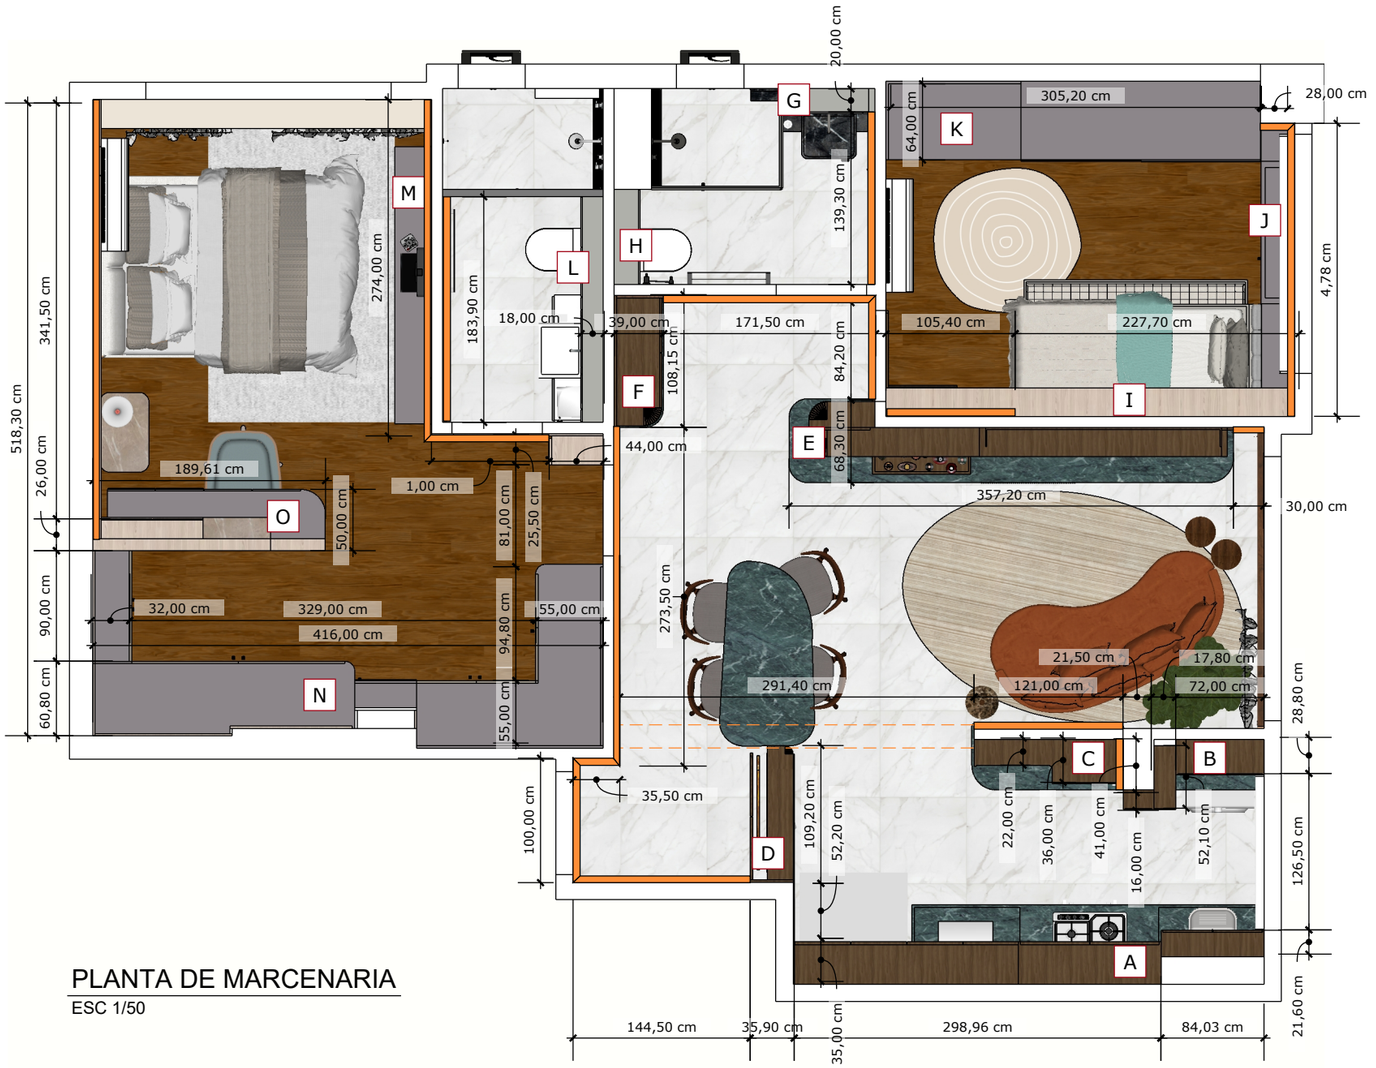

PLANTA DE MARCENARIA

ESC 1/50

OBSERVAÇÕES IMPORTANTES	
	-ALGUMAS MEDIDAS ESTÃO COM VALORES APROXIMADOS.
	-TODAS AS MEDIDAS DEVERÃO SER CONFERIDAS NO LOCAL.
	-TODAS AS MEDIDAS ESTÃO EM CENTÍMETROS.
	-EM CASO DE DÚVIDAS, CONSULTAR AS PROFISSIONAIS.

REVISÃO	DATA	ANDAMENTO
1	05/08	APRESENTAÇÃO ANTEPROJETO - 1/3
2	26/08	APRESENTAÇÃO ANTEPROJETO - 2/3
3	16/10	ENTREGA PROJETO EXECUTIVO

CLIENTE
CHARBEL

CONTEÚDO
PLANTA DE MARCENARIA

FORMATO	DATA
A3	OUT/2026
ESCALA	**FOLHA**
1/50	14

MARIANA BORGES - ARQUITETURA & INTERIORES
BELO HORIZONTE - NOVA LIMA - BRASIL - (31) 98789-4636 - @marianaborges_arquiteta

"As ideias constantes do projeto, sua concepção e detalhamento constituem patrimônio da profissional como direito autoral, e somente poderão ser divulgados com a sua autorização."