
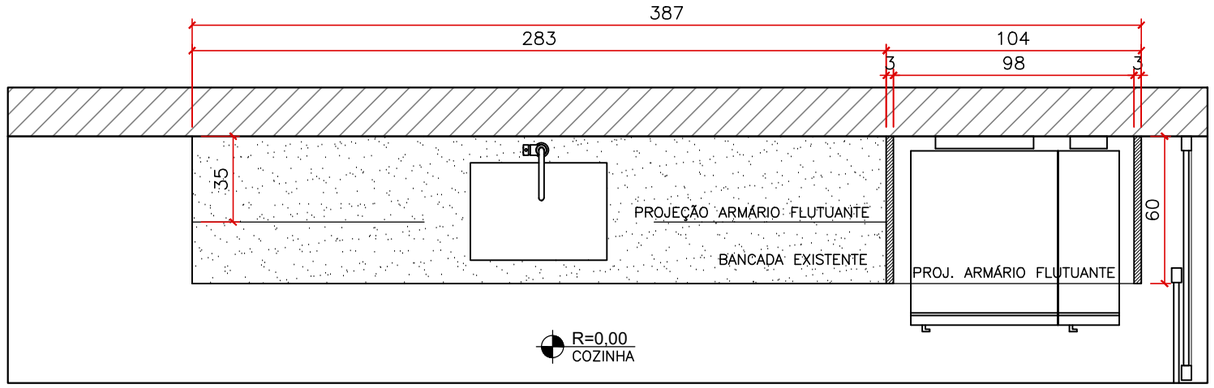



PLANTA ARMÁRIOS COMPLEMENTARES COZINHA

ESCALA 1:25

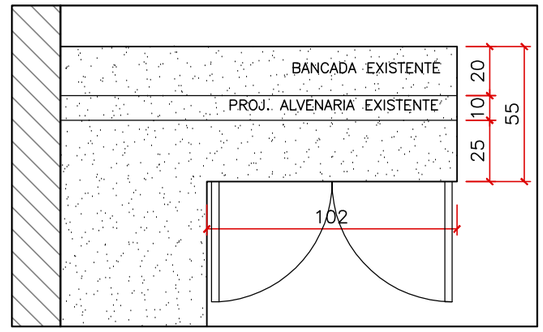


PLANTA ARMÁRIO COMPLEMENTAR GOURMET

ESCALA 1:25

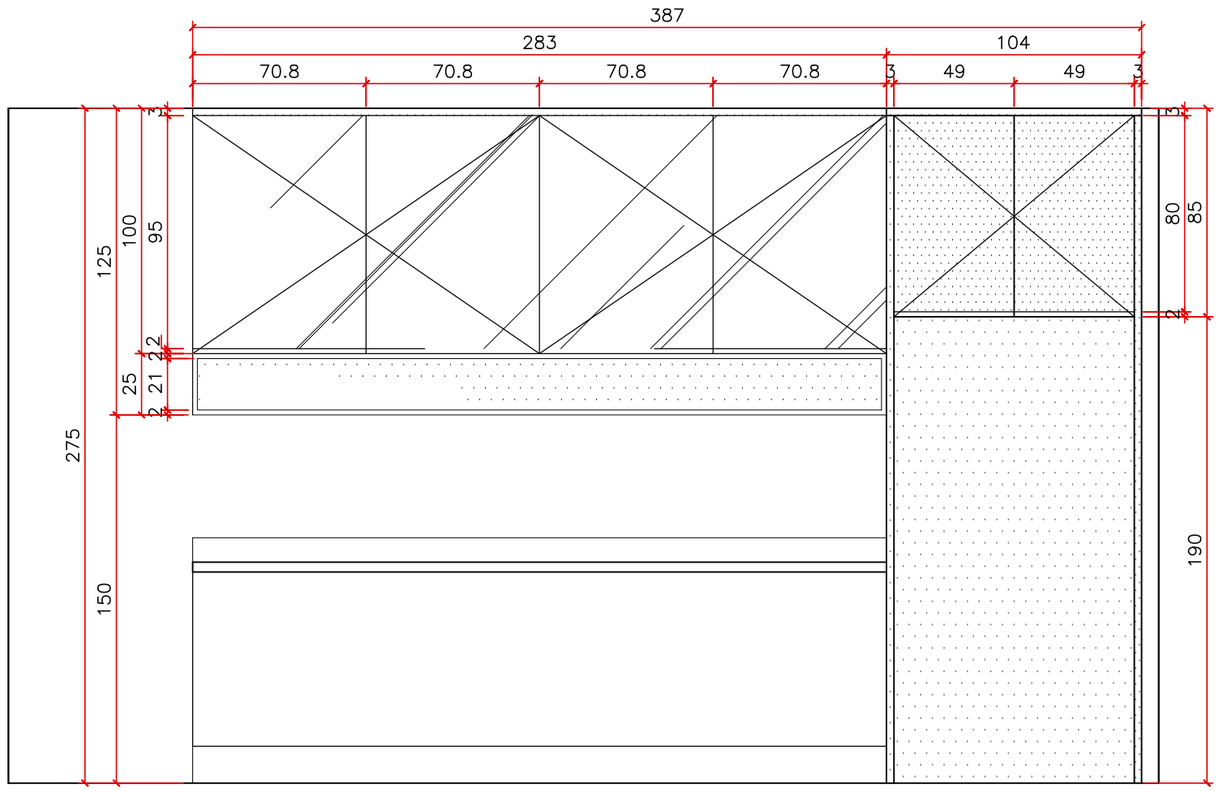

ELEVAÇÃO ARMÁRIOS COMPLEMENTARES COZINHA

ESCALA 1:25

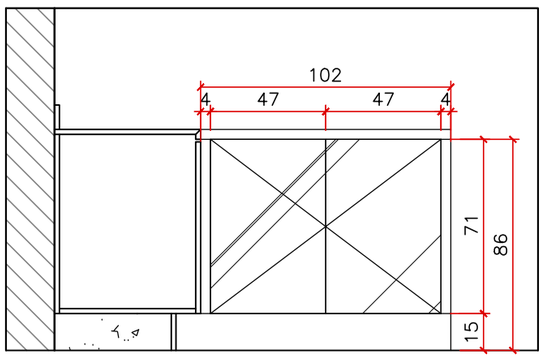

ELEV. ARMÁRIO COMPLEMENTAR GOURMET

ESCALA 1:25

LEGENDA DE ACABAMENTOS:

MDF AMADEIRADO A DEFINIR	RIPADO EM MDF AMADEIRADO A DEFINIR
TRAVERTINO ROMANO ESCOVADO	VIDRO REFLECTA CRISTAL

A3