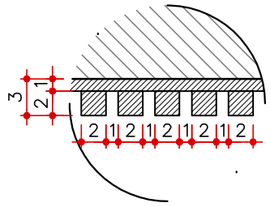

DET.PLANTA PAINEL RIPADO

ESCALA 1:5

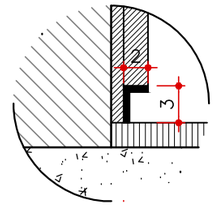

DET.CORTE RODAPÉ PAINEL

ESCALA 1:5

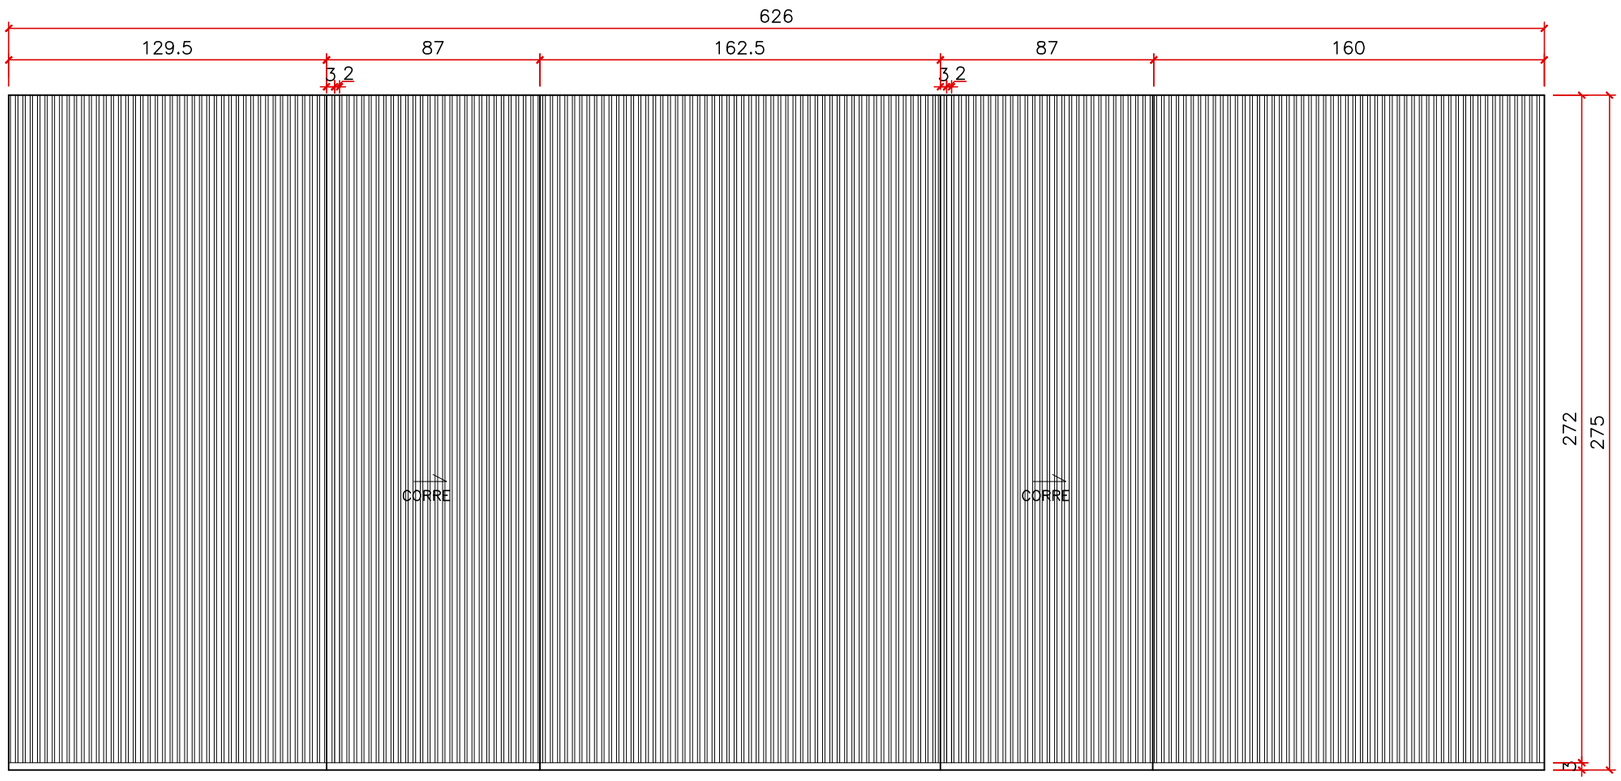

ELEVAÇÃO PAINEL RIPADO

ESCALA 1:25

A3