
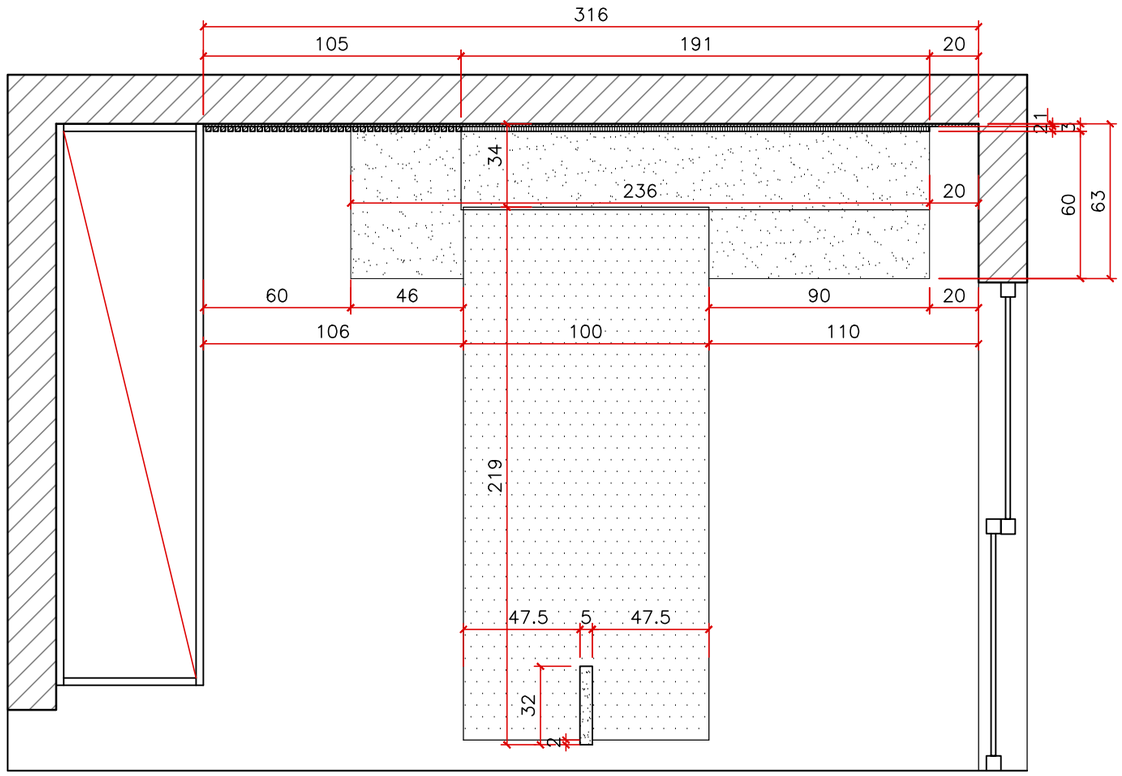



PLANTA ESCRITÓRIO

ESCALA 1:25

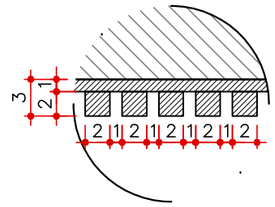

DET.PLANTA PAINEL RIPADO

ESCALA 1:5

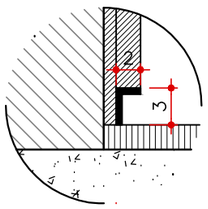

DET.CORTE RODAPÉ PAINEL

ESCALA 1:5

LEGENDA DE ACABAMENTOS:	
MDF AMADEIRADO A DEFINIR	RIPADO EM MDF AMADEIRADO A DEFINIR
TRAVERTINO ROMANO ESCOVADO	VIDRO REFLECTA CRISTAL

A3