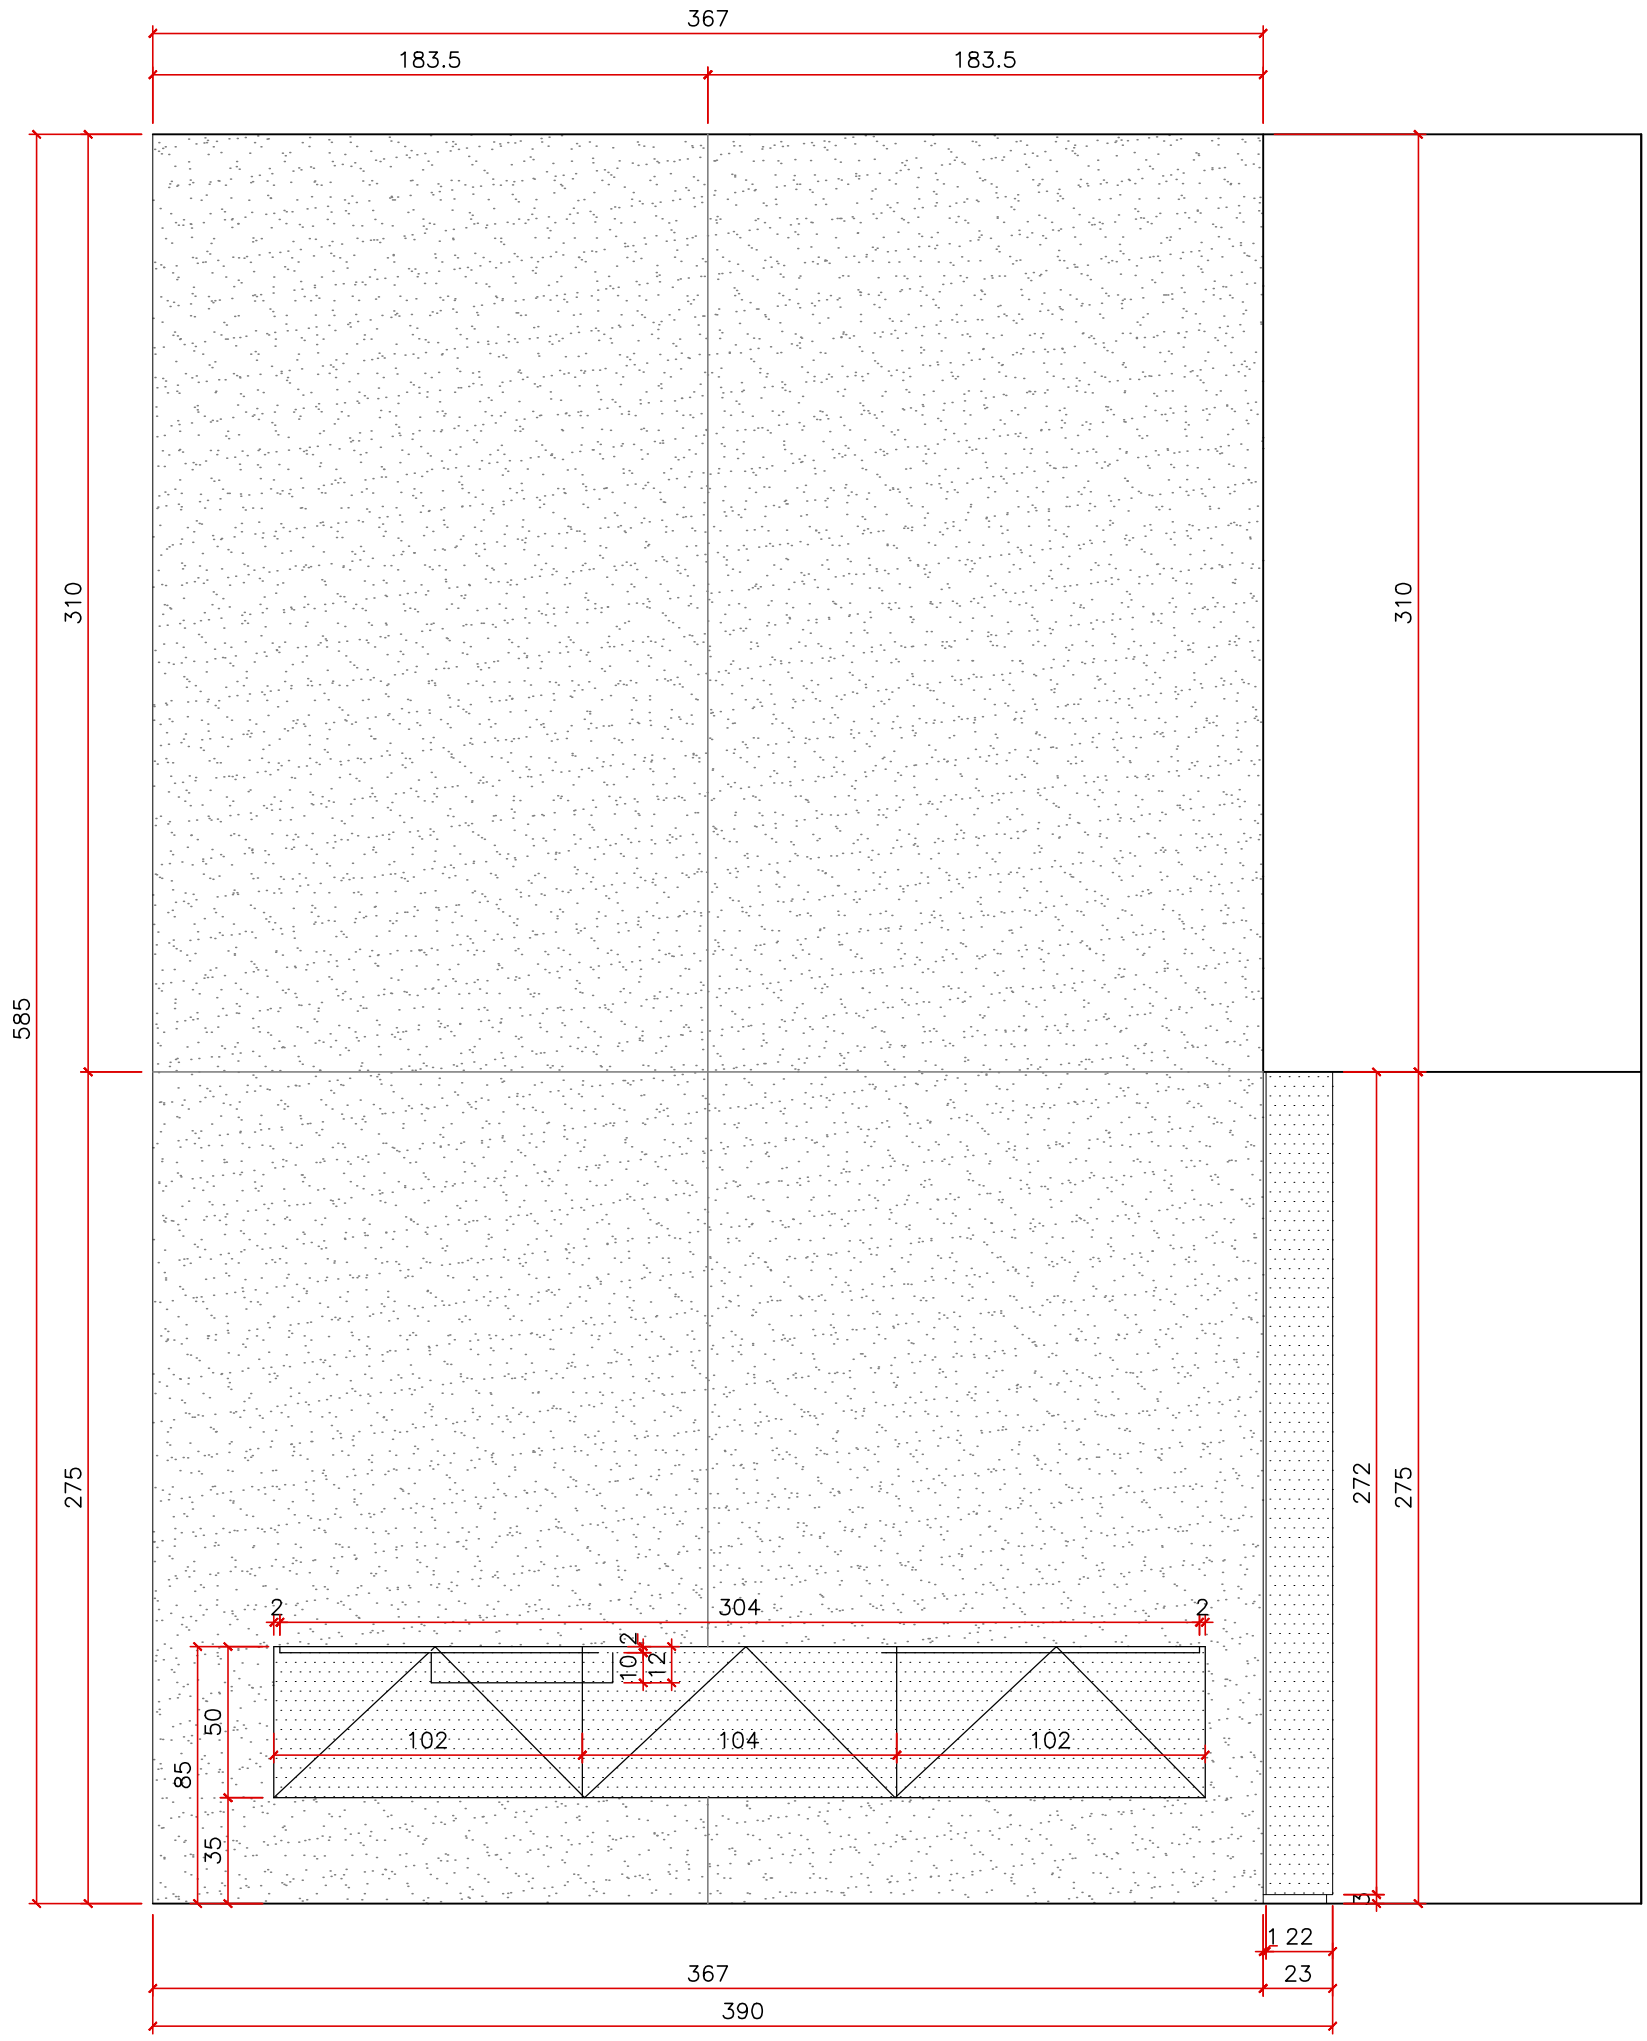


ELEVAÇÃO APARADOR E PAINEL JANTAR

ESCALA 1:25

LEGENDA DE ACABAMENTOS:	
MDF AMADEIRADO A DEFINIR	RIPADO EM MDF AMADEIRADO A DEFINIR
TRAVERTINO ROMANO ESCOVADO	VIDRO REFLECTA CRISTAL

A3