


PLANTA PAINEL E RACK SALA DE TELEVISÃO

ESCALA 1:25

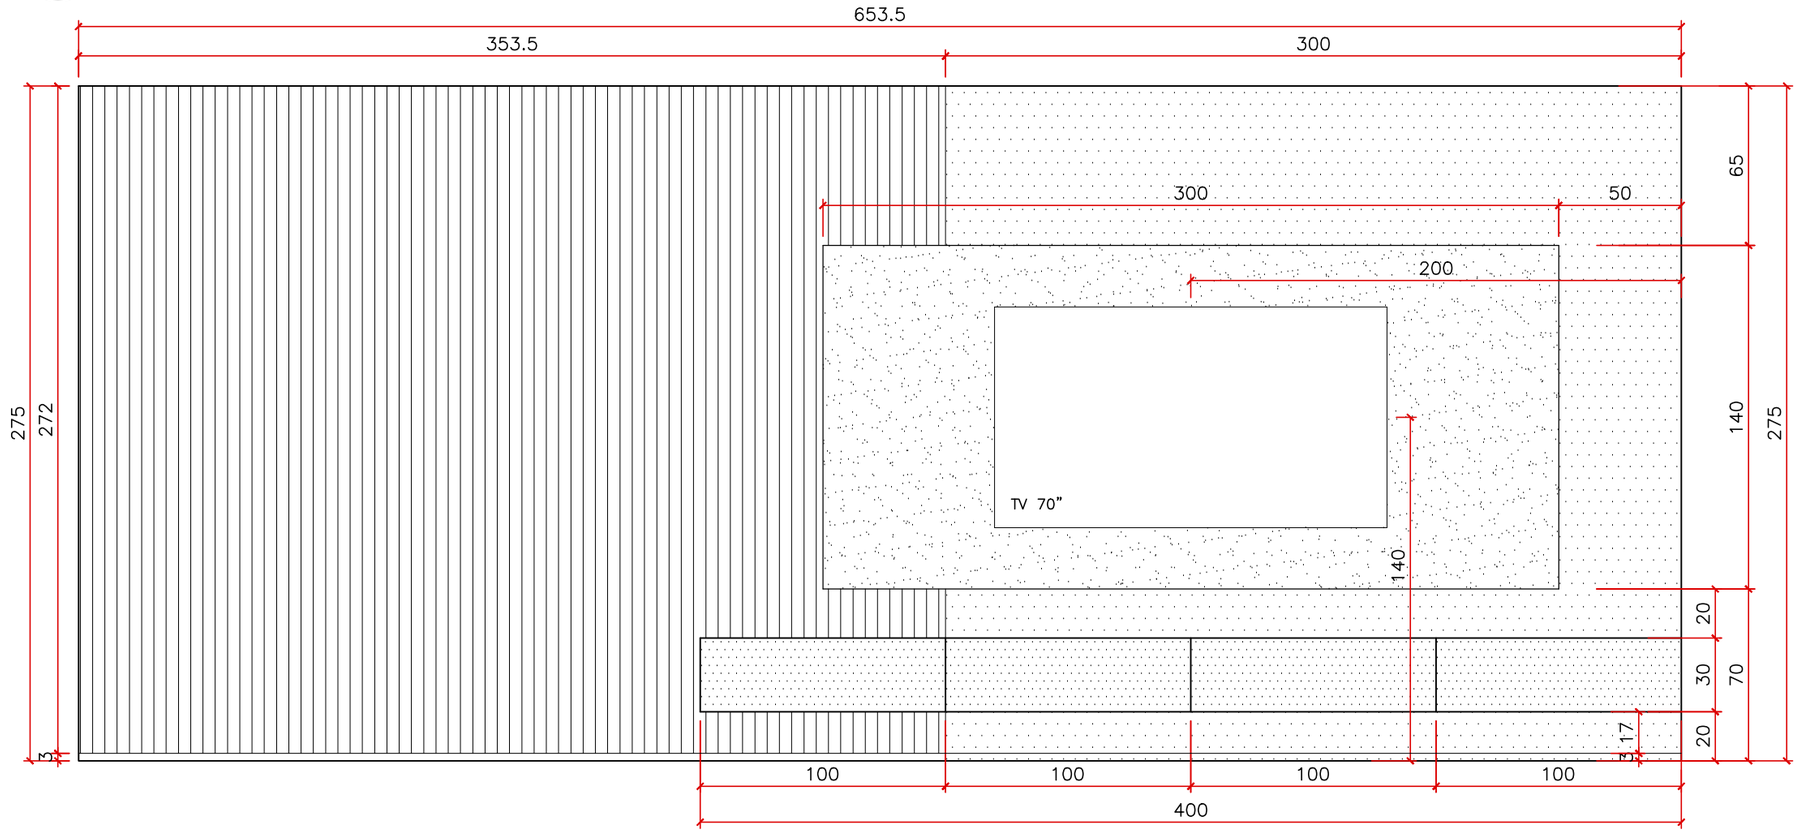


ELEV. PAINEL E RACK SALA DE TELEVISÃO

ESCALA 1:25


LEGENDA DE ACABAMENTOS:

MDF AMADEIRADO A DEFINIR	RIPADO EM MDF AMADEIRADO A DEFINIR
TRAVERTINO ROMANO ESCOVADO	VIDRO REFLECTA CRISTAL

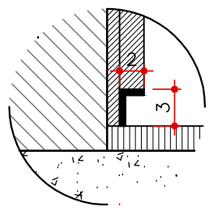

DET.CORTE RODAPÉ PAINEL

ESCALA 1:5

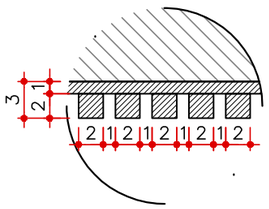

DET.PLANTA PAINEL RIPADO

ESCALA 1:5

A3