




ANEXO - HOMESCHOOLING
ELEVAÇÃO A
Esc.: 1/25

Tomada Dupla

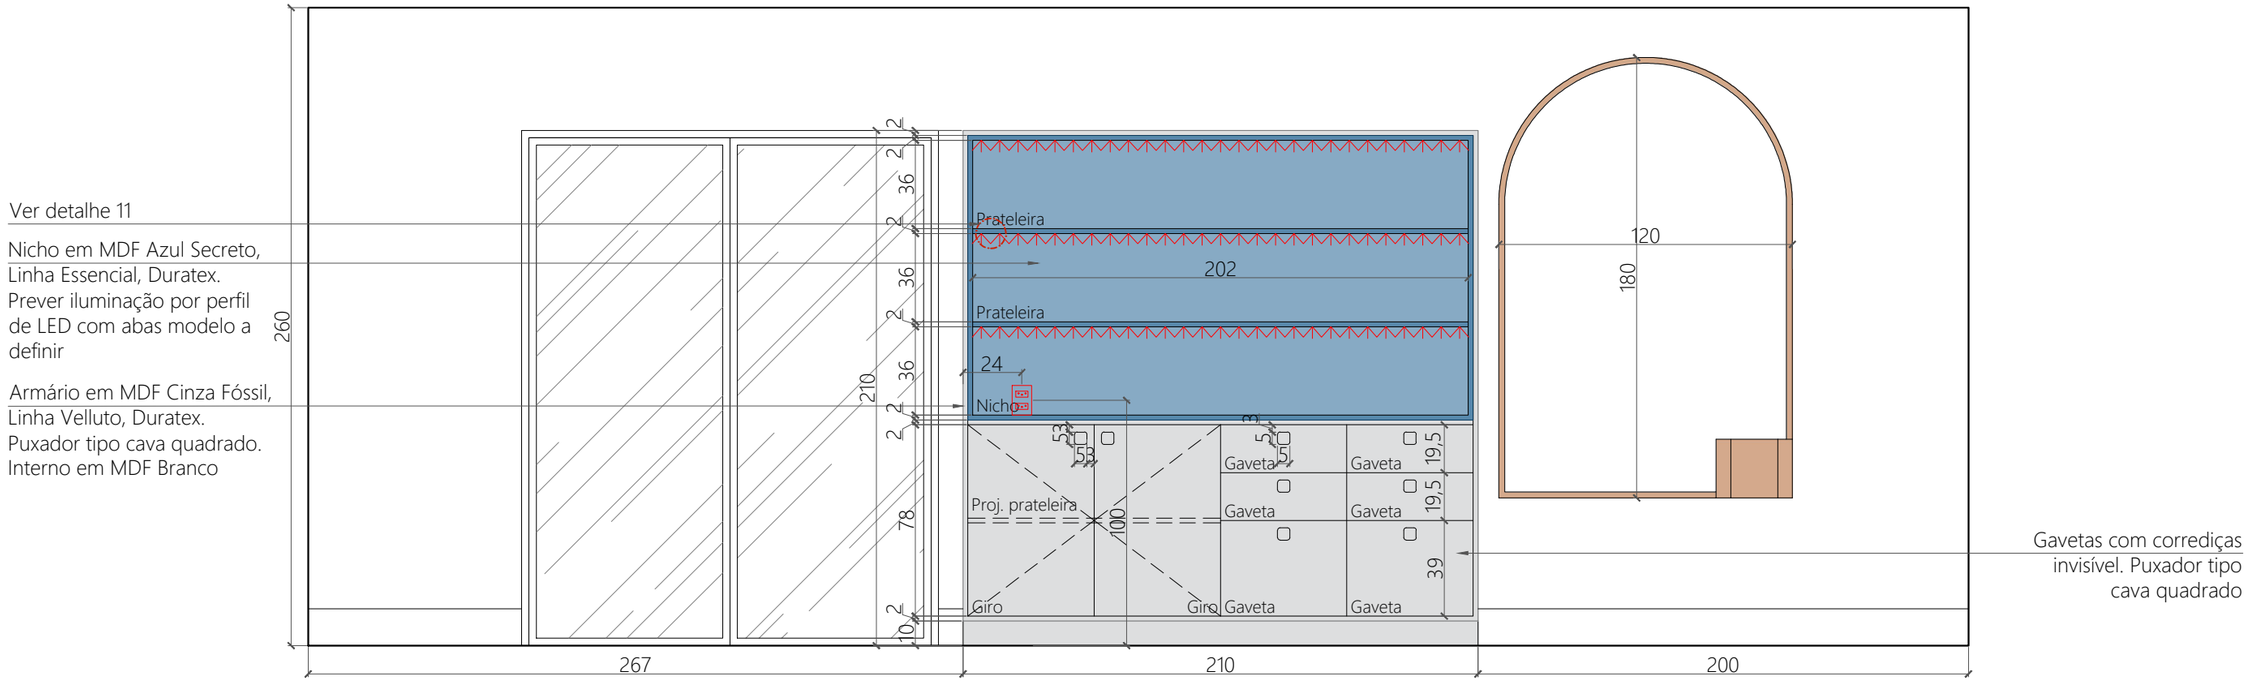

DETALHE 11
PERFIL DE LED EMBUTIDO
Esc.: 1/5

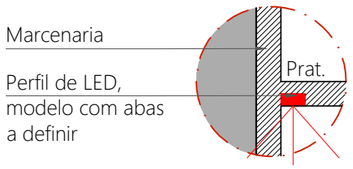

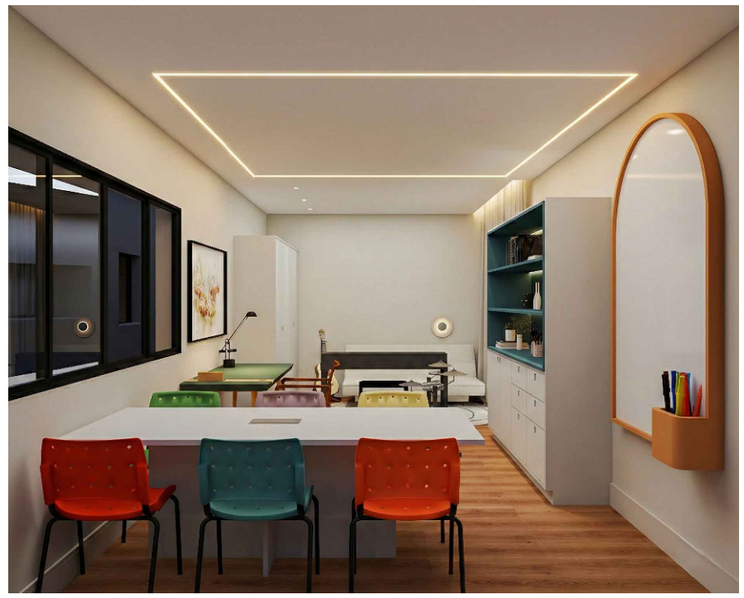

LUIZA PACHECO ARQUITETURA
Luiza Pacheco
CAU: A69992-6
(31) 98885-1403
luiza@luizapacheco.com.br
www.luizapacheco.com.br

Todas as medidas devem ser conferidas no local antes da execução;
Cotas em centímetros (salvo onde há informação de uso de outras medidas);
Todos os direitos autorais reservados ao escritório;
Em caso de dúvidas ou necessidade de alterações durante a execução, contatar o escritório de arquitetura.

CLIENTE: Gustavo Raposo
ENDEREÇO: Condomínio Vale dos Pinhais, Nova Lima, MG

EXECUTIVO
ANEXO HOMESCHOOLING - ELEVAÇÃO

Revisão: 00
Março, 2026

Formato: A3