

IONAH | PINHO
arquitetura & interiores

KARINA RAMOS
PROJETO INTERIORES - ESCRITÓRIO

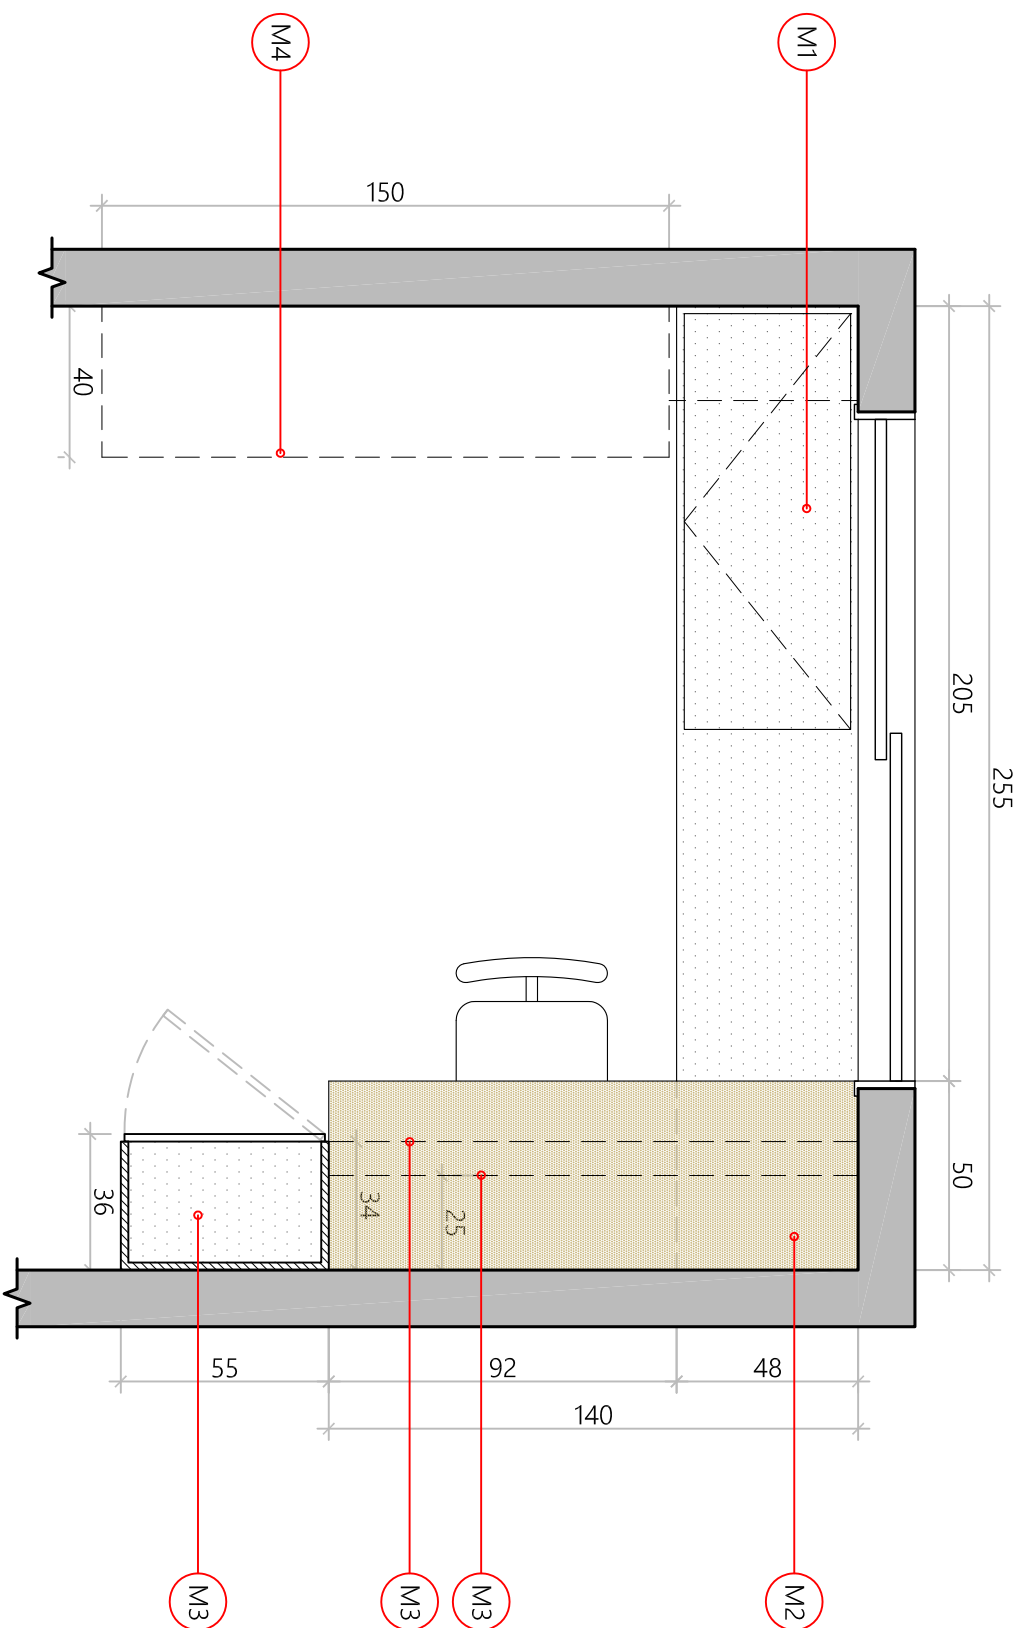

PLANTA GERAL
ESC. 1/20





arquitetura & interiores
31 99113-9502
ionahpinho.arquitetura@gmail.com

OBSERVAÇÕES:
- TODAS AS MEDIDAS DO ESPAÇO, DO MOBILIÁRIO E DOS EQUIPAMENTOS EXISTENTES DEVEM SER CONFERIDAS NO LOCAL, ANTES DA PRODUÇÃO OU FABRICAÇÃO DO CONTEÚDO DESTES PROJETOS.

Projeto:	Cliente:
ESCRITÓRIO	KARIAN RAMOS
Conteúdo:	Endereço:
MARcenARIA	RUA SERGIPE, 440, AP:101 FUNCIONARIOS, BH/MG
Folha: 01	Aprovado: 0
	Revisão: 0
	Data: JUN/2026






- TRANSFERIR A TOMADA DE ENERGIA EXISTENTE ATRÁS DO APARADOR PARA O TAMPO SUPERIOR COM TAMPA ARTICULADA;

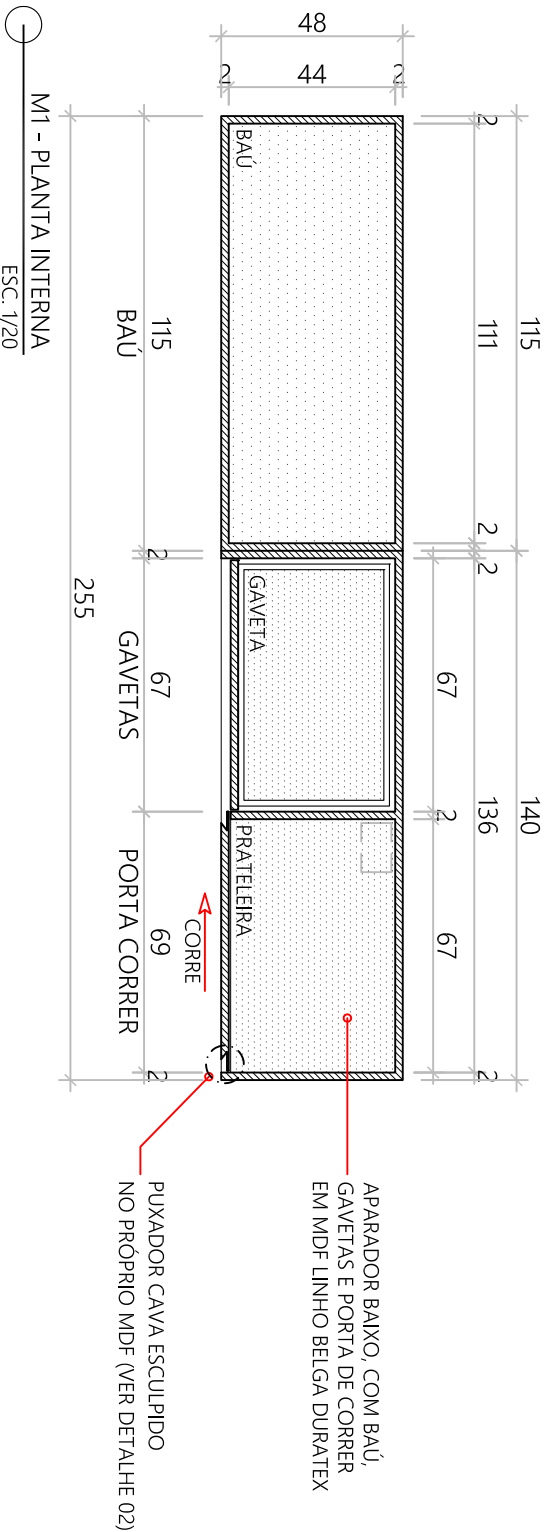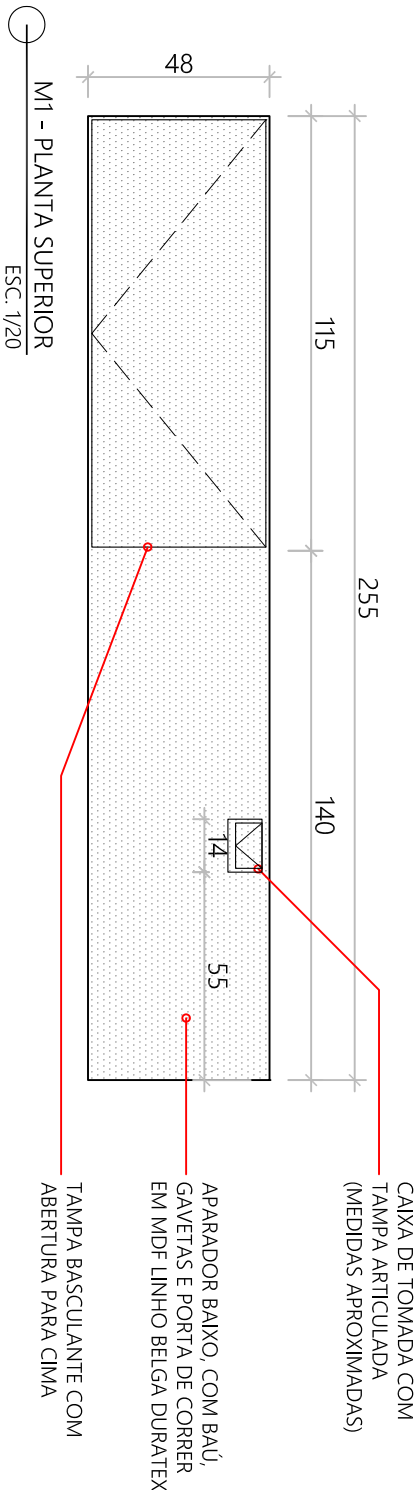

OBSERVAÇÕES:
- TODAS AS MEDIDAS DO ESPAÇO, DO MOBILIÁRIO E DOS EQUIPAMENTOS EXISTENTES DEVEM SER CONFERIDAS NO LOCAL, ANTES DA PRODUÇÃO OU FABRICAÇÃO DO CONTEÚDO DESTES PROJETO.

arquitetura & interiores
31 99113-9502 CAU: 29.315-6
ionahpinho.arquitetura@gmail.com

Cliente: KARIAN RAMOS		Projeto: ESCRITÓRIO	
Endereço: RUA SERGIPE, 440, AP.101 FUNCIONÁRIOS, BH/MG		Conteúdo: MARCENARIA	
Aprovado:	Revisão: 0	Data: JUN/2026	Folha: 02

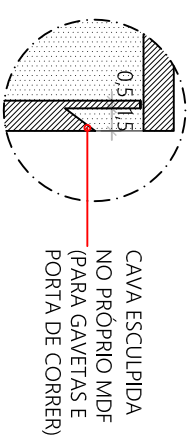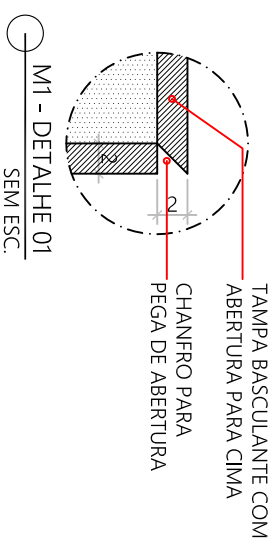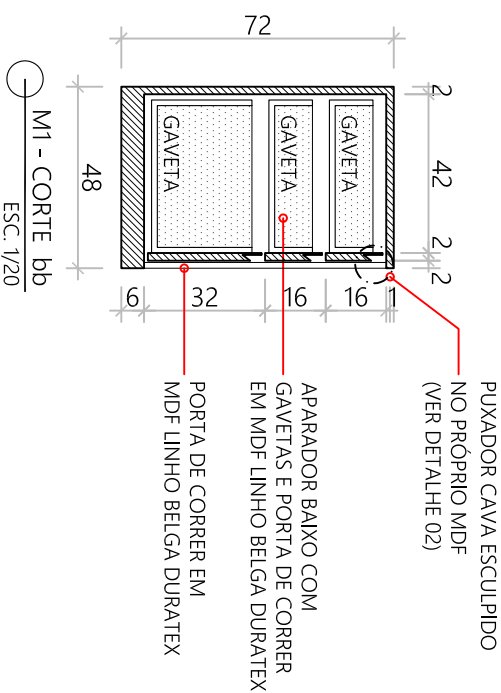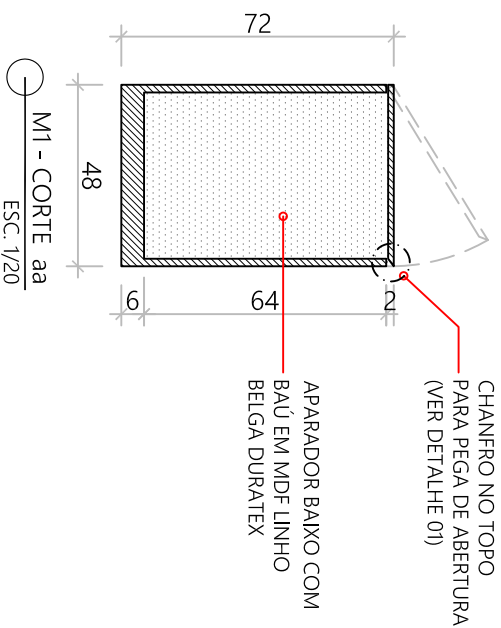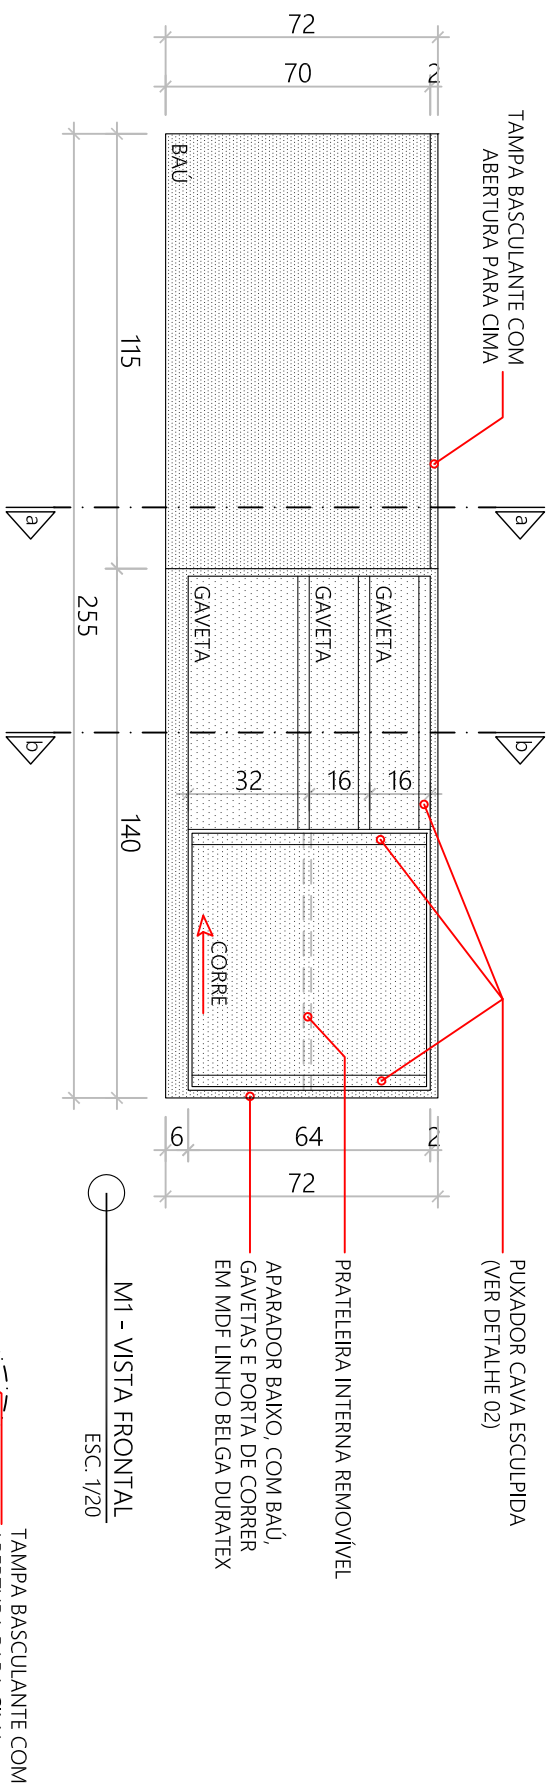

IONAH PINHO

arquitetura & interiores
31 99113-9502 CAU: 29.315-6
ionahpinho.arquitetura@gmail.com

Cliente:
KARIAN RAMOS

Projeto:
ESCRITÓRIO

Endereço:
RUA SERGIPE, 440, AP.101
FUNCIONARIOS, BH/MG

Conteúdo:
MARCCENARIA



Aprovado:

Revisão: 0

Data: JUN/2026

Folha: 03



OBSERVAÇÕES:
- TODAS AS MEDIDAS DO ESPAÇO, DO MOBILIÁRIO E DOS EQUIPAMENTOS EXISTENTES DEVEM SER CONFERIDAS NO LOCAL, ANTES DA PRODUÇÃO OU FABRICAÇÃO DO CONTEÚDO DESTES PROJETO.

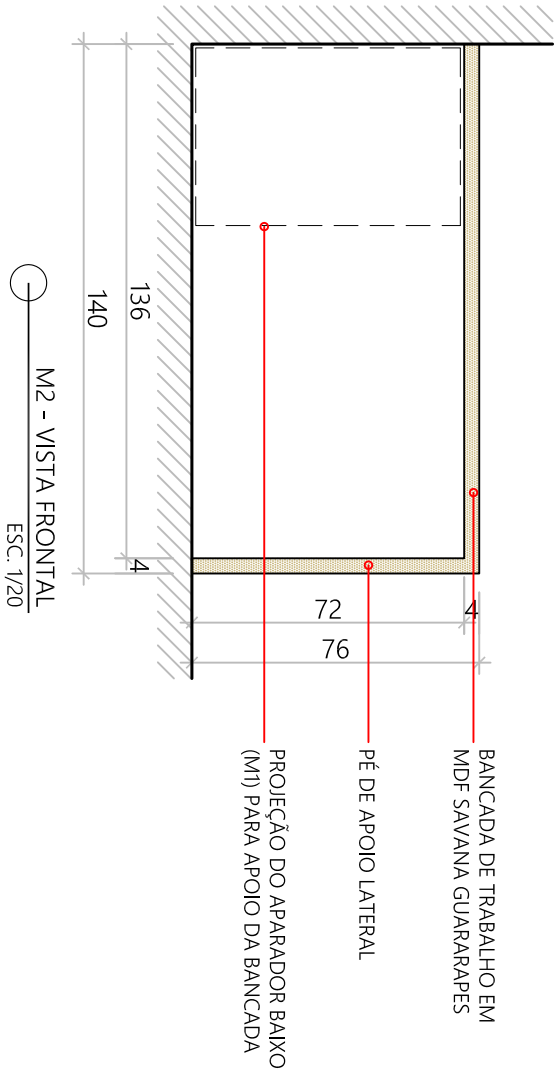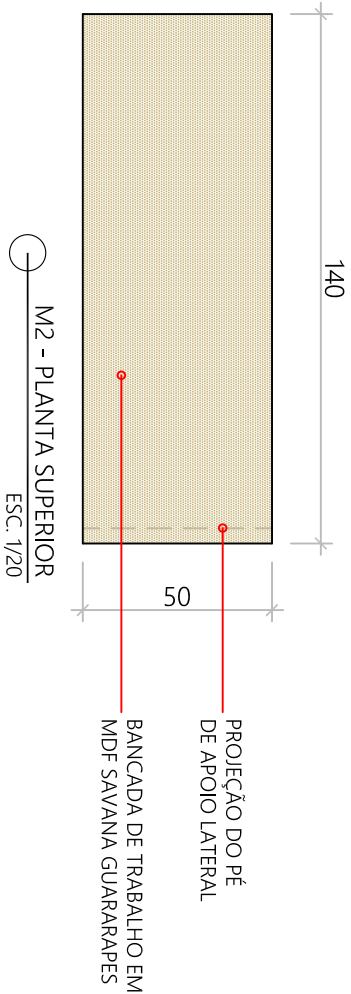

OBSERVAÇÕES:

- TODAS AS MEDIDAS DO ESPAÇO, DO MOBILIÁRIO E DOS EQUIPAMENTOS EXISTENTES DEVEM SER CONFERIDAS NO LOCAL, ANTES DA PRODUÇÃO OU FABRICAÇÃO DO CONTEÚDO DESTES PROJETO.


IONAH PINHO arquitetura & interiores 31 99113-9502 CAU: 29.315-6 ionahpinho.arquitetura@gmail.com		Projeto: ESCRITÓRIO	
Cliente: KARIAN RAMOS		Conteúdo: MARCENARIA	
Endereço: RUA SERGIPE, 440, AP:101 FUNCIONARIOS, BH/MG		Revisão: 0 Data: JUN/2026 Folha: 04	
Aprovado:			

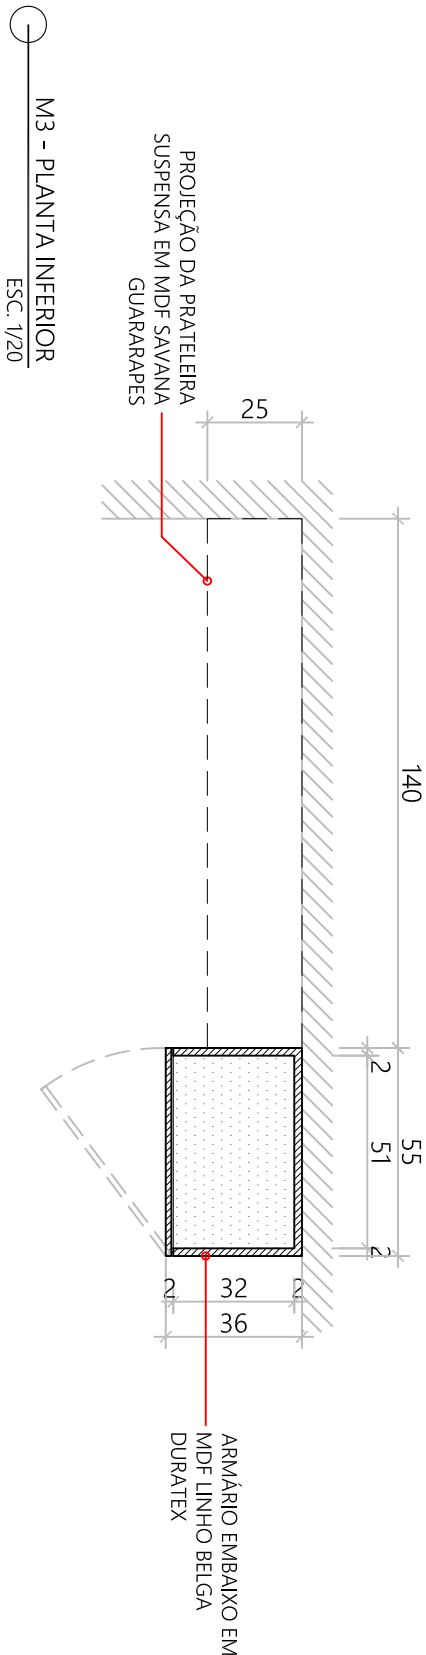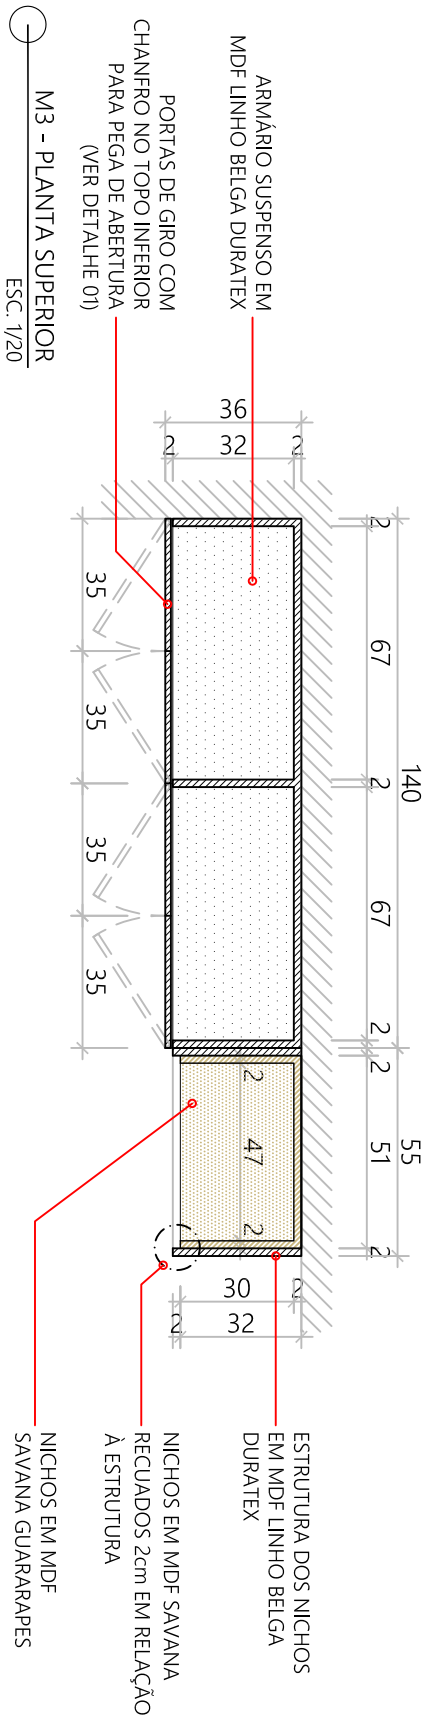

OBSERVAÇÕES:
- TODAS AS MEDIDAS DO ESPAÇO, DO MOBILIÁRIO E DOS EQUIPAMENTOS EXISTENTES DEVEM SER CONFERIDAS NO LOCAL, ANTES DA PRODUÇÃO OU FABRICAÇÃO DO CONTEÚDO DESTA PROJETO.

arquitetura & interiores
31 99113-9502 CAU: 29.315-6
ionahpinho.arquitetura@gmail.com

Cliente: KARIAN RAMOS		Projeto: ESCRITÓRIO	
Endereço: RUA SERGIPE, 440, AP:101 FUNCIONARIOS, BH/MG		Conteúdo: MARCCENARIA	
Aprovado:	Revisão: 0	Data: JUN/2026	Folha: 05

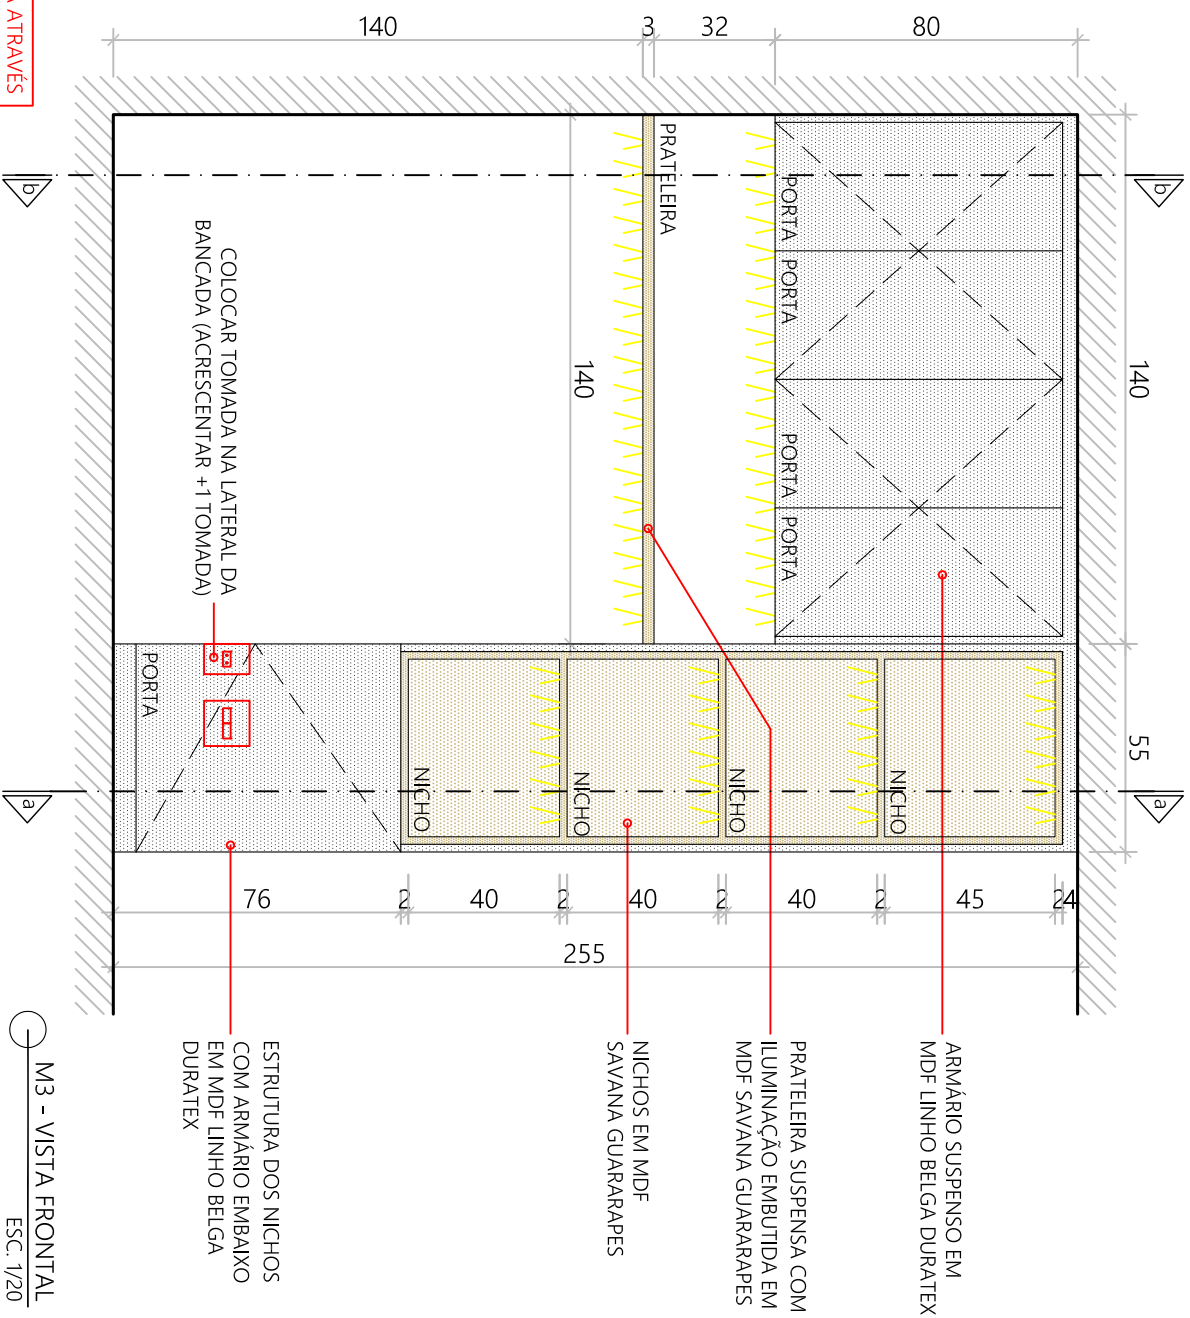


- BUSCAR ENERGIA PARA ILUMINAÇÃO EMBUTIDA ATRAVÉS DA TOMADA ATRÁS DA TORRE;
- ILUMINAÇÃO EMBUTIDA COM PERFIL METÁLICO E TAMPA ACRÍLICA)

OBSERVAÇÕES:

- TODAS AS MEDIDAS DO ESPAÇO, DO MOBILIÁRIO E DOS EQUIPAMENTOS EXISTENTES DEVEM SER CONFERIDAS NO LOCAL, ANTES DA PRODUÇÃO OU FABRICAÇÃO DO CONTEÚDO DESTE PROJETO.

IONAH PINHO arquitetura & interiores 31 99113-9502 CAU: 29.315-6 ionahpinho.arquitetura@gmail.com		Cliente:	Projeto:	
KARIAN RAMOS		ESCRITÓRIO		
Endereço:	Conteúdo:			
RUA SERGIPE, 440, AP.101 FUNCIONÁRIOS, BH/MG		MARCENARIA		
Aprovado:	Revisão: 0	Data: JUN/2026	Folha: 06	

MARCEMARIA - M3

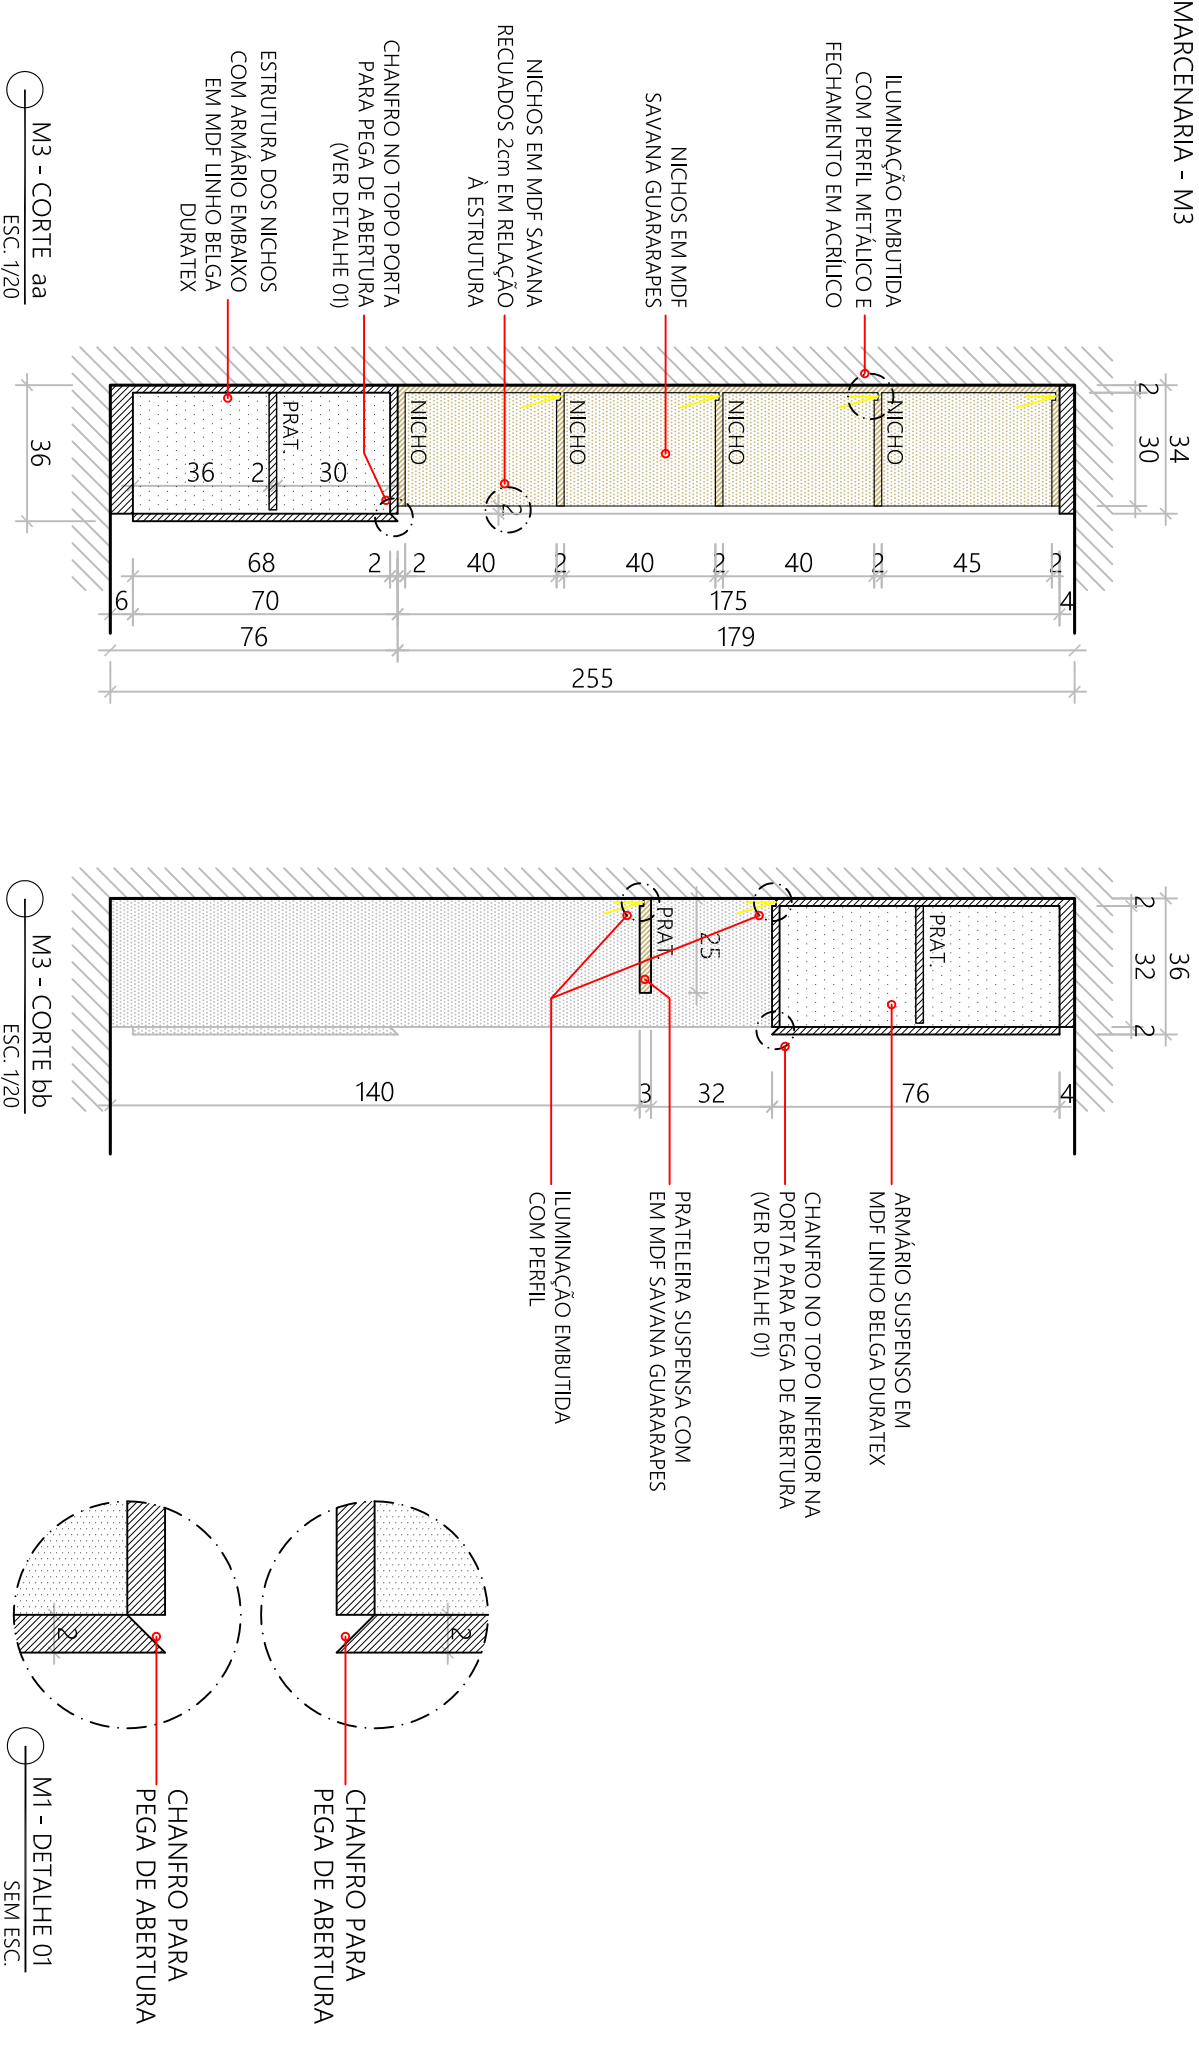

OBSERVAÇÕES:

- TODAS AS MEDIDAS DO ESPAÇO, DO MOBILIÁRIO E DOS EQUIPAMENTOS EXISTENTES DEVEM SER CONFERIDAS NO LOCAL, ANTES DA PRODUÇÃO OU FABRICAÇÃO DO CONTEÚDO DESTES PROJETO.

IONAH PINHO

arquitetura & interiores
31 99113-9502 CAU: 29.315-6
ionahpinho.arquitetura@gmail.com

Cliente:
KARIAN RAMOS

Projeto:
ESCRITÓRIO

Endereço:
RUA SERGIPE, 440, AP.101
FUNCIONÁRIOS, BH/MG



Conteúdo:
MARCEMARIA

Aprovado:

Revisão: 0

Data: JUN/2026

Folha: 07

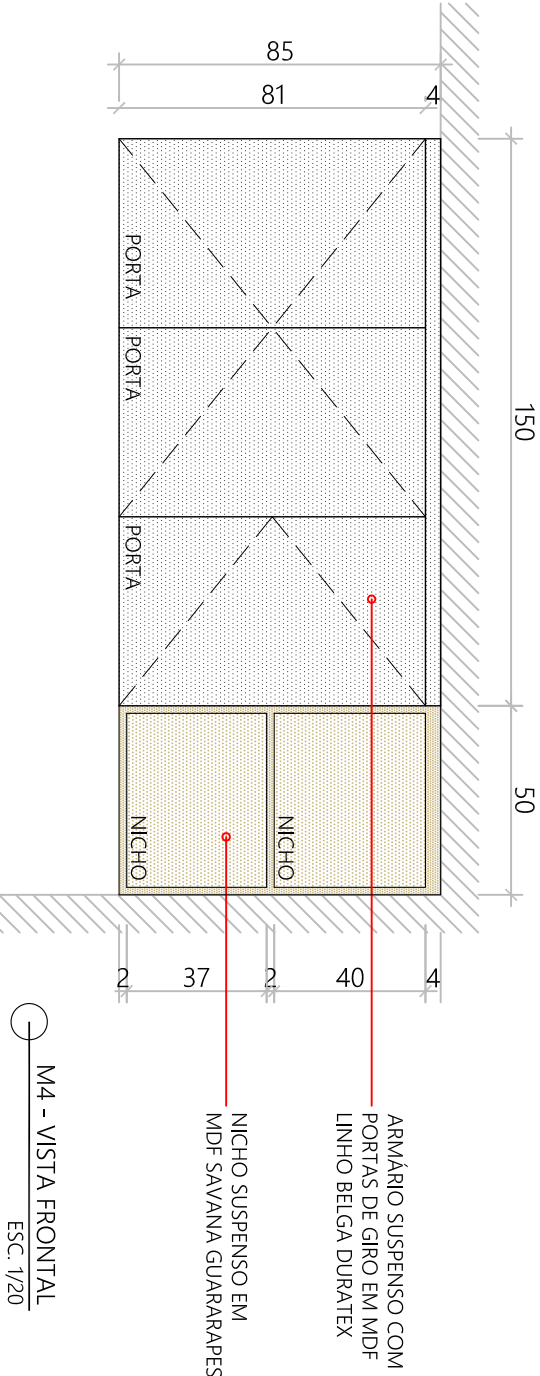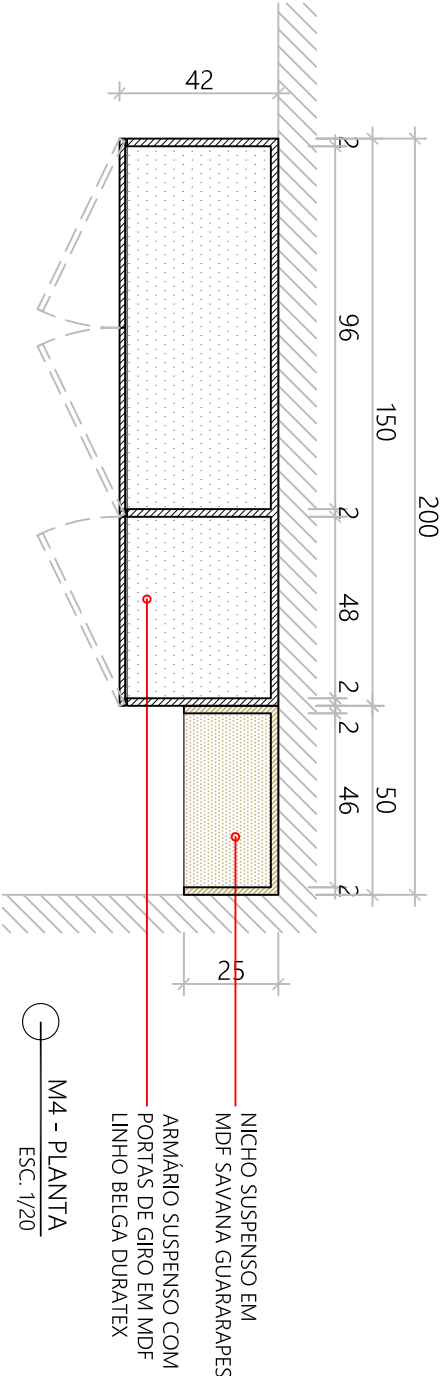

OBSERVAÇÕES:
- TODAS AS MEDIDAS DO ESPAÇO, DO MOBILIÁRIO E DOS EQUIPAMENTOS EXISTENTES DEVEM SER CONFERIDAS NO LOCAL, ANTES DA PRODUÇÃO OU FABRICAÇÃO DO CONTEÚDO DESTES PROJETO.

IONAH PINHO arquitetura & interiores 31 99113-9502 CAU: 29.315-6 ionahpinho.arquitetura@gmail.com		Projeto: ESCRITÓRIO	
Cliente: KARIAN RAMOS		Conteúdo: MARCENARIA	
Endereço: RUA SERGIPE, 440, AP:101 FUNCIONARIOS, BH/MG		Revisão: 0 Data: JUN/2026 Folha: 08	
Aprovado:			